

5

4

3

2

1

C


C

B

B

A

A

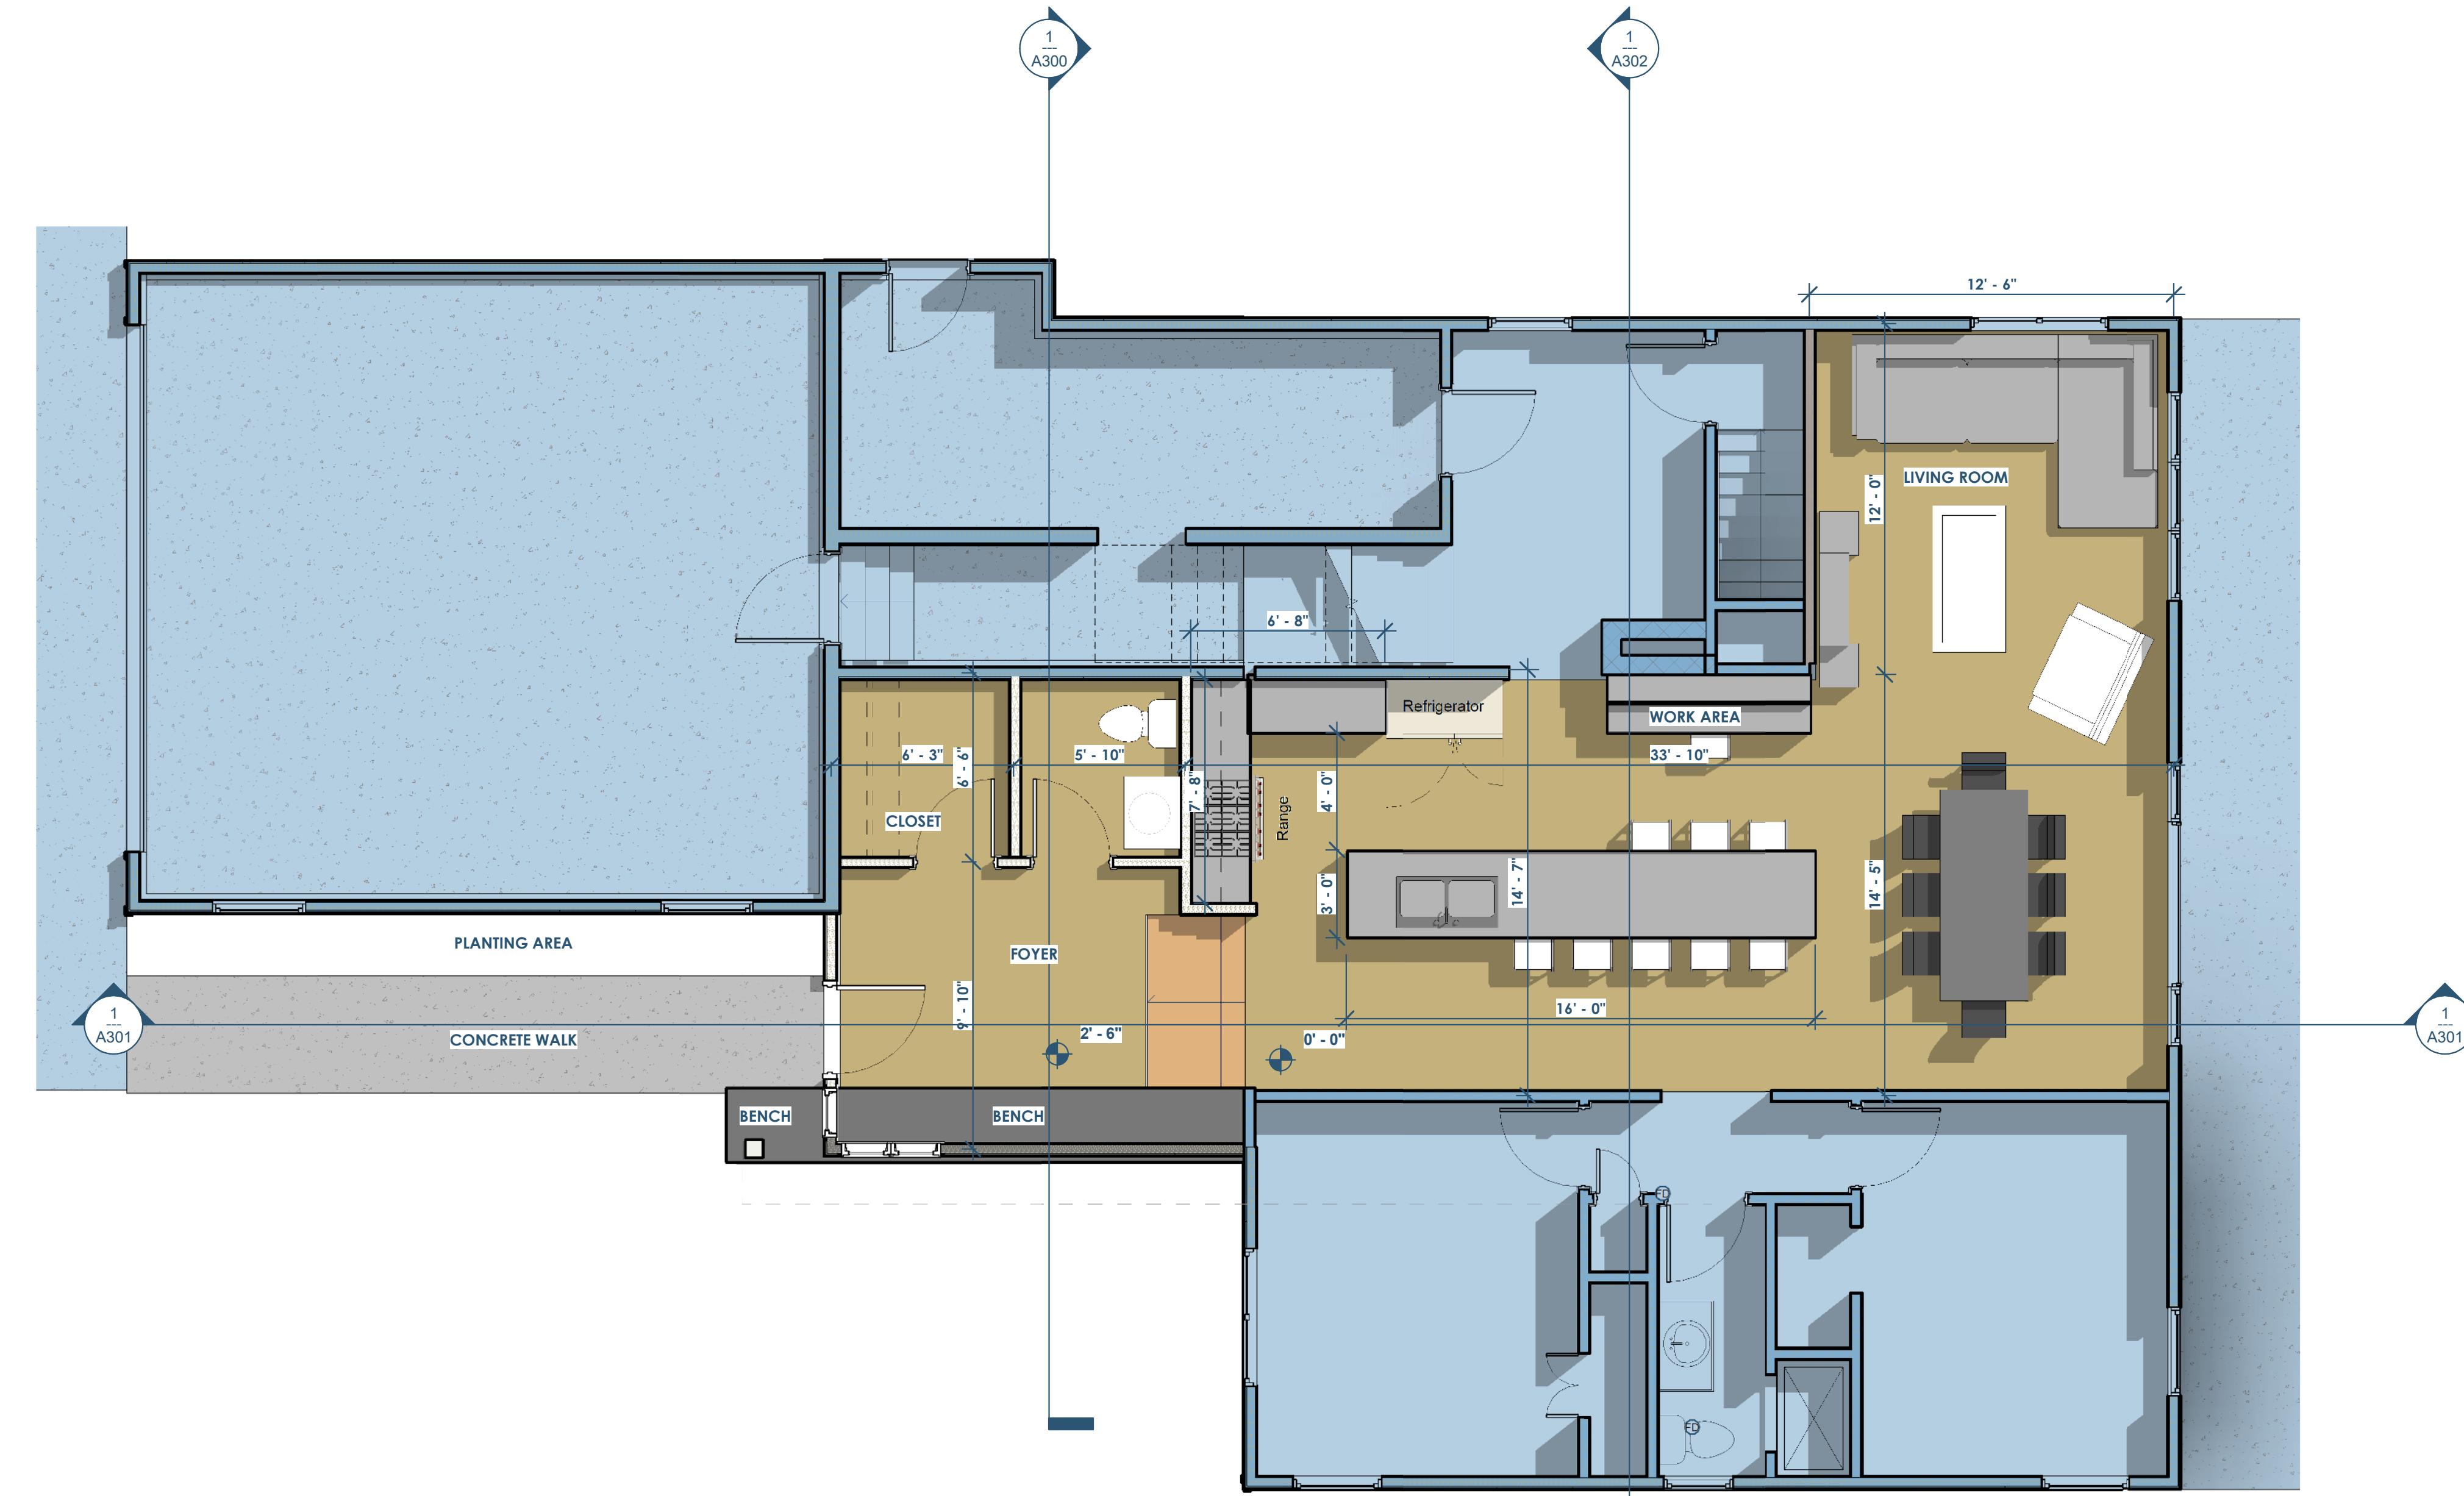

(1) FLOOR PLAN - 1ST  
1/4" = 1'-0"



Architect: OpeningDesign  
316 W Washington Ave | Suite 675  
Madison, WI 53703  
ryan@openingdesign.com | 773.425.6456

FLOOR PLAN - 1ST FLOOR - 07/17/2019  
KERN RESIDENCE  
N6790 SHOREWOOD HILLS RD - LAKE MILLS, WI 53551

A101

5

4

3

2

1

5

4

3

2

1

C

C

B

B

A


A

① FLOOR PLAN - ROOF  
1/4" = 1'-0"



Architect: OpeningDesign  
316 W Washington Ave | Suite 675  
Madison, WI 53703  
ryan@openingdesign.com | 773.425.6456

FLOOR PLAN - ROOF - 07/17/2019  
KERN RESIDENCE  
N6790 SHOREWOOD HILLS RD - LAKE MILLS, WI 53551  
A102

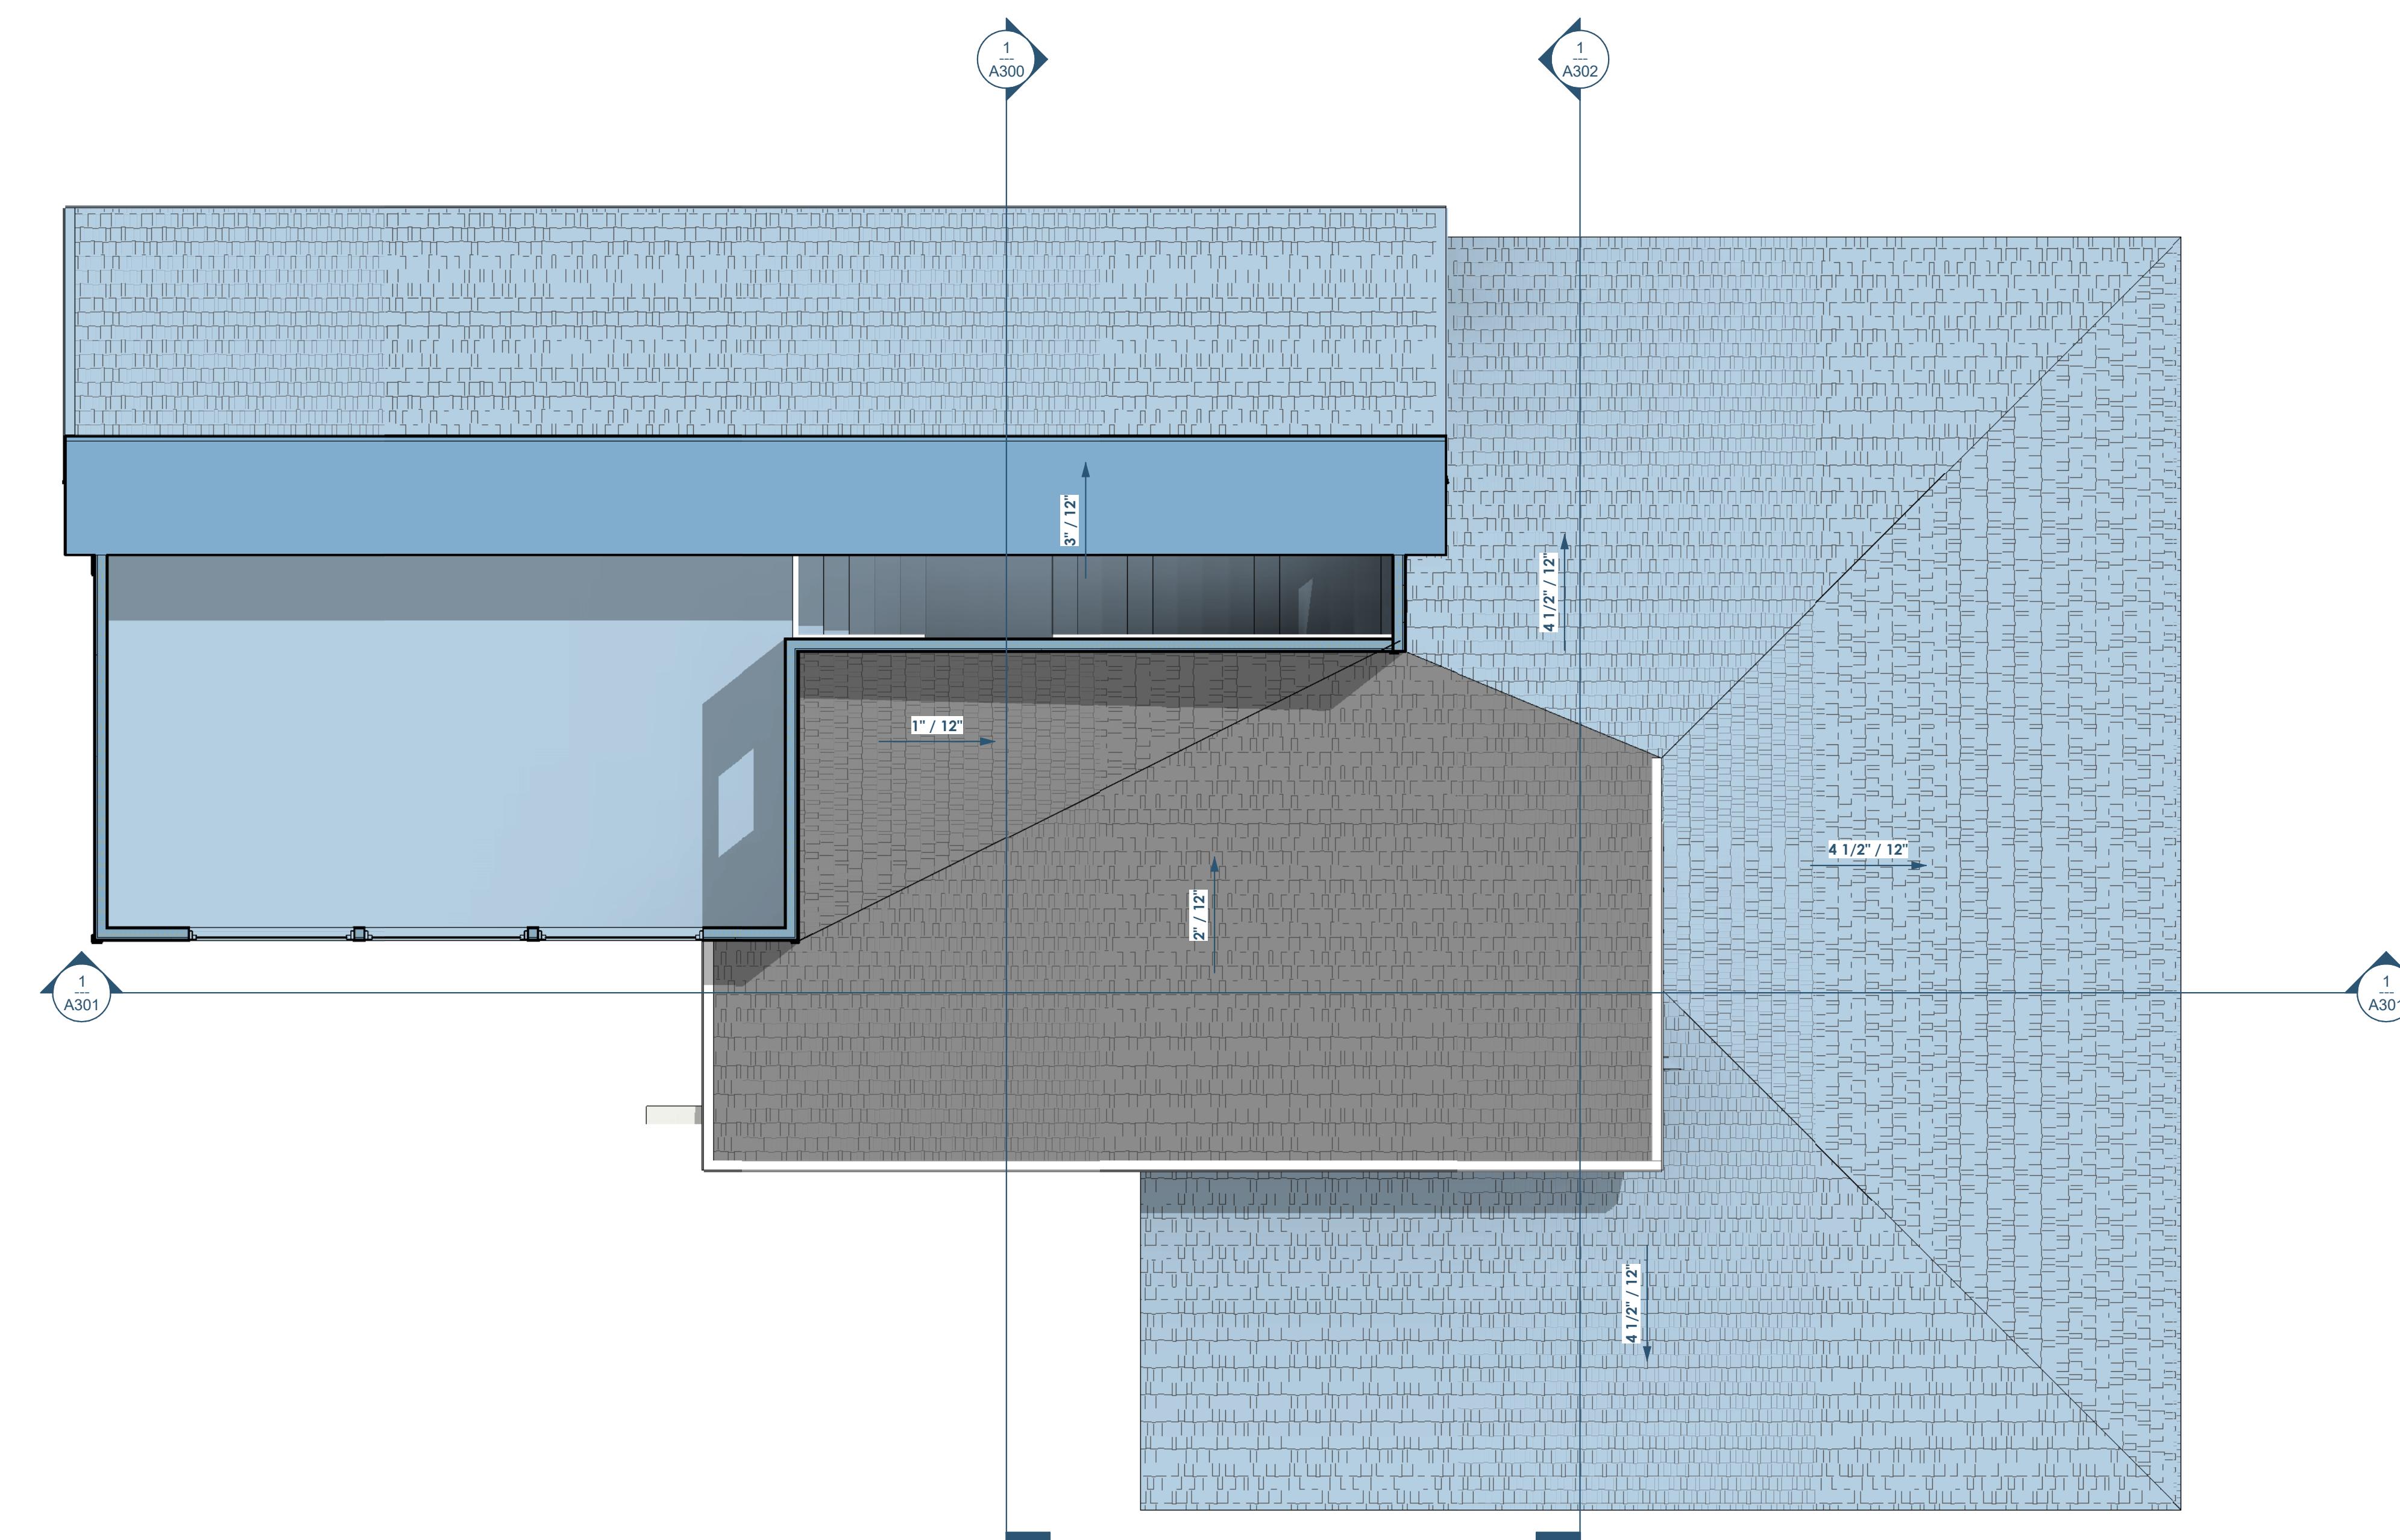

5

4

3

2

1

C


C

B

B

A

A

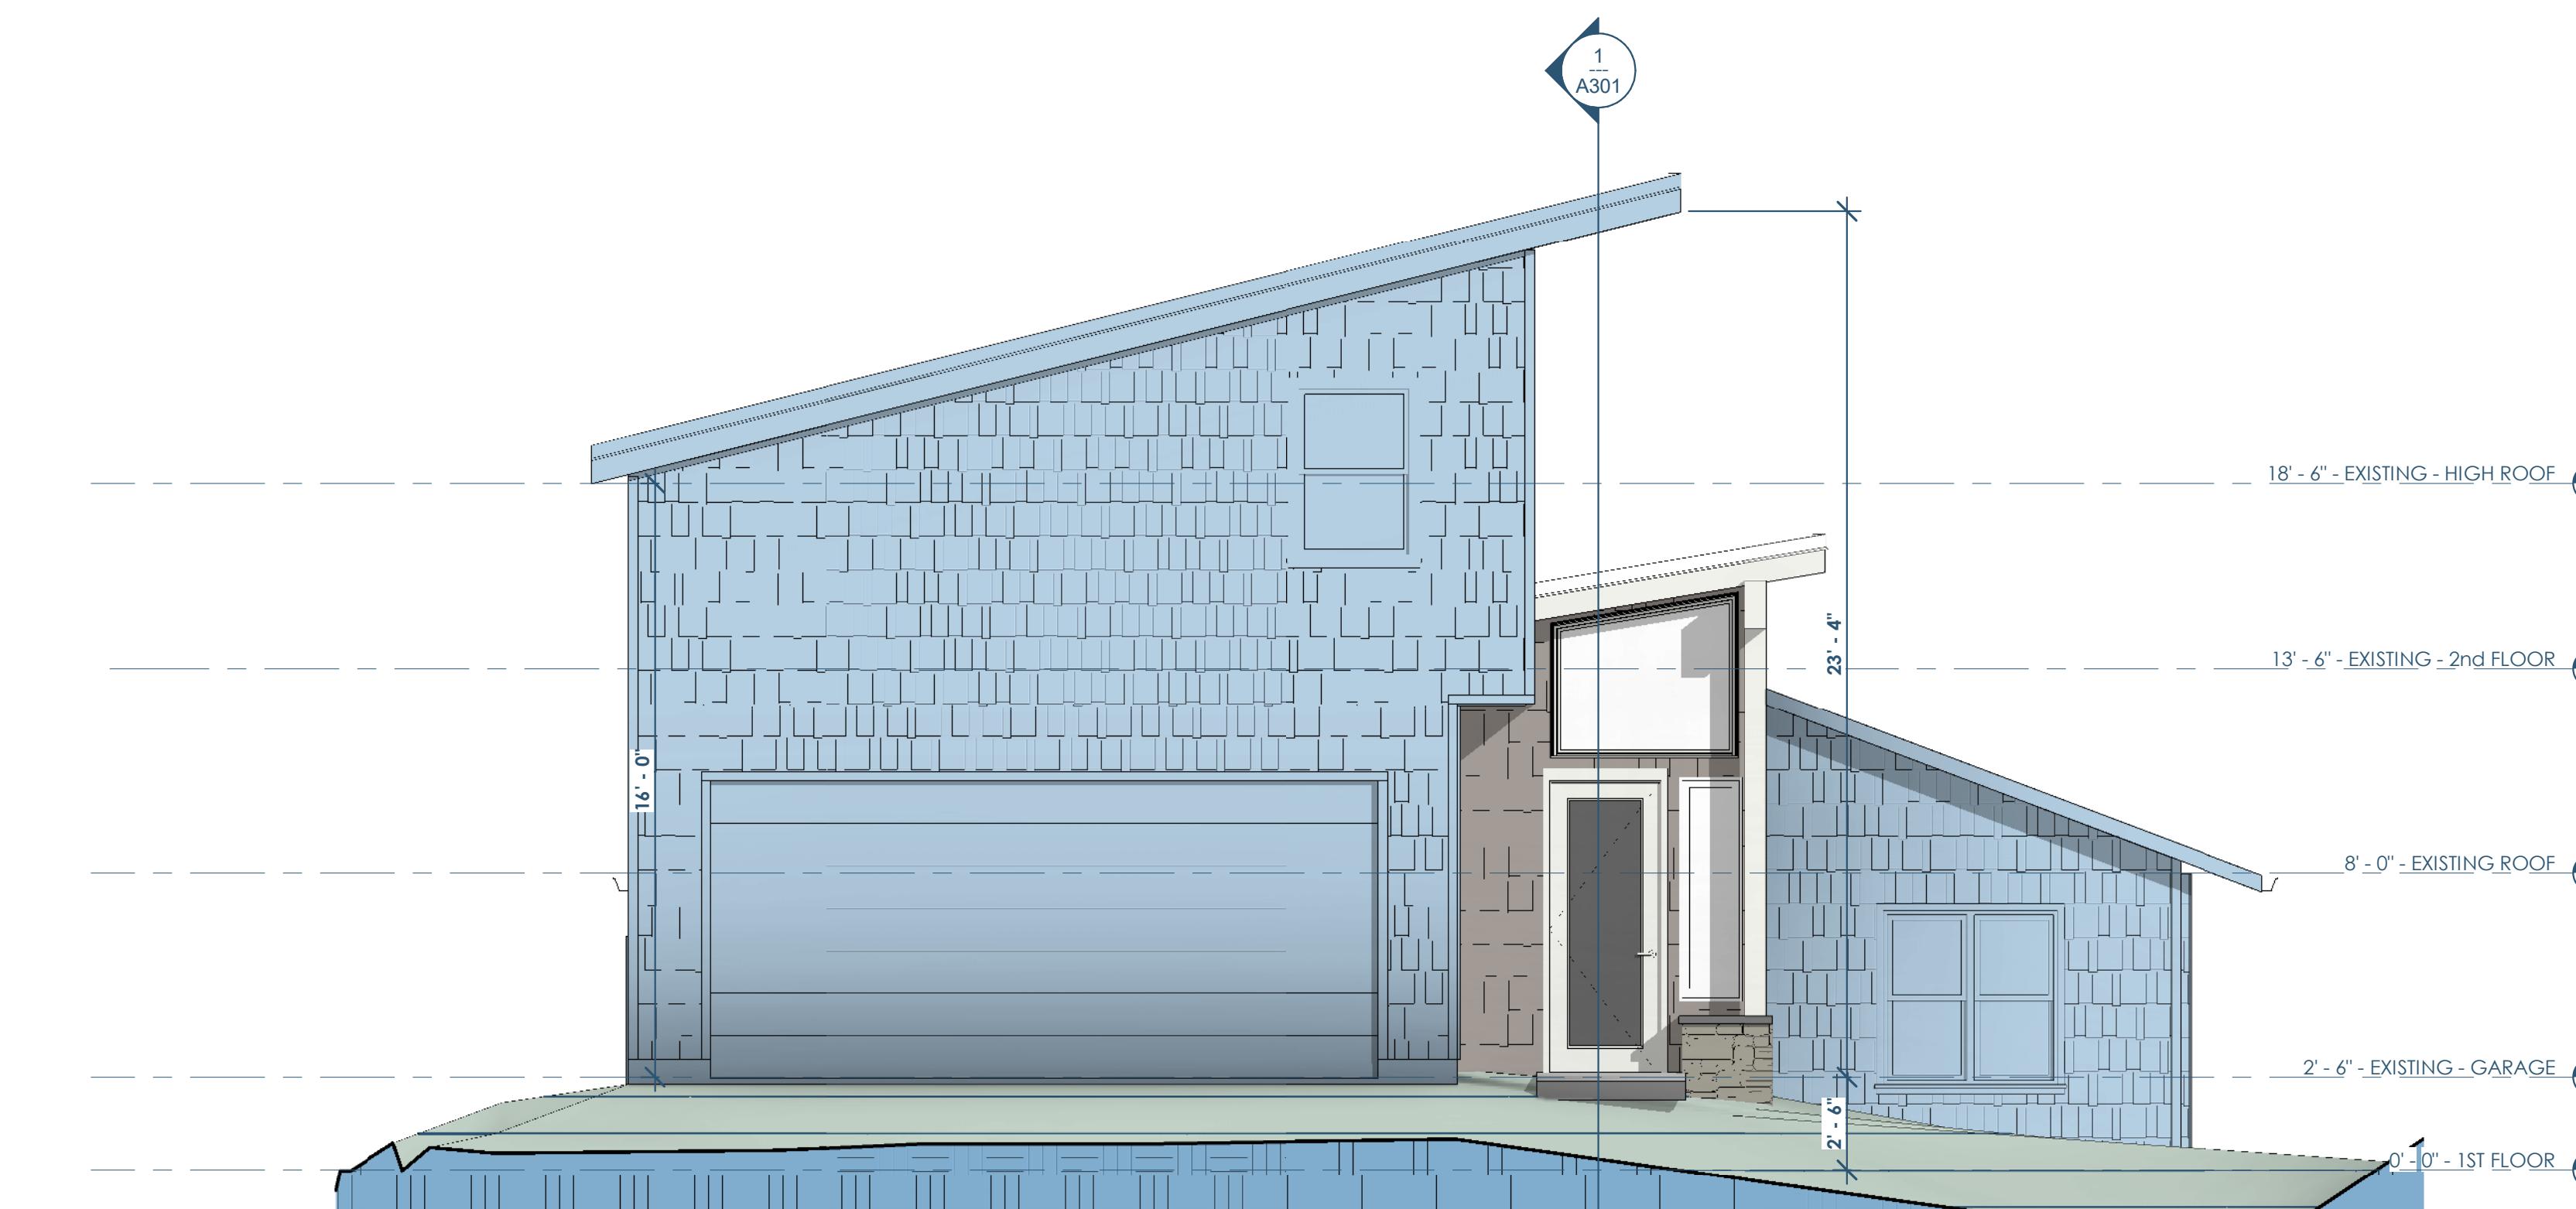

① PROPOSED WEST ELEVATION  
1/4" = 1'-0"

0' 2' 4' 8'



Architect: OpeningDesign  
316 W Washington Ave | Suite 675  
Madison, WI 53703  
ryan@openingdesign.com | 773.425.6456

BUILDING ELEVATIONS - 07/17/2019  
KERN RESIDENCE  
N6790 SHOREWOOD HILLS RD - LAKE MILLS, WI 53551  
A200

5

4

3

2

1

5

4


3

2

1

C

C

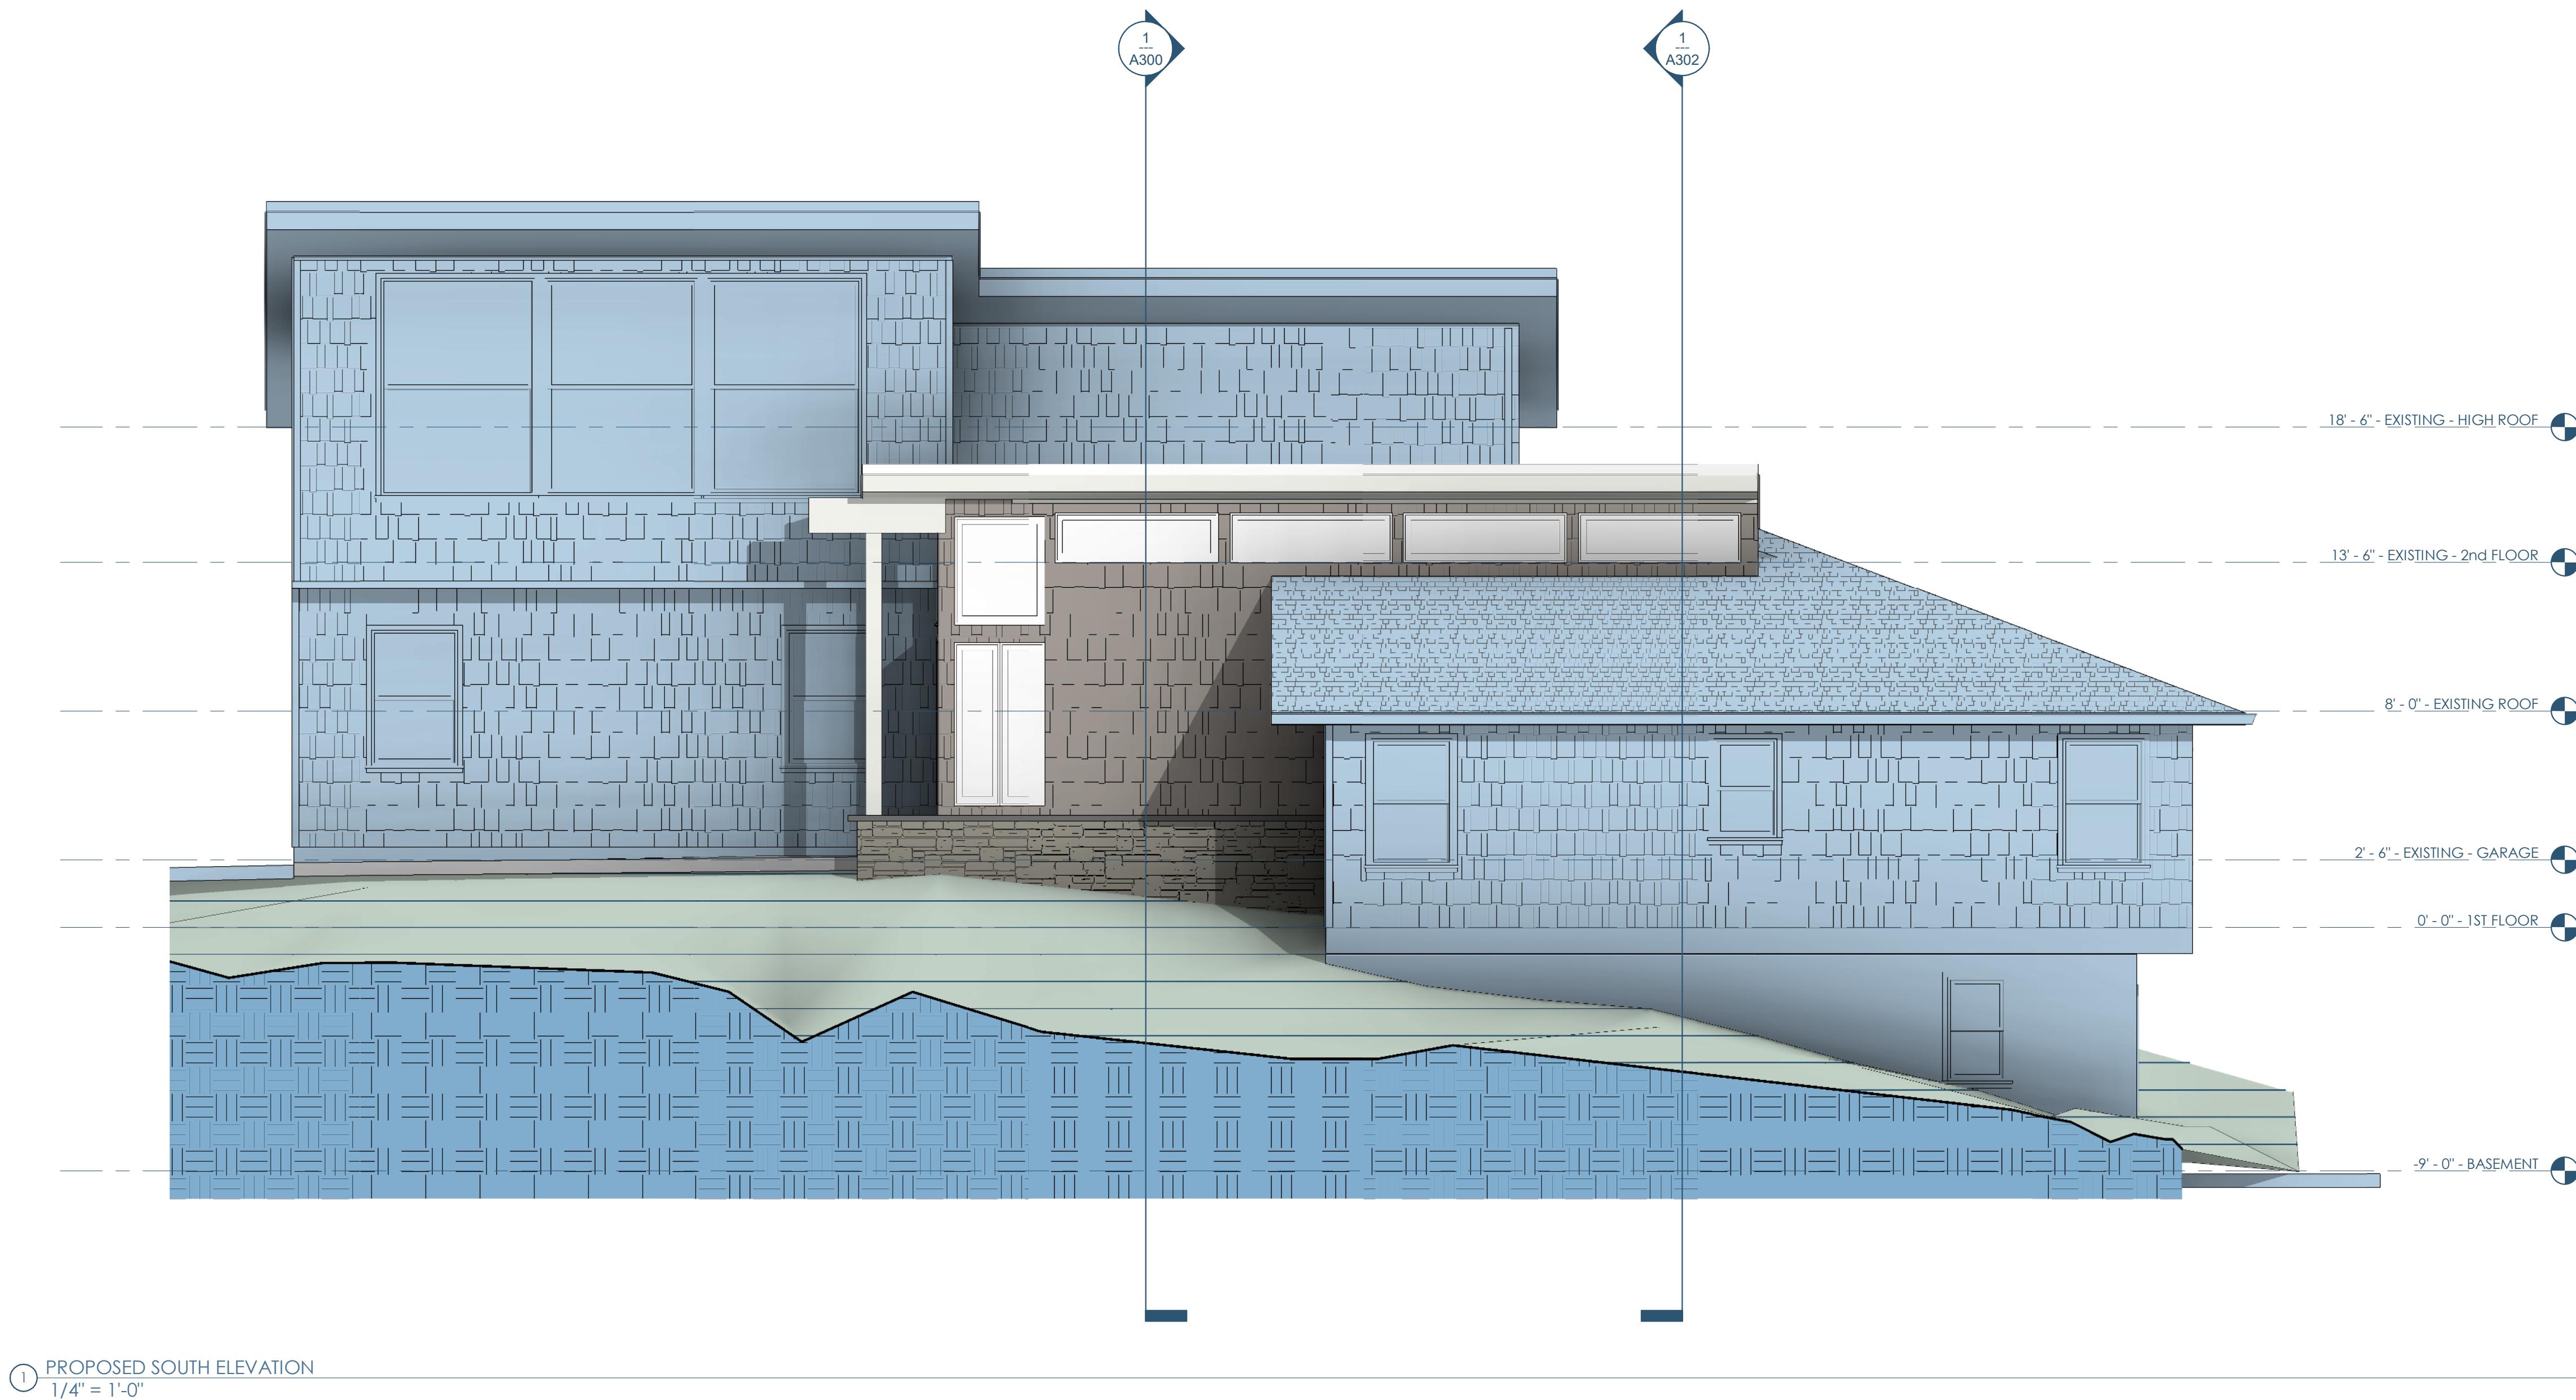

0 2' 4' 8'



Architect: OpeningDesign  
316 W Washington Ave | Suite 675  
Madison, WI 53703  
ryan@openingdesign.com | 773.425.6456

BUILDING ELEVATIONS - 07/17/2019  
KERN RESIDENCE  
N6790 SHOREWOOD HILLS RD - LAKE MILLS, WI 53551

A201

5

4

3


2

1

5 4 3 2 1

C

C

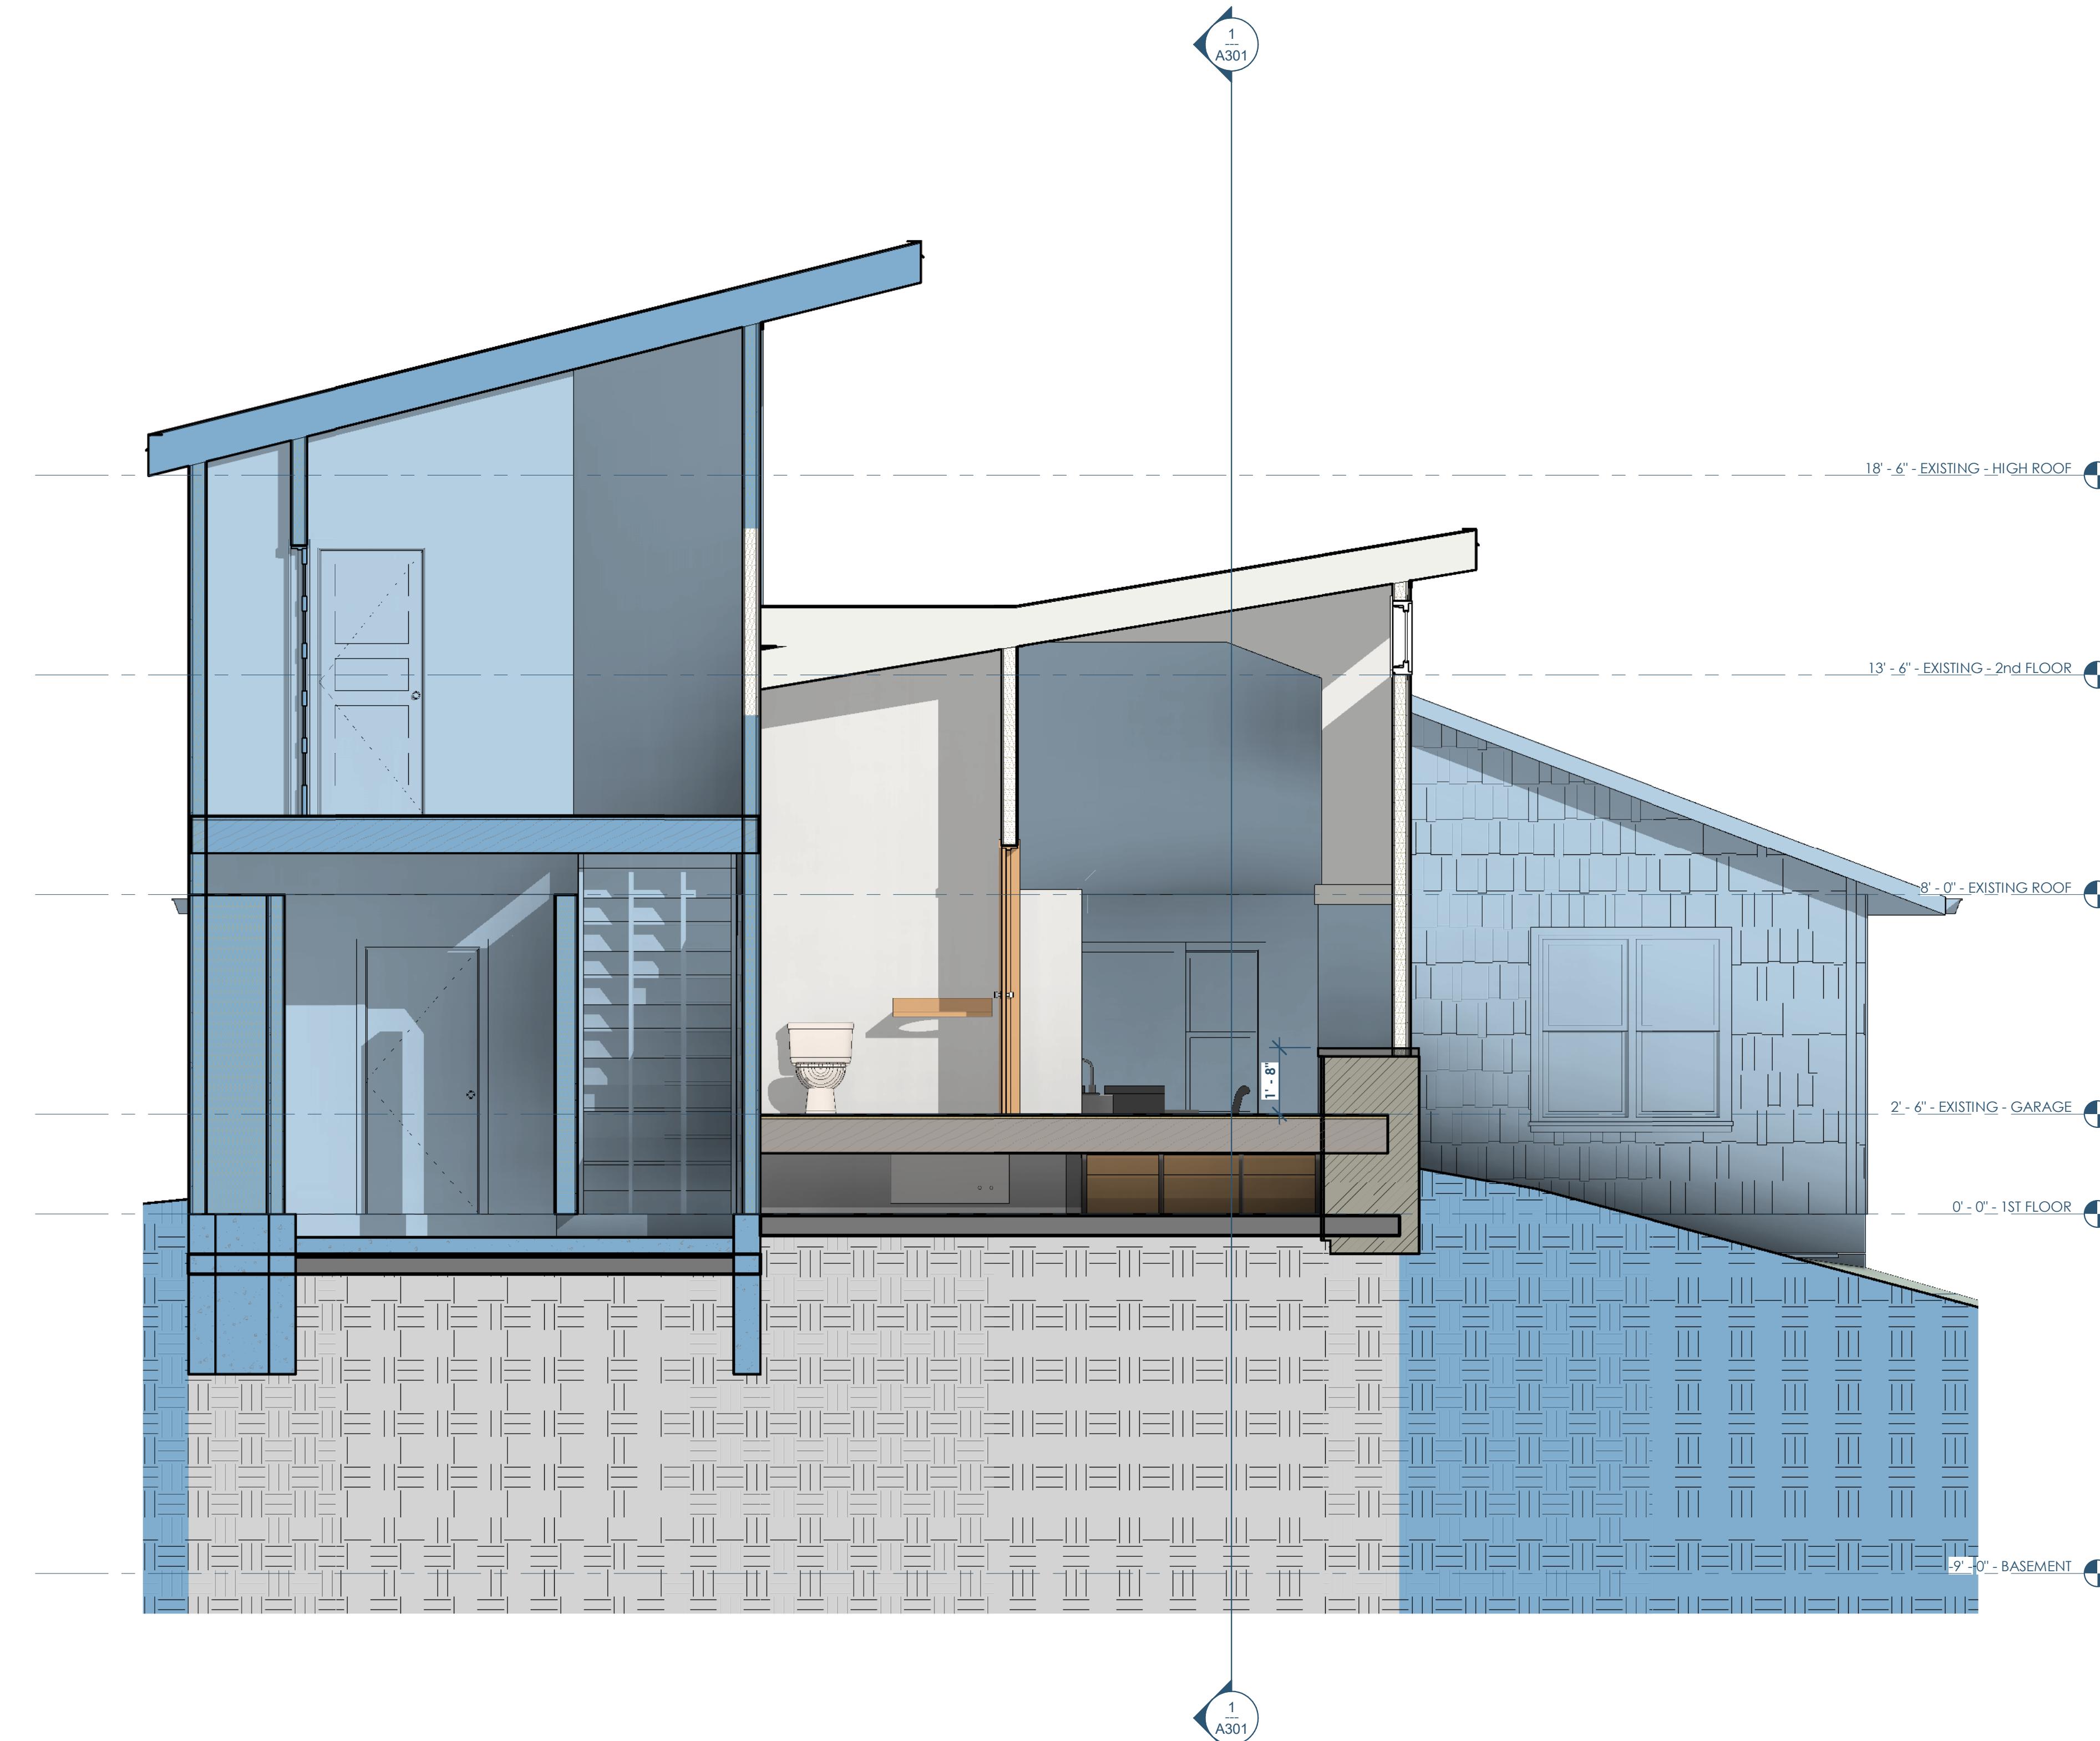

SECTION 1  
3/8" = 1'-0"

0 2' 4' 6'

BUILDING SECTION - 07/17/2019

KERN RESIDENCE

N6790 SHOREWOOD HILLS RD - LAKE MILLS, WI 53551

A300



5 4 3 2 1

C


C

B

B

A

A

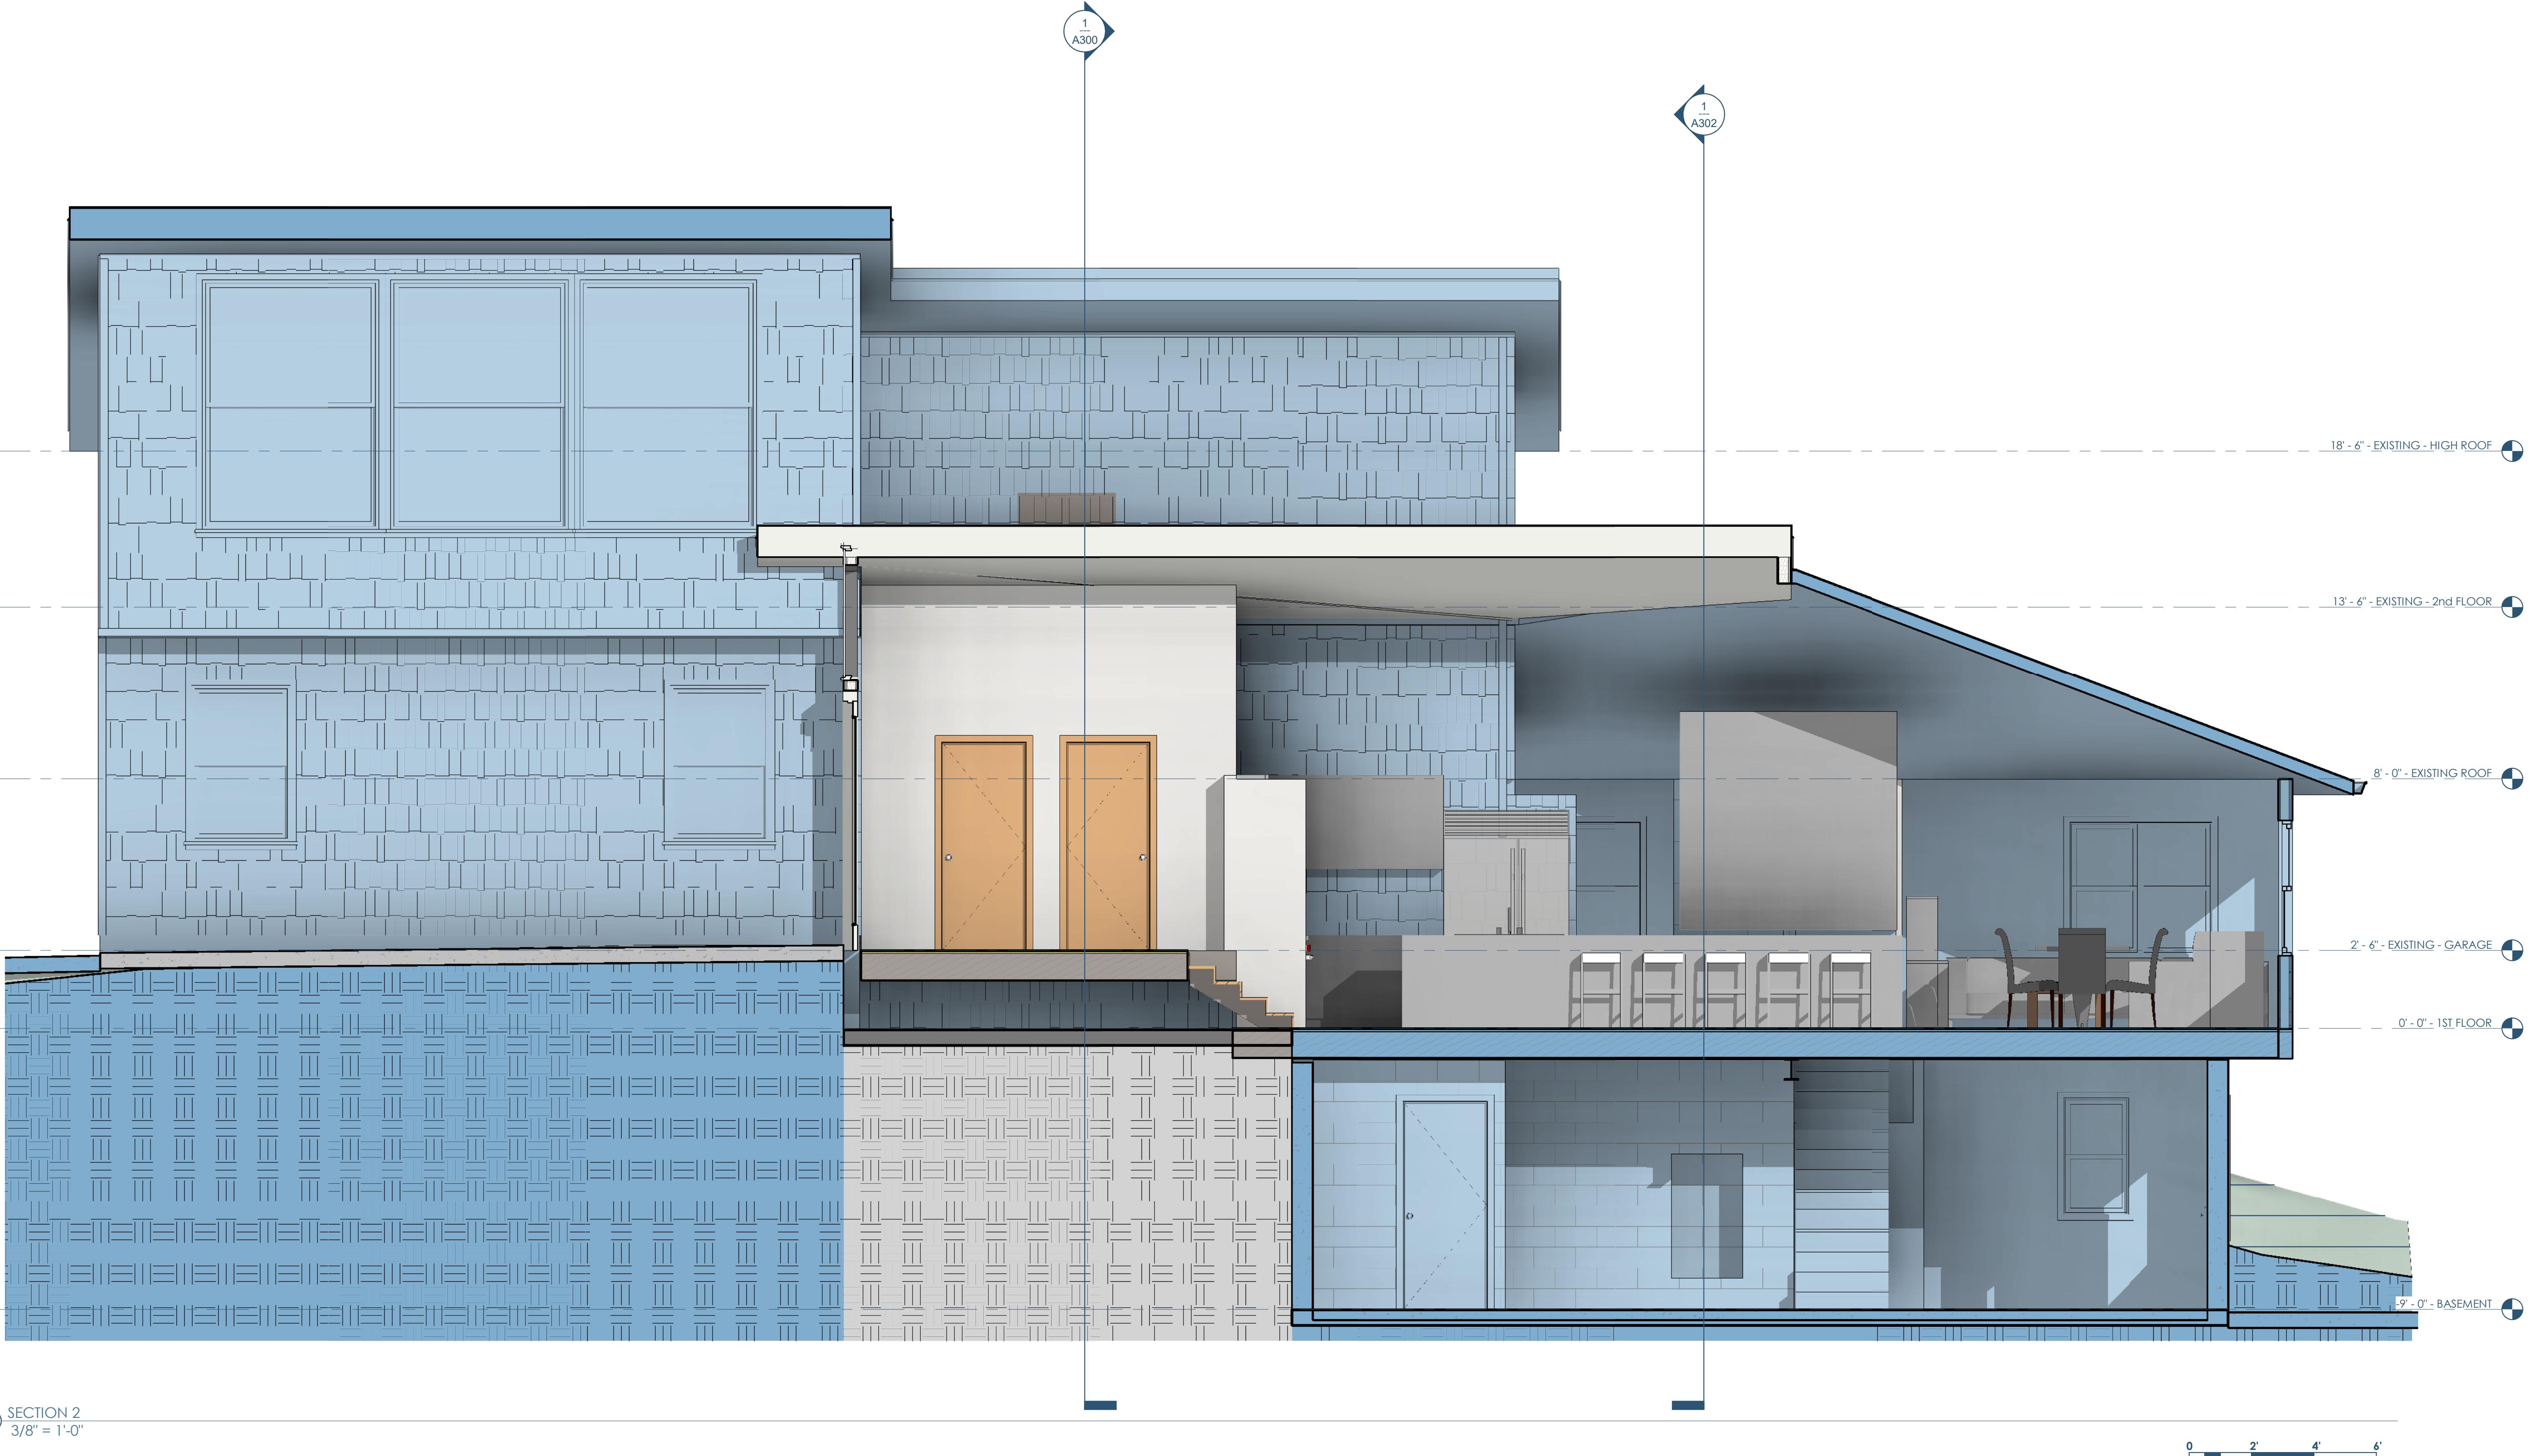

5 4 3 2 1

C


C

B

B

A

A

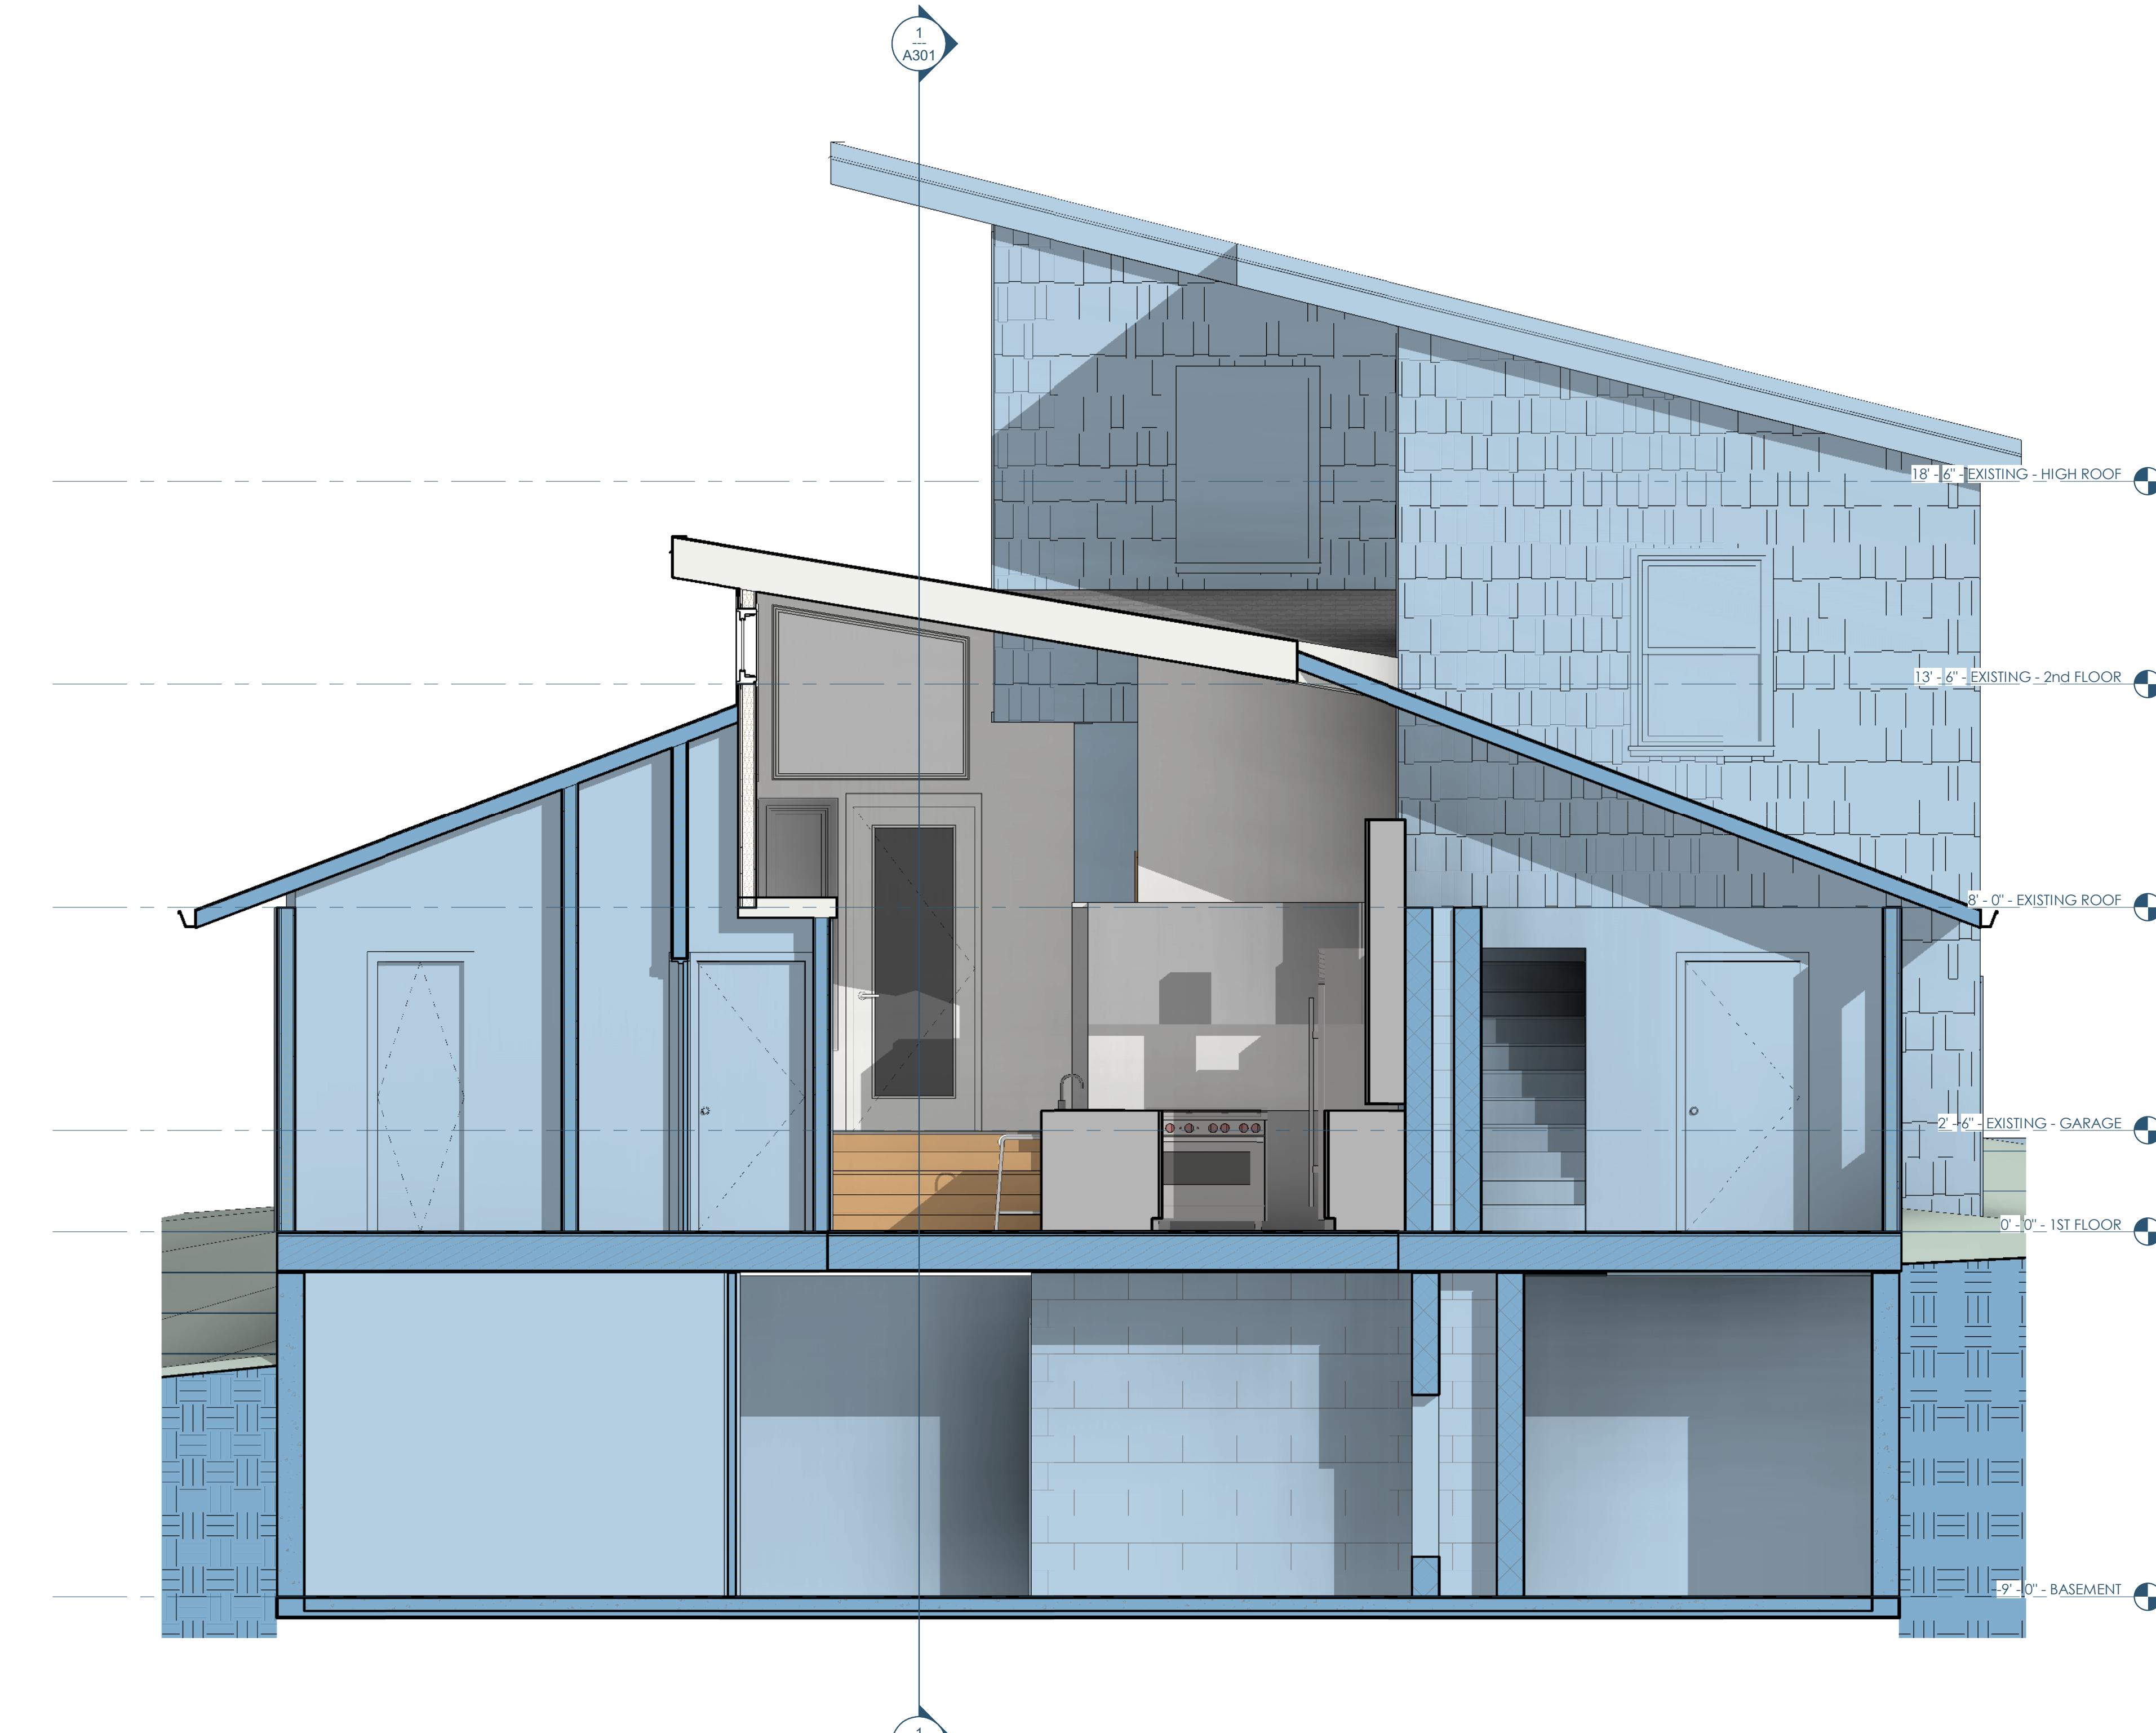

SECTION 3  
1/8" = 1'-0"

0 2' 4' 6'



Architect: OpeningDesign  
316 W Washington Ave | Suite 675  
Madison, WI 53703  
ryan@openingdesign.com | 773.425.6456

BUILDING SECTION - 07/17/2019  
KERN RESIDENCE  
N6790 SHOREWOOD HILLS RD - LAKE MILLS, WI 53551  
A302