


(1) SITE/LOCATION PLAN
1" = 20'-0"

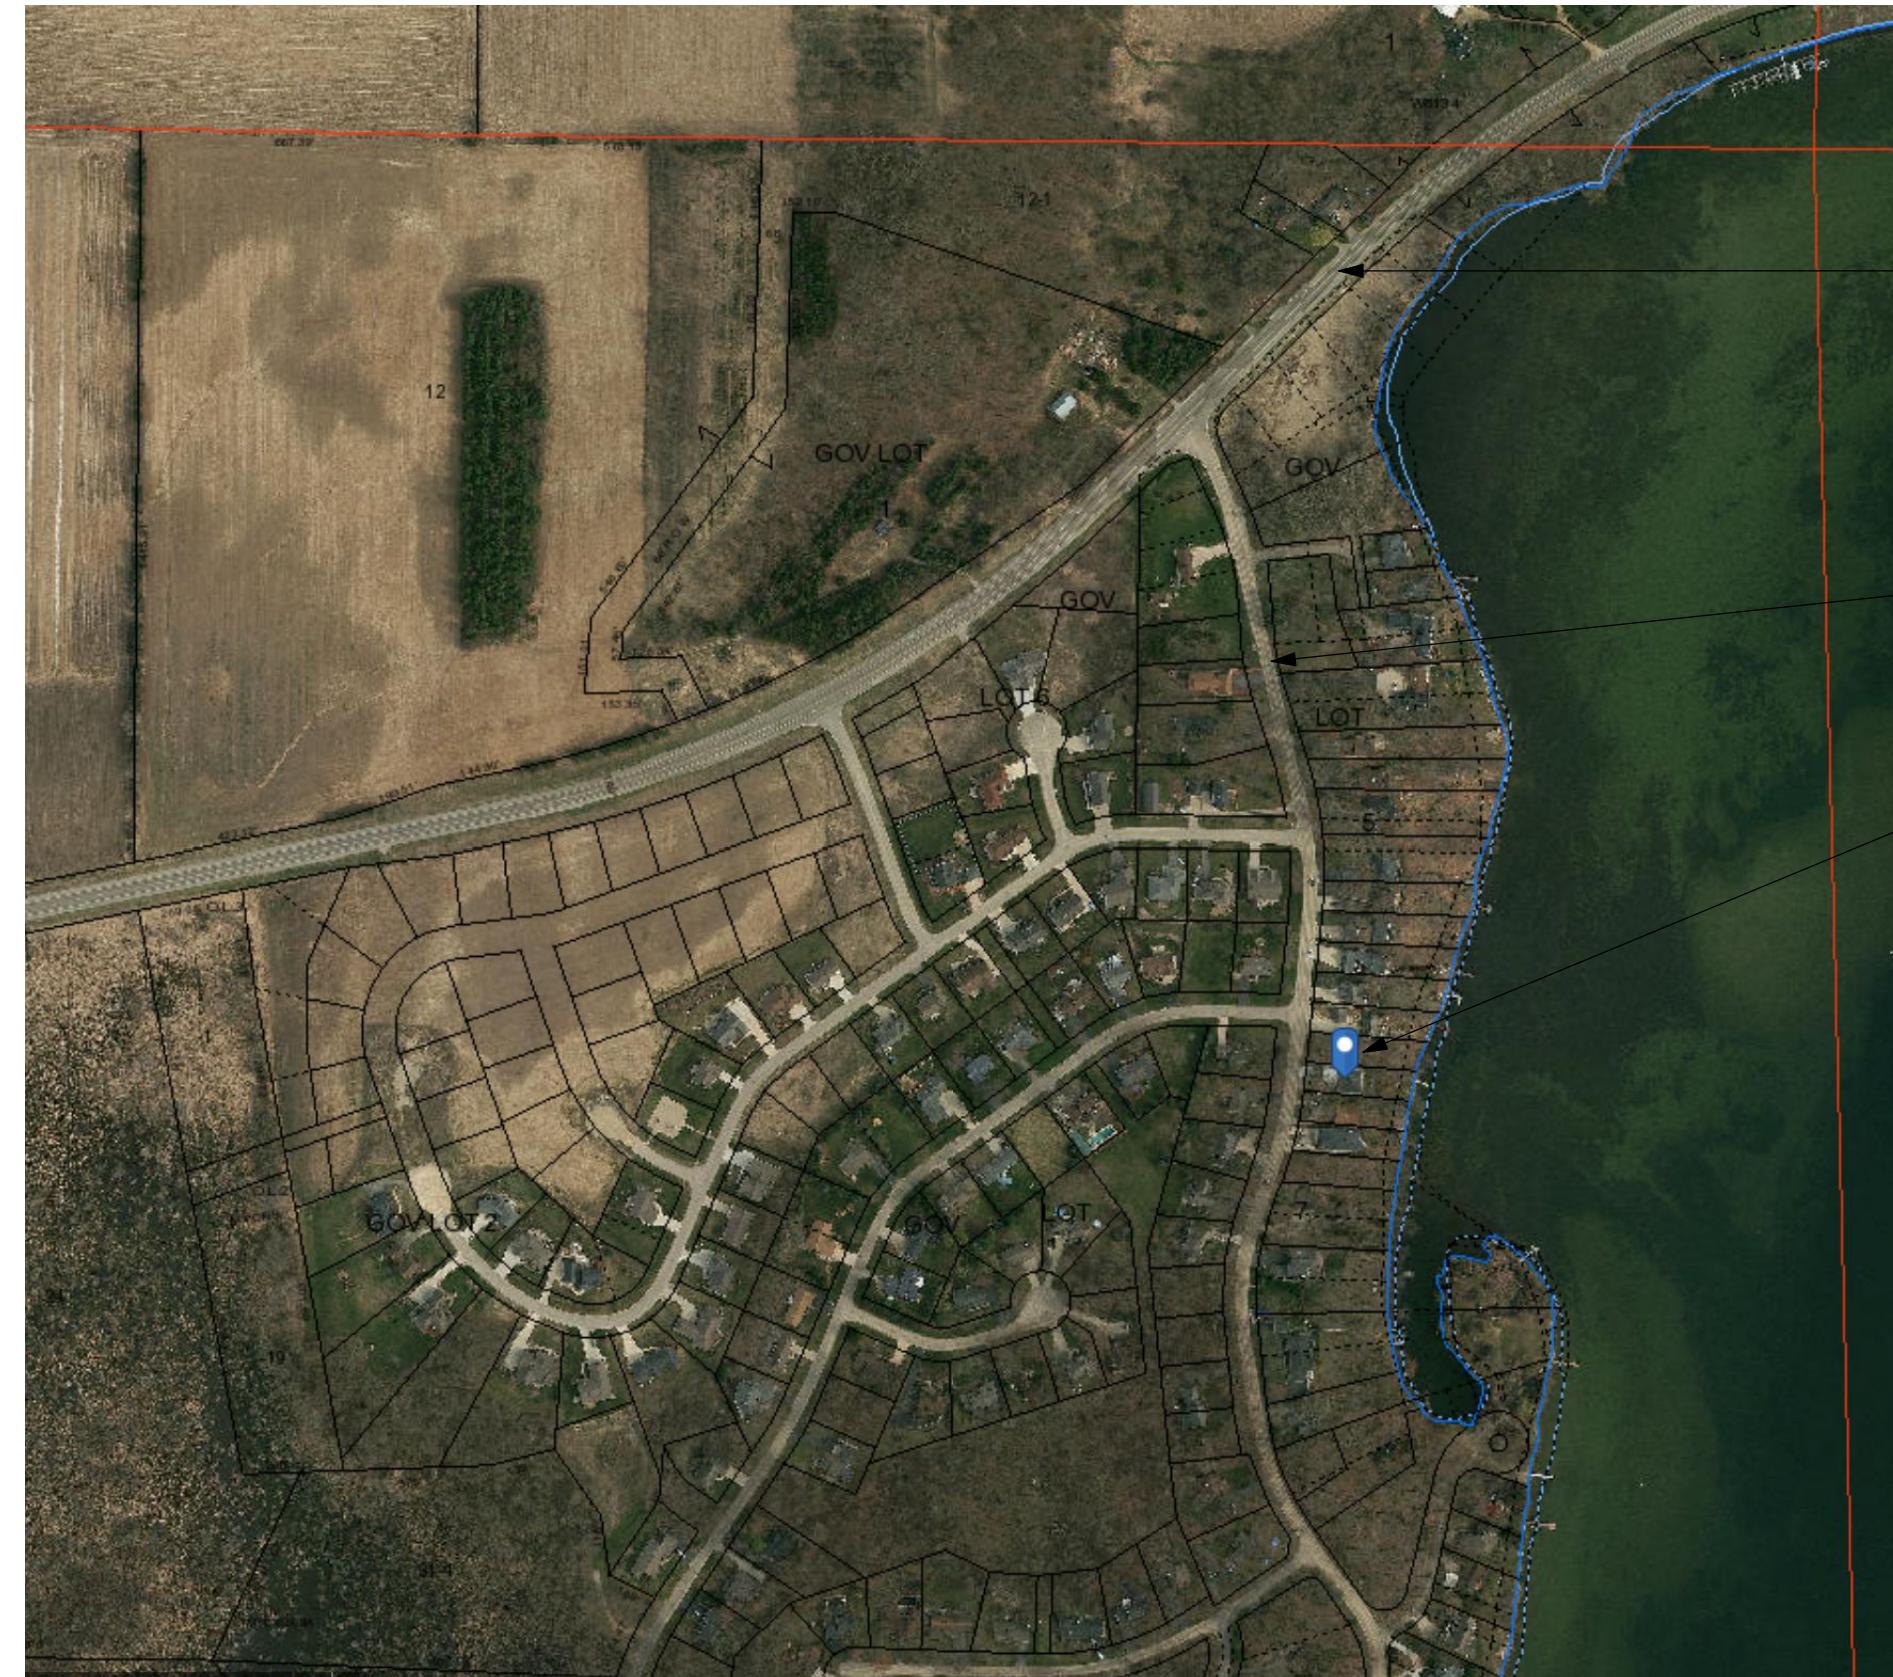

(2) LOCATION MAP

SHEET LIST - PERMIT SET	
Sheet Number	Sheet Name
C001	COVER SHEET, PROJECT INFORMATION
AE100	EXISTING BASEMENT PLAN
AE101	EXISTING FIRST (MAIN) FLOOR PLAN
AE102	EXISTING UPPER LEVEL FLOOR PLAN
AE103	EXISTING OVERALL ROOF PLAN
AD101	DEMOLITION FIRST (MAIN) FLOOR PLAN
AD102	DEMOLITION ROOF PLAN
S101	STRUCTURAL GENERAL NOTES & FOUNDATION PLAN
S102	STRUCTURAL FRAMING PLANS
A101	PROPOSED OVERALL FIRST FLOOR PLAN
A102	PROPOSED OVERALL UPPER FLOOR PLAN
A103	PROPOSED OVERALL ROOF PLAN
A200	BUILDING ELEVATIONS
A201	BUILDING ELEVATIONS
A202	BUILDING ELEVATIONS
A203	BUILDING ELEVATIONS
A300	BUILDING SECTION
A301	BUILDING SECTION
A302	BUILDING SECTION
A310	WALL SECTIONS
A450	INTERIOR ELEVATIONS
A451	INTERIOR ELEVATIONS
A500	ARCHITECTURAL DETAILS
A600	SCHEDULES, DOOR AND WINDOW TYPES

SITE AND BUILDING DATA:

EXISTING BUILDING SQUARE FOOTAGE:

PROPOSED SQUARE FOOTAGE:
REMODELED AREA:

EXISTING SITE AREA/SQUARE FOOTAGE:

BUILDING HEIGHT CRITERIA:

BUILDING CODE INFORMATION:

COVER SHEET, PROJECT INFORMATION - 08/16/2019

KERN RESIDENCE

N6790 SHOREWOOD HILLS RD - LAKE MILLS, WI 53551

C001

5

4

3

2

1

C

C

B

B

A

A



EXISTING - BASEMENT FLOOR PLAN
1/4" = 1'-0"

0 2' 4' 8'



Architect: OpeningDesign
316 W Washington Ave | Suite 675
Madison, WI 53703
ryan@openingdesign.com | 773.425.6456

EXISTING BASEMENT PLAN - 08/16/2019
KERN RESIDENCE
N6790 SHOREWOOD HILLS RD - LAKE MILLS, WI 53551 AE100

5

4

3

2

1

5

4

3

2

1



① EXISTING - 1ST FLOOR PLAN
1/4" = 1'-0"



EXISTING FIRST (MAIN) FLOOR PLAN - 08/16/2019
KERN RESIDENCE
N6790 SHOREWOOD HILLS RD - LAKE MILLS, WI 53551 AE101

5

4

3

2

1

C


C

B

B

A

A

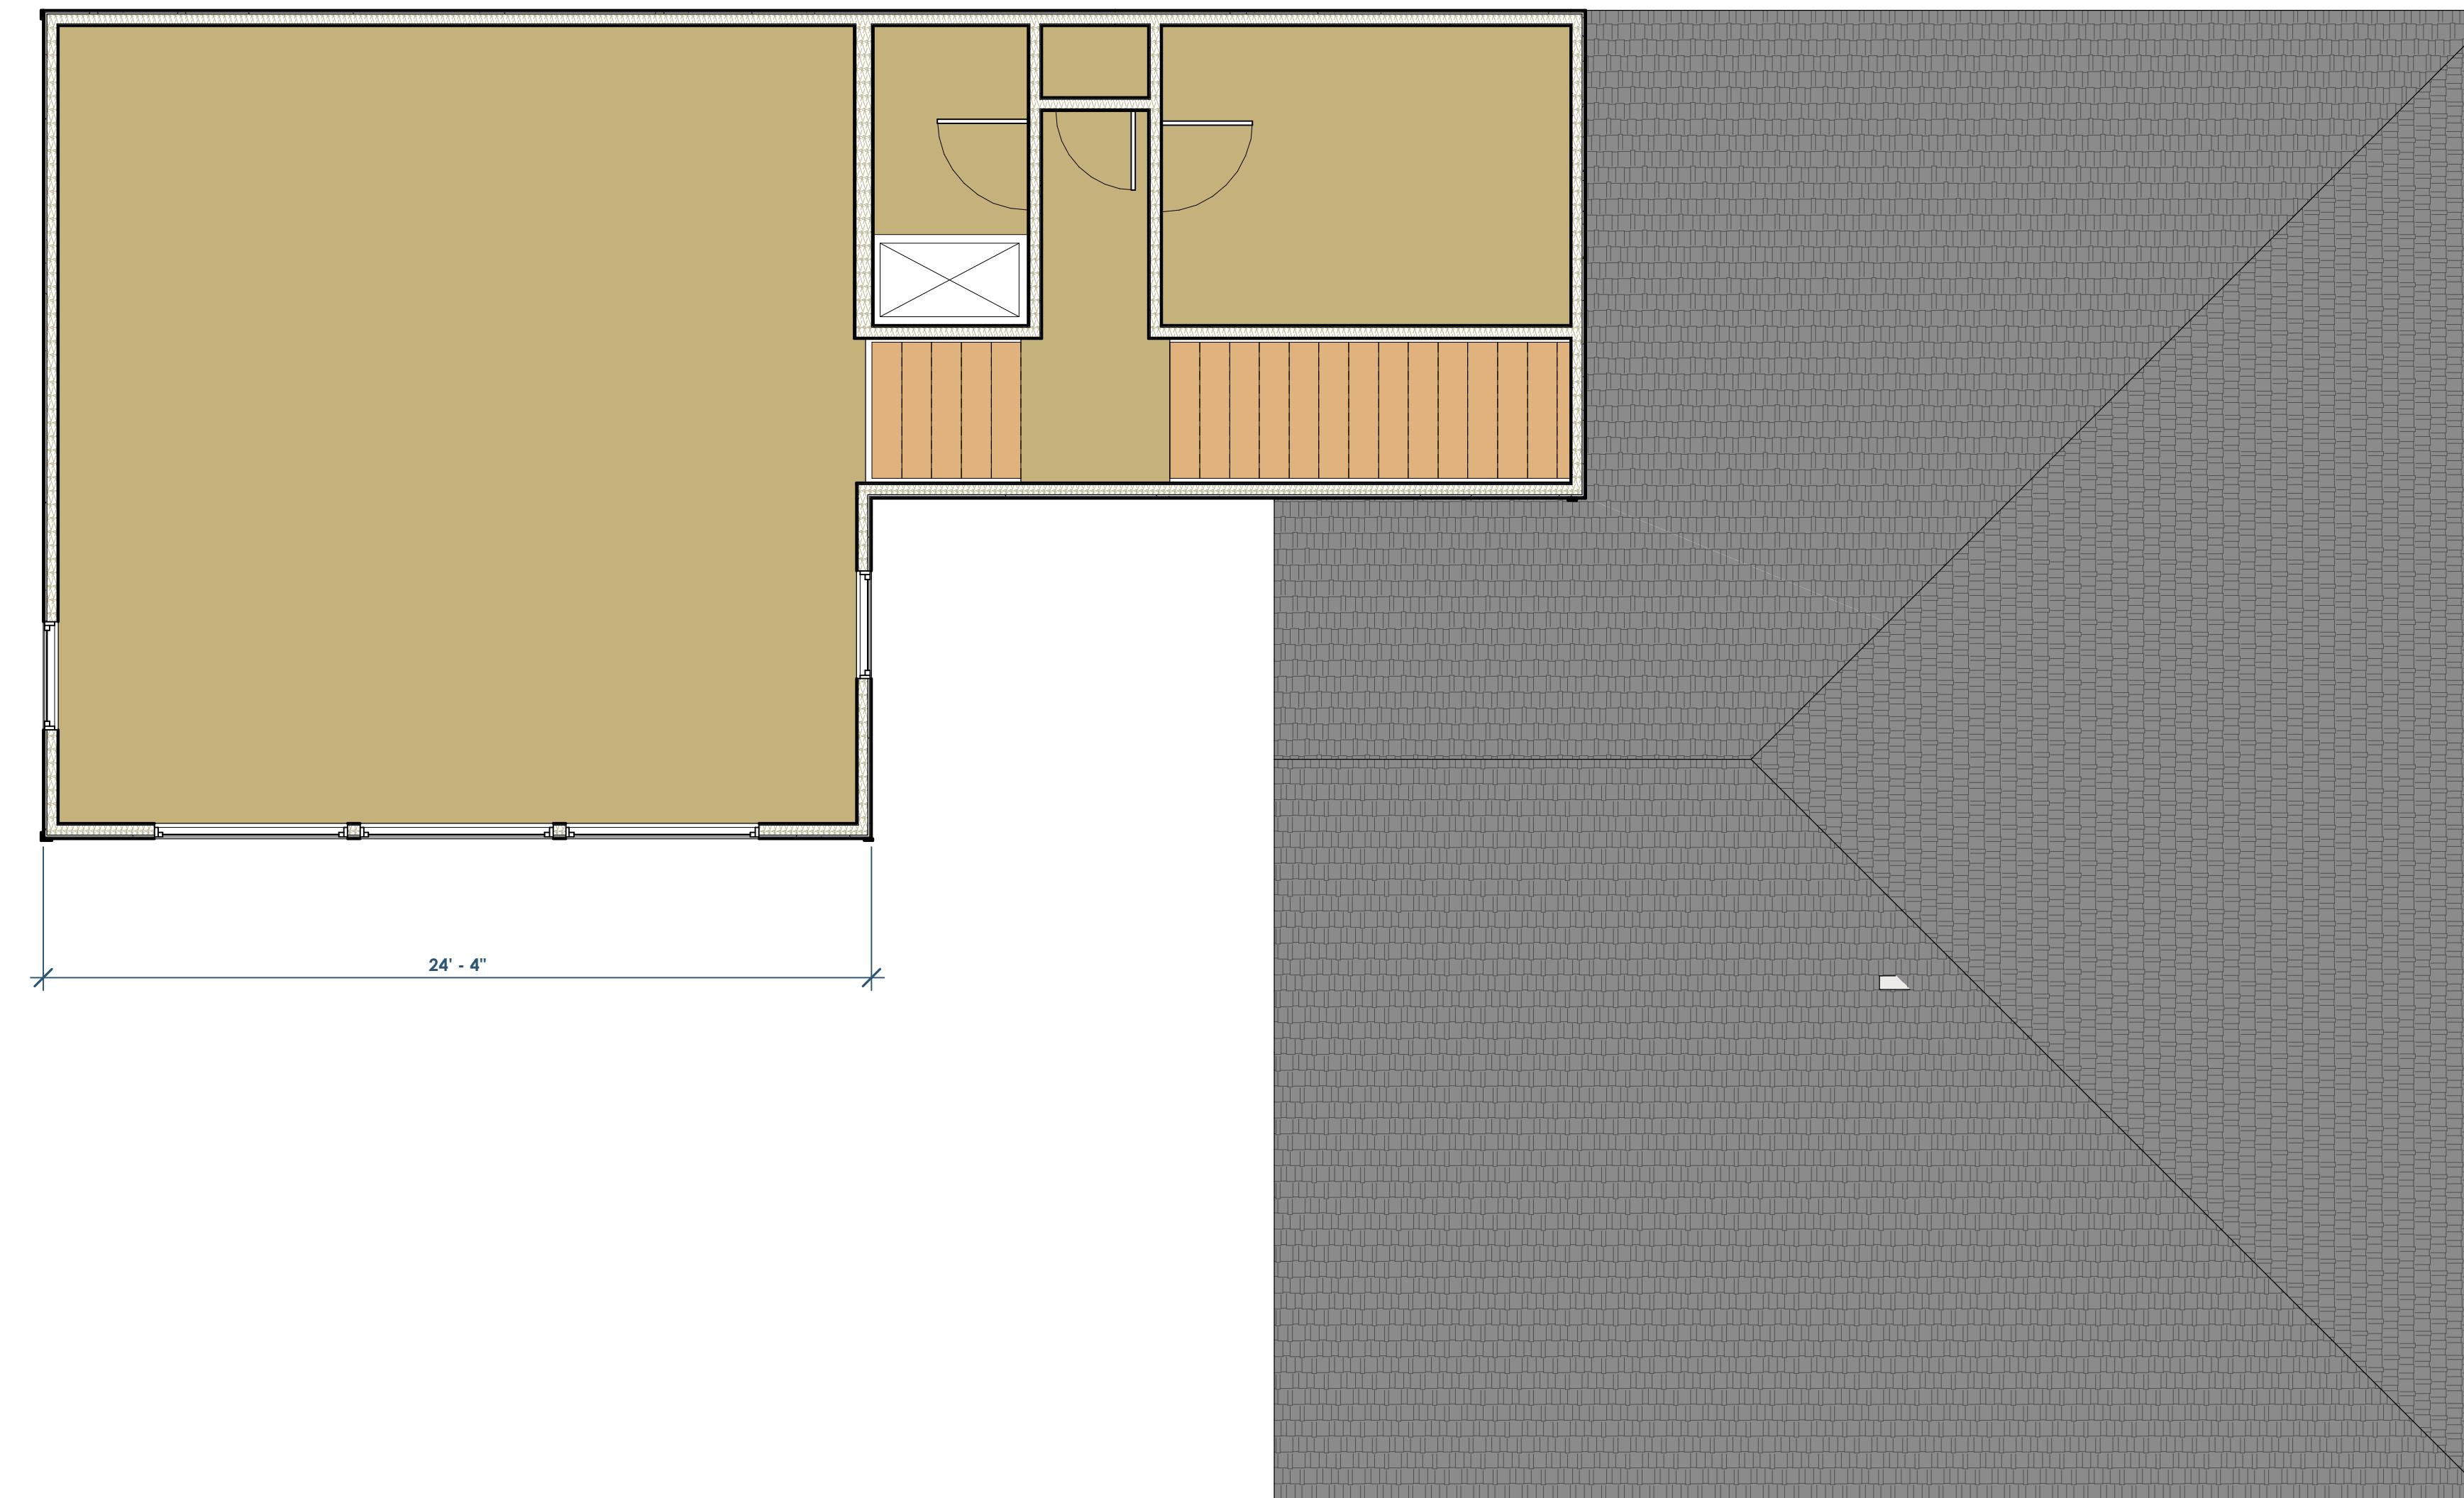

① EXISTING - 2nd FLOOR
1/4" = 1'-0"

5

4

3

2

1

C


C

B

B

A

A

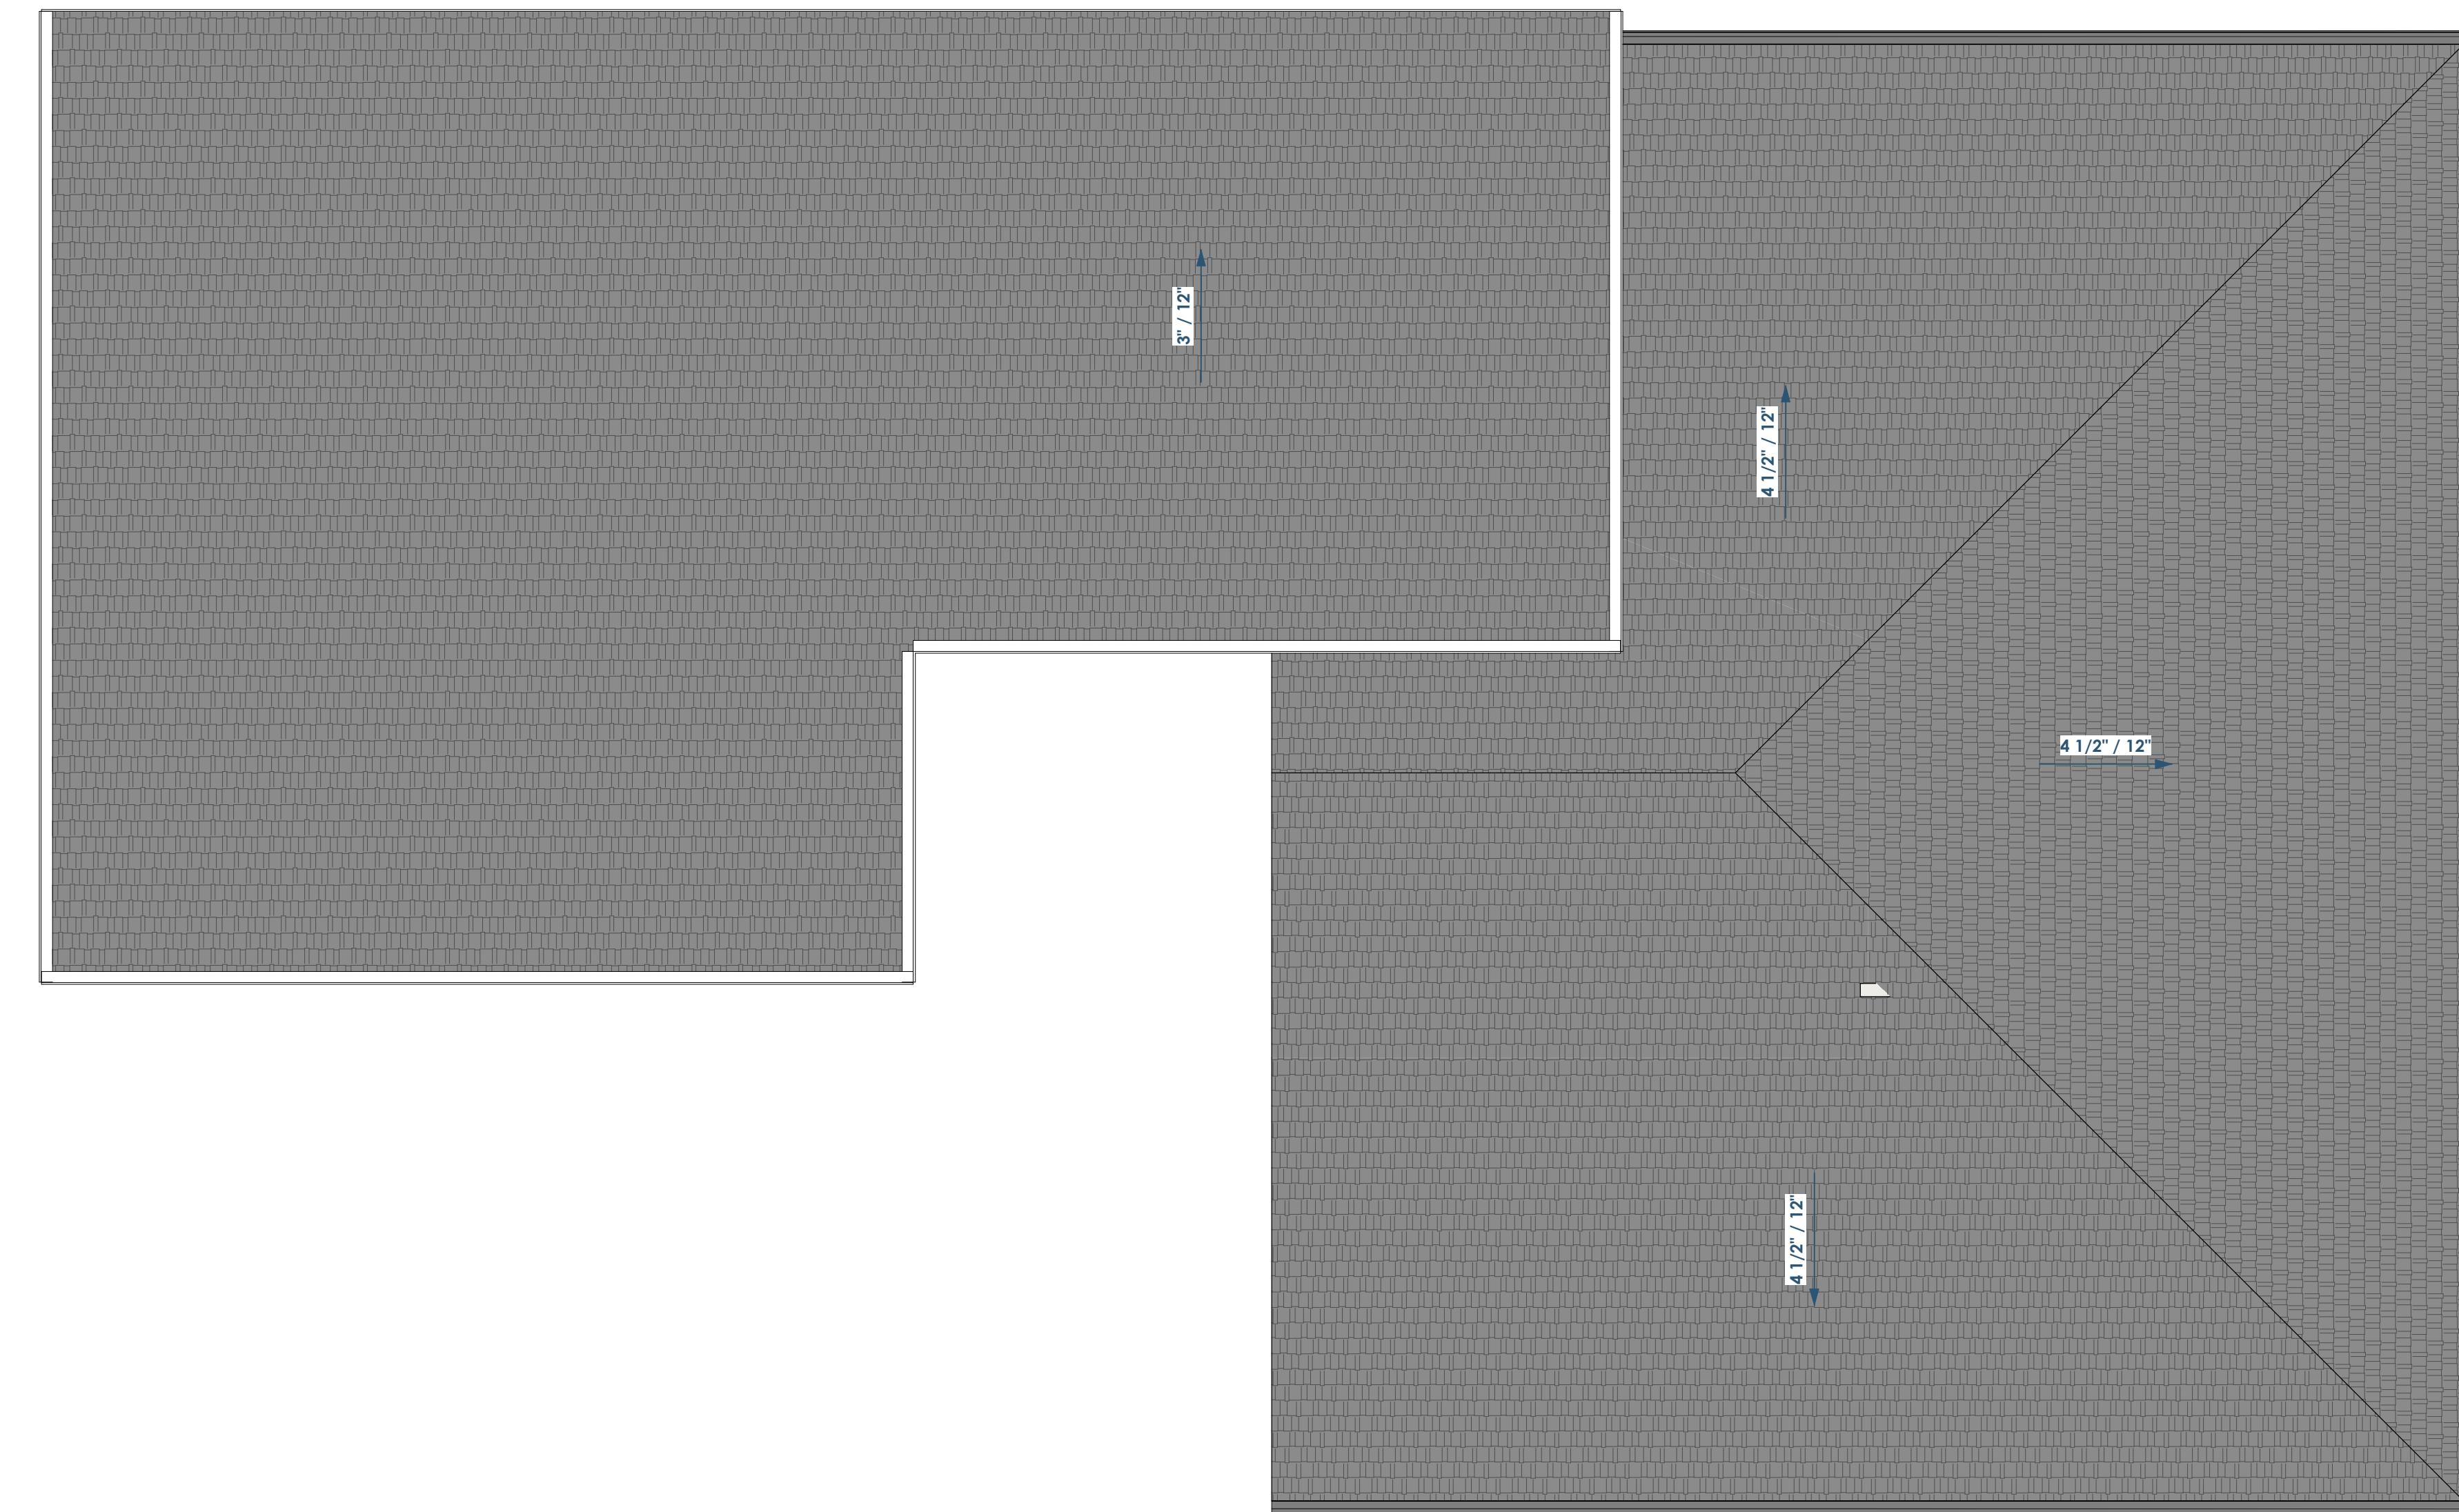

① EXISTING - HIGH ROOF
1/4" = 1'-0"

5

4

3

2

1

C


C

B

B

A

A

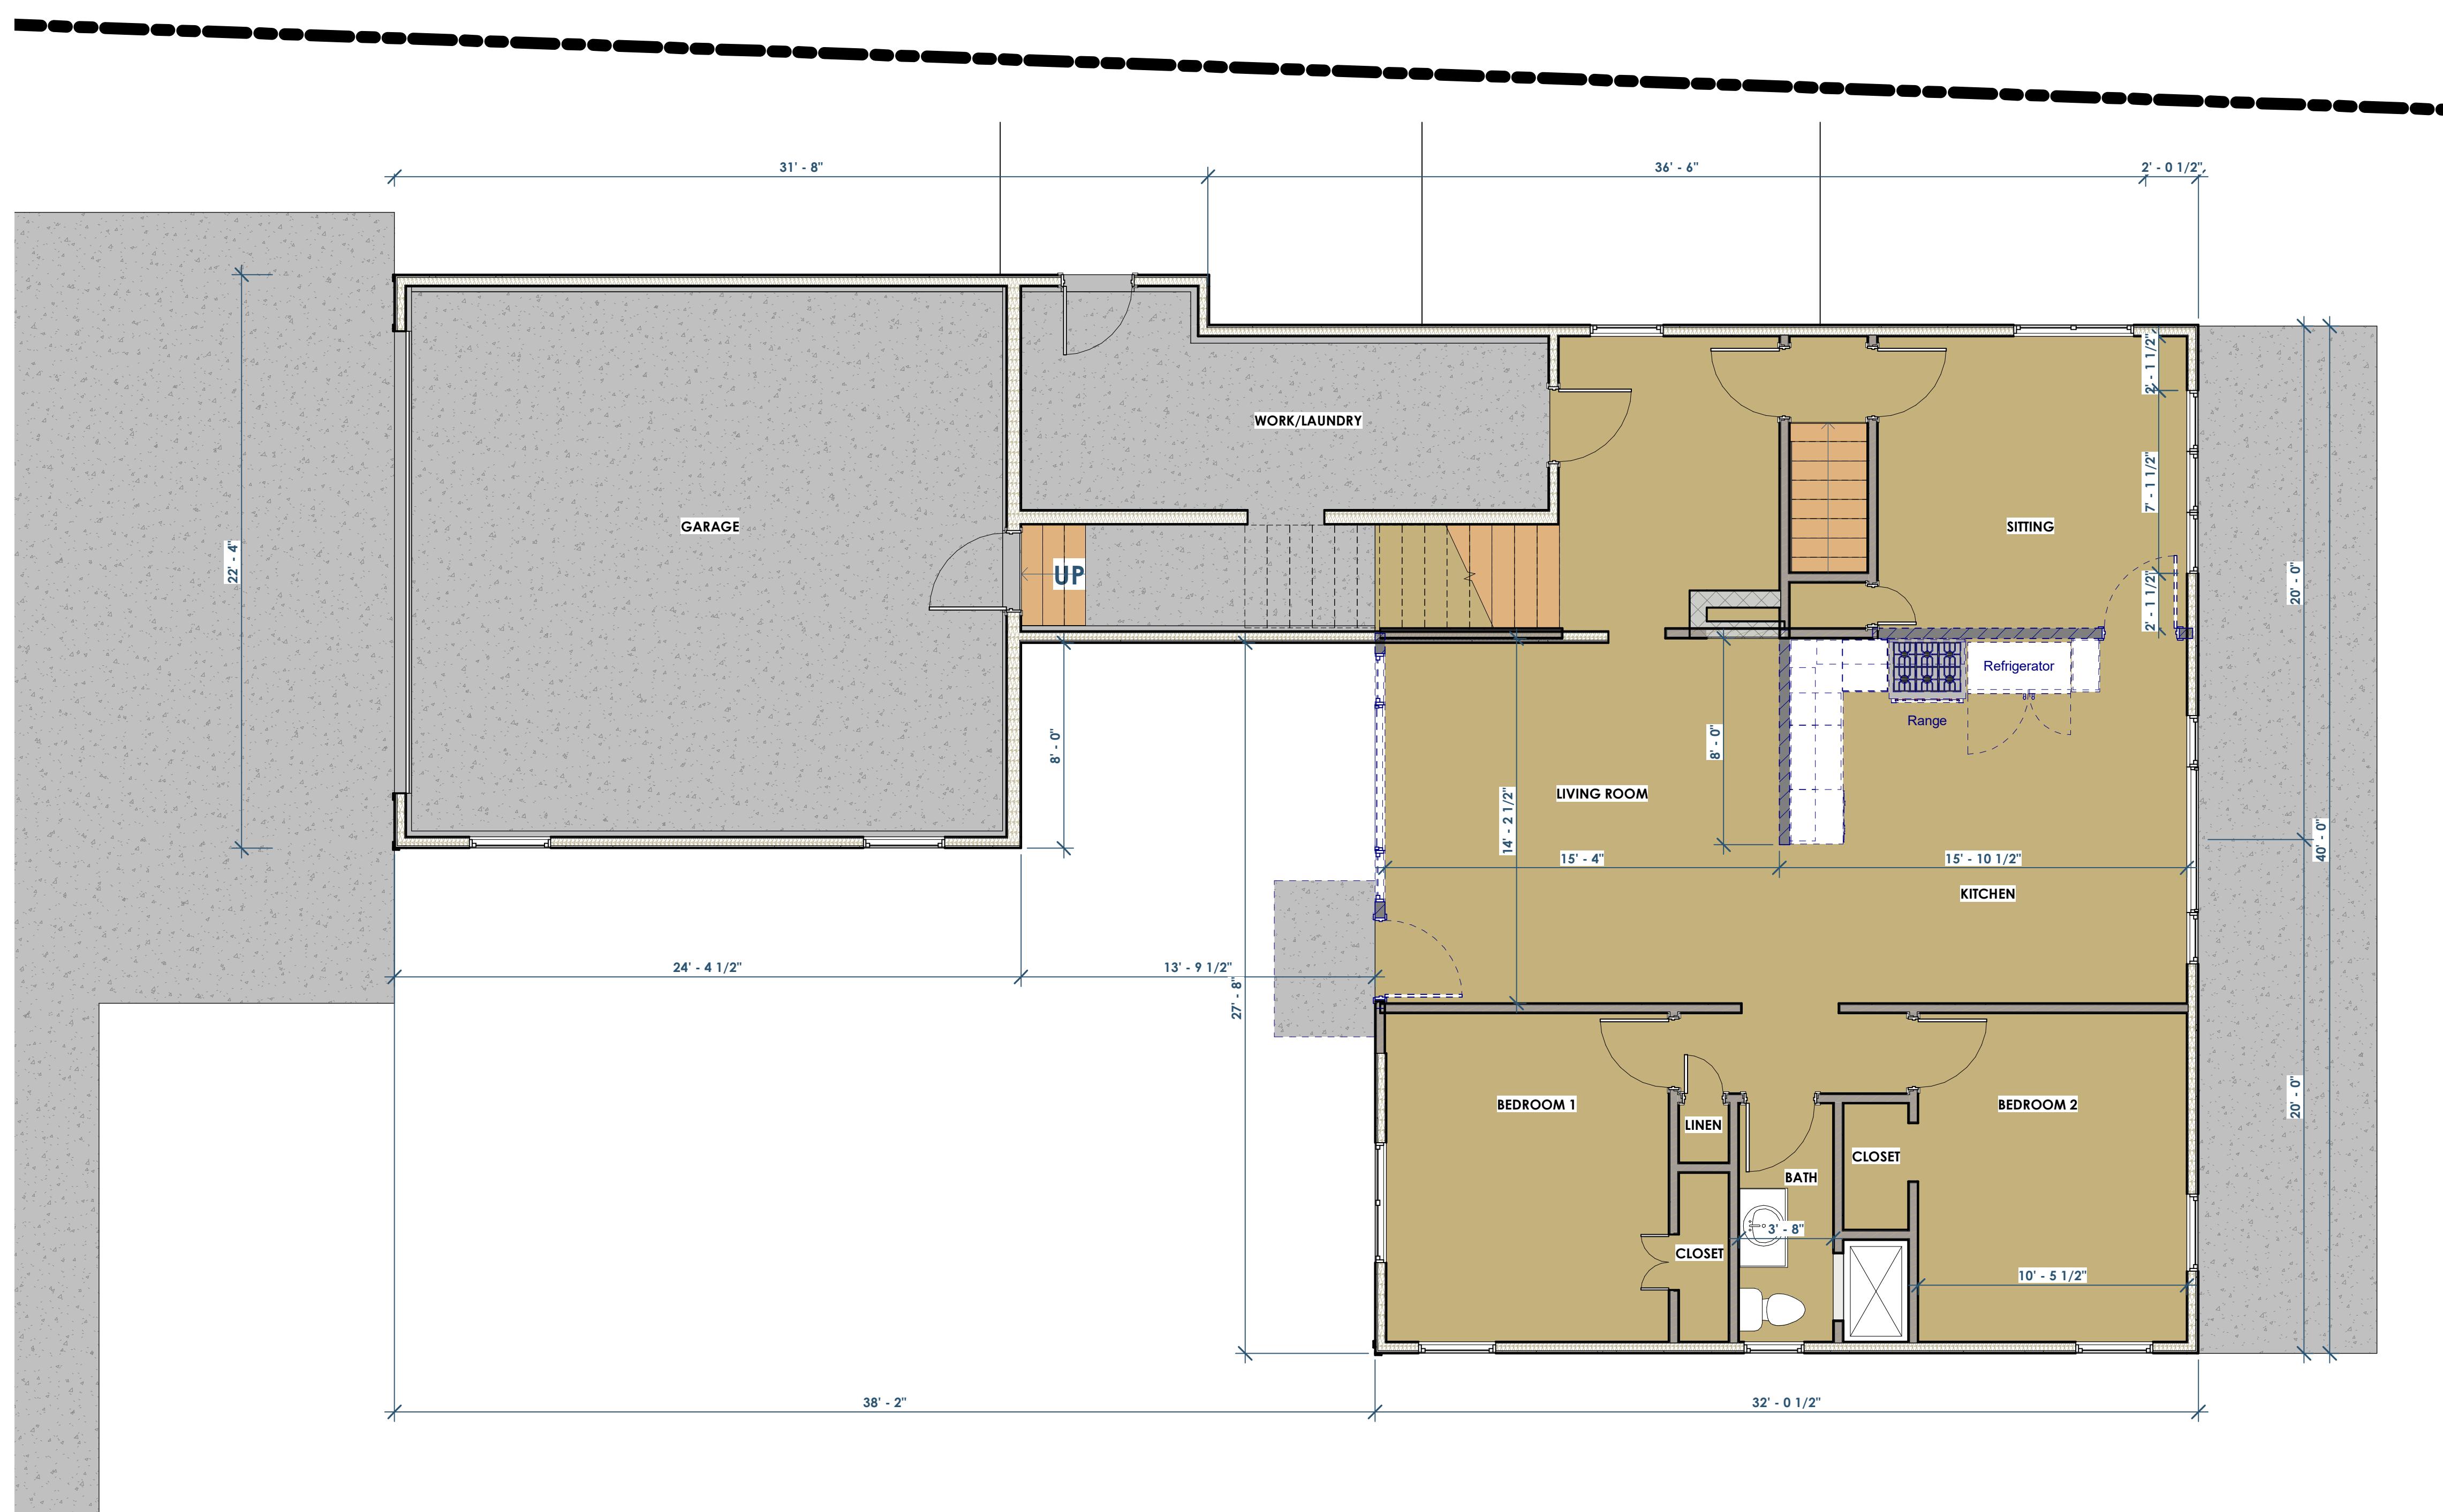

① EXISTING - 1ST FLOOR DEMOLITION
1/4" = 1'-0"



DEMOLITION FIRST (MAIN) FLOOR PLAN - 08/16/2019

KERN RESIDENCE
N6790 SHOREWOOD HILLS RD - LAKE MILLS, WI 53551 AD101

5

4

3

2

1

C


C

B


B

A

A

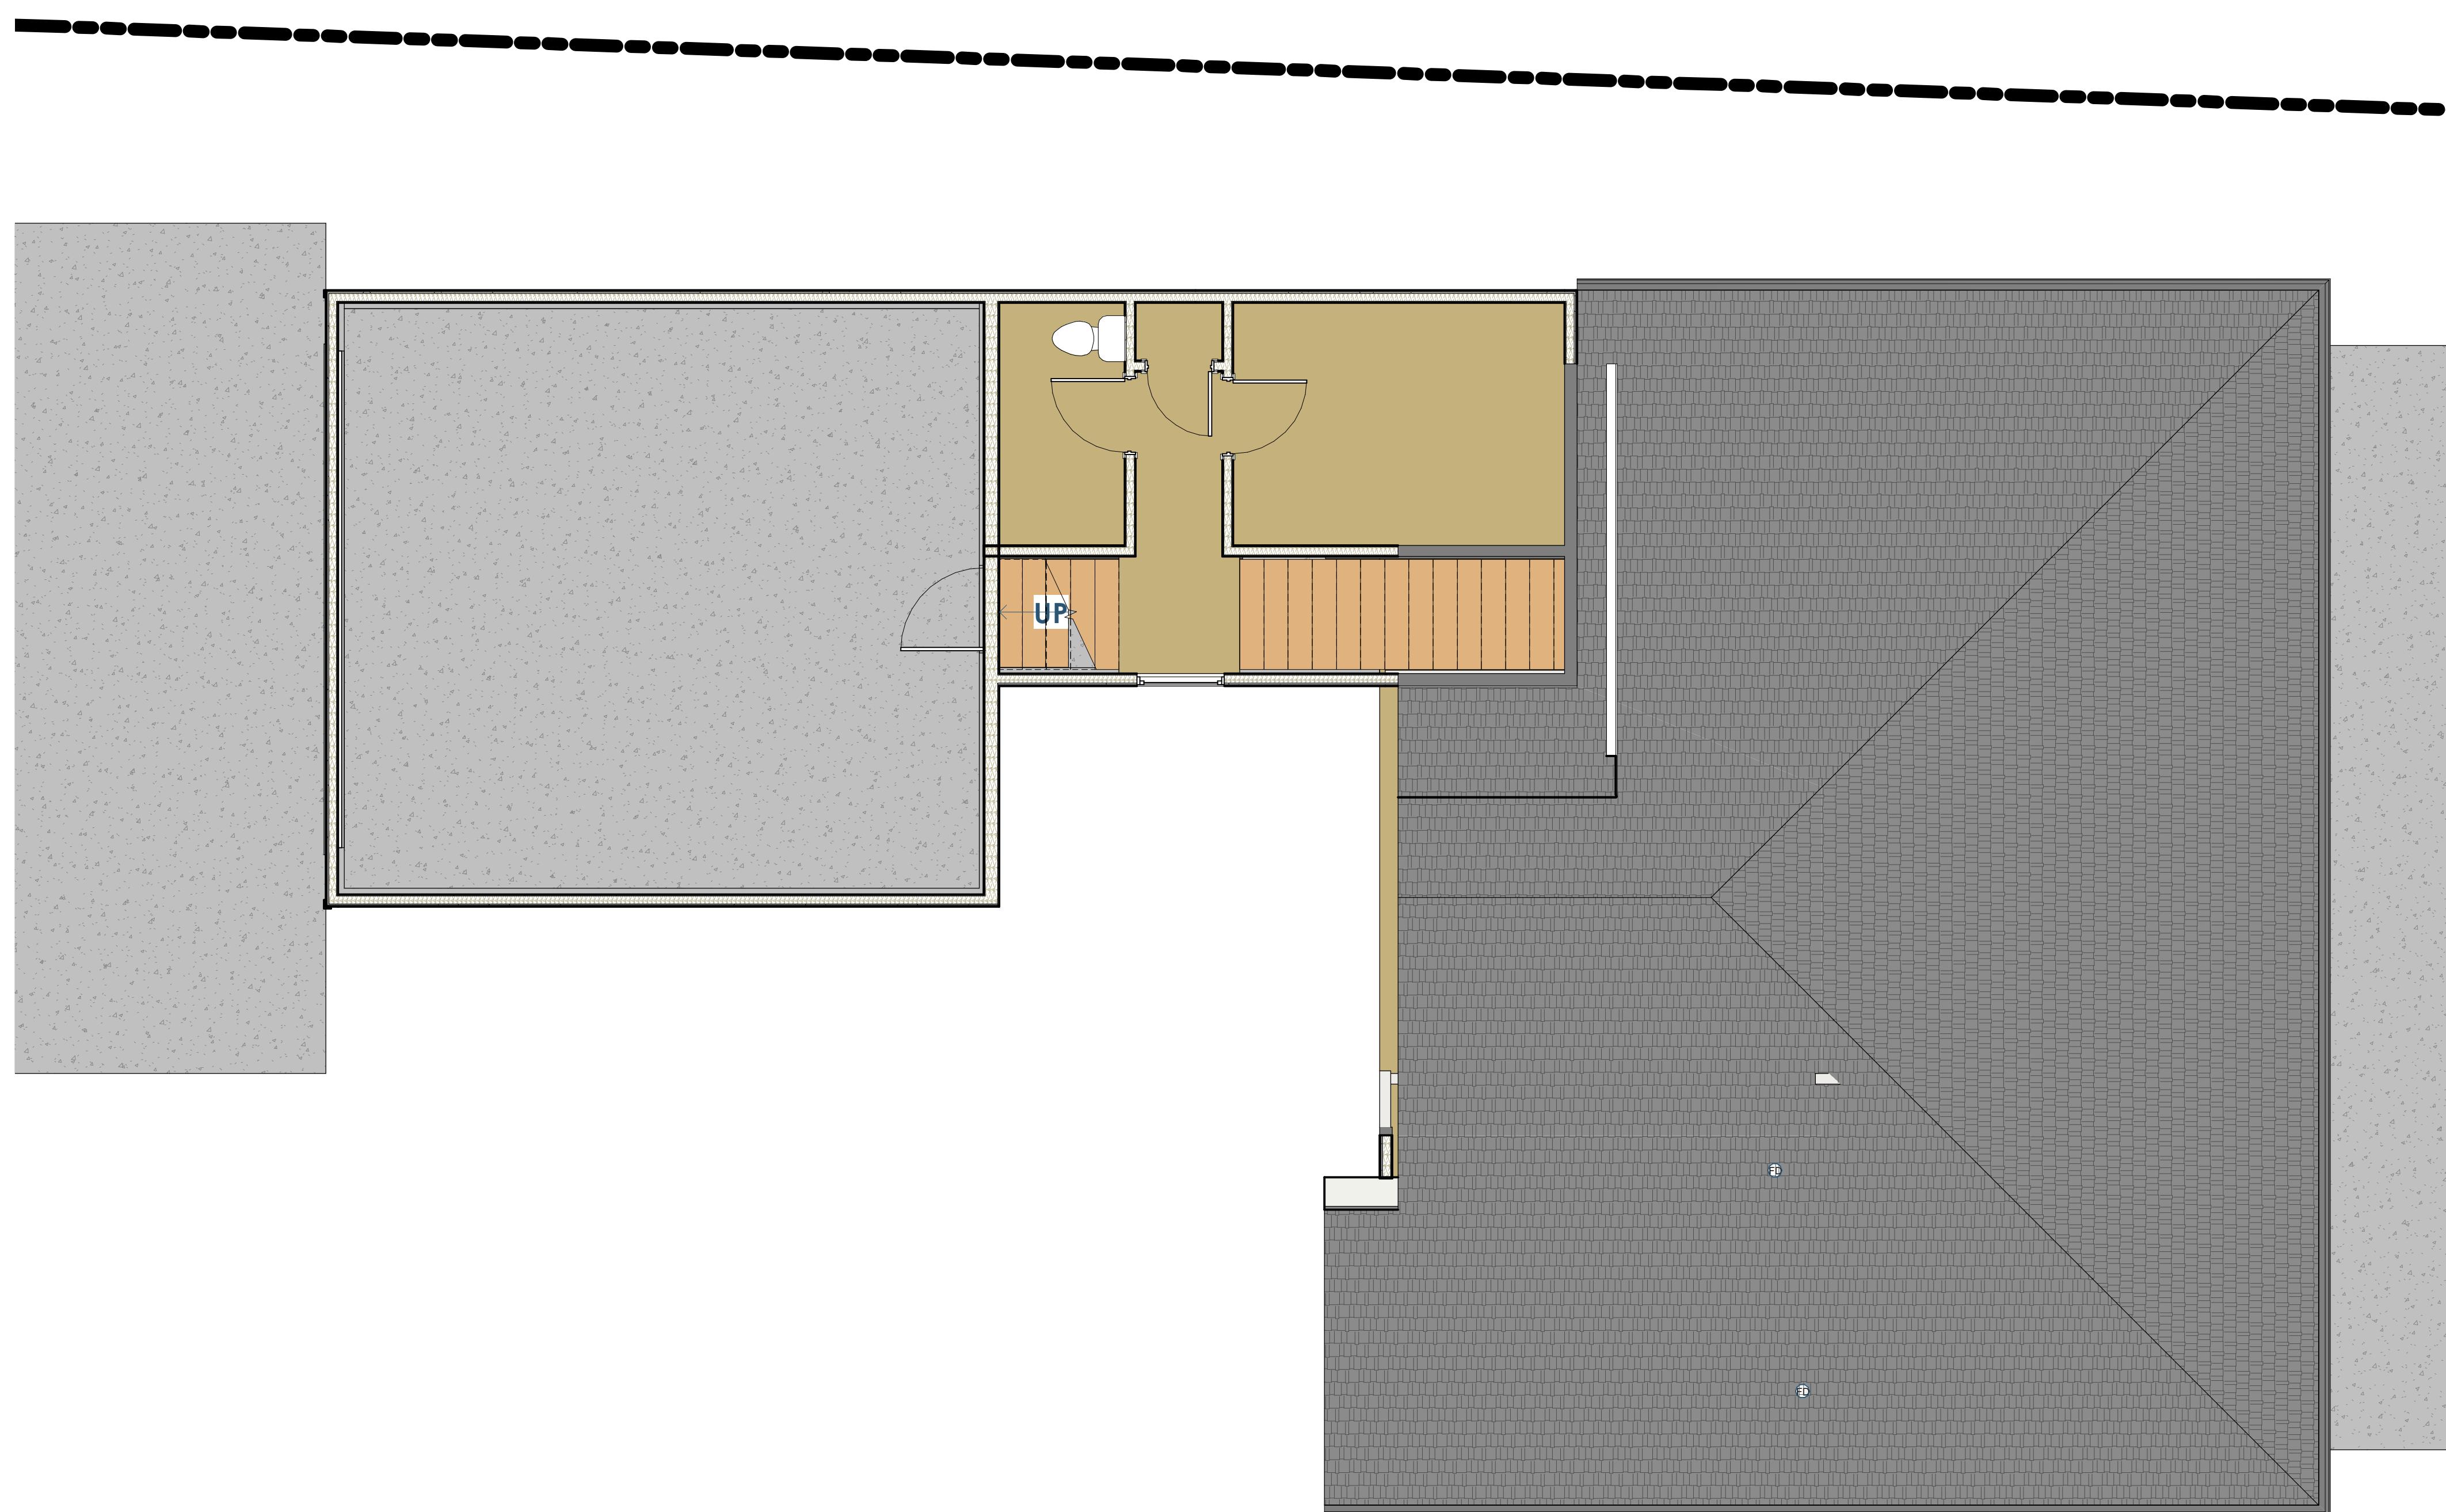

EXISTING - LOW ROOF DEMOLITION
1/4" = 1'-0"

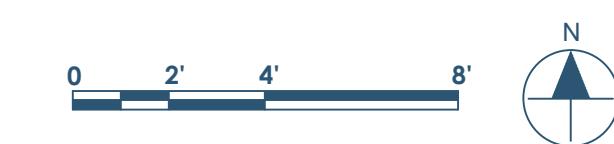

DEMOLITION ROOF PLAN - 08/16/2019

KERN RESIDENCE

N6790 SHOREWOOD HILLS RD - LAKE MILLS, WI 53551 AD102

5

4

3

2

1

C


C

B

B

A

A

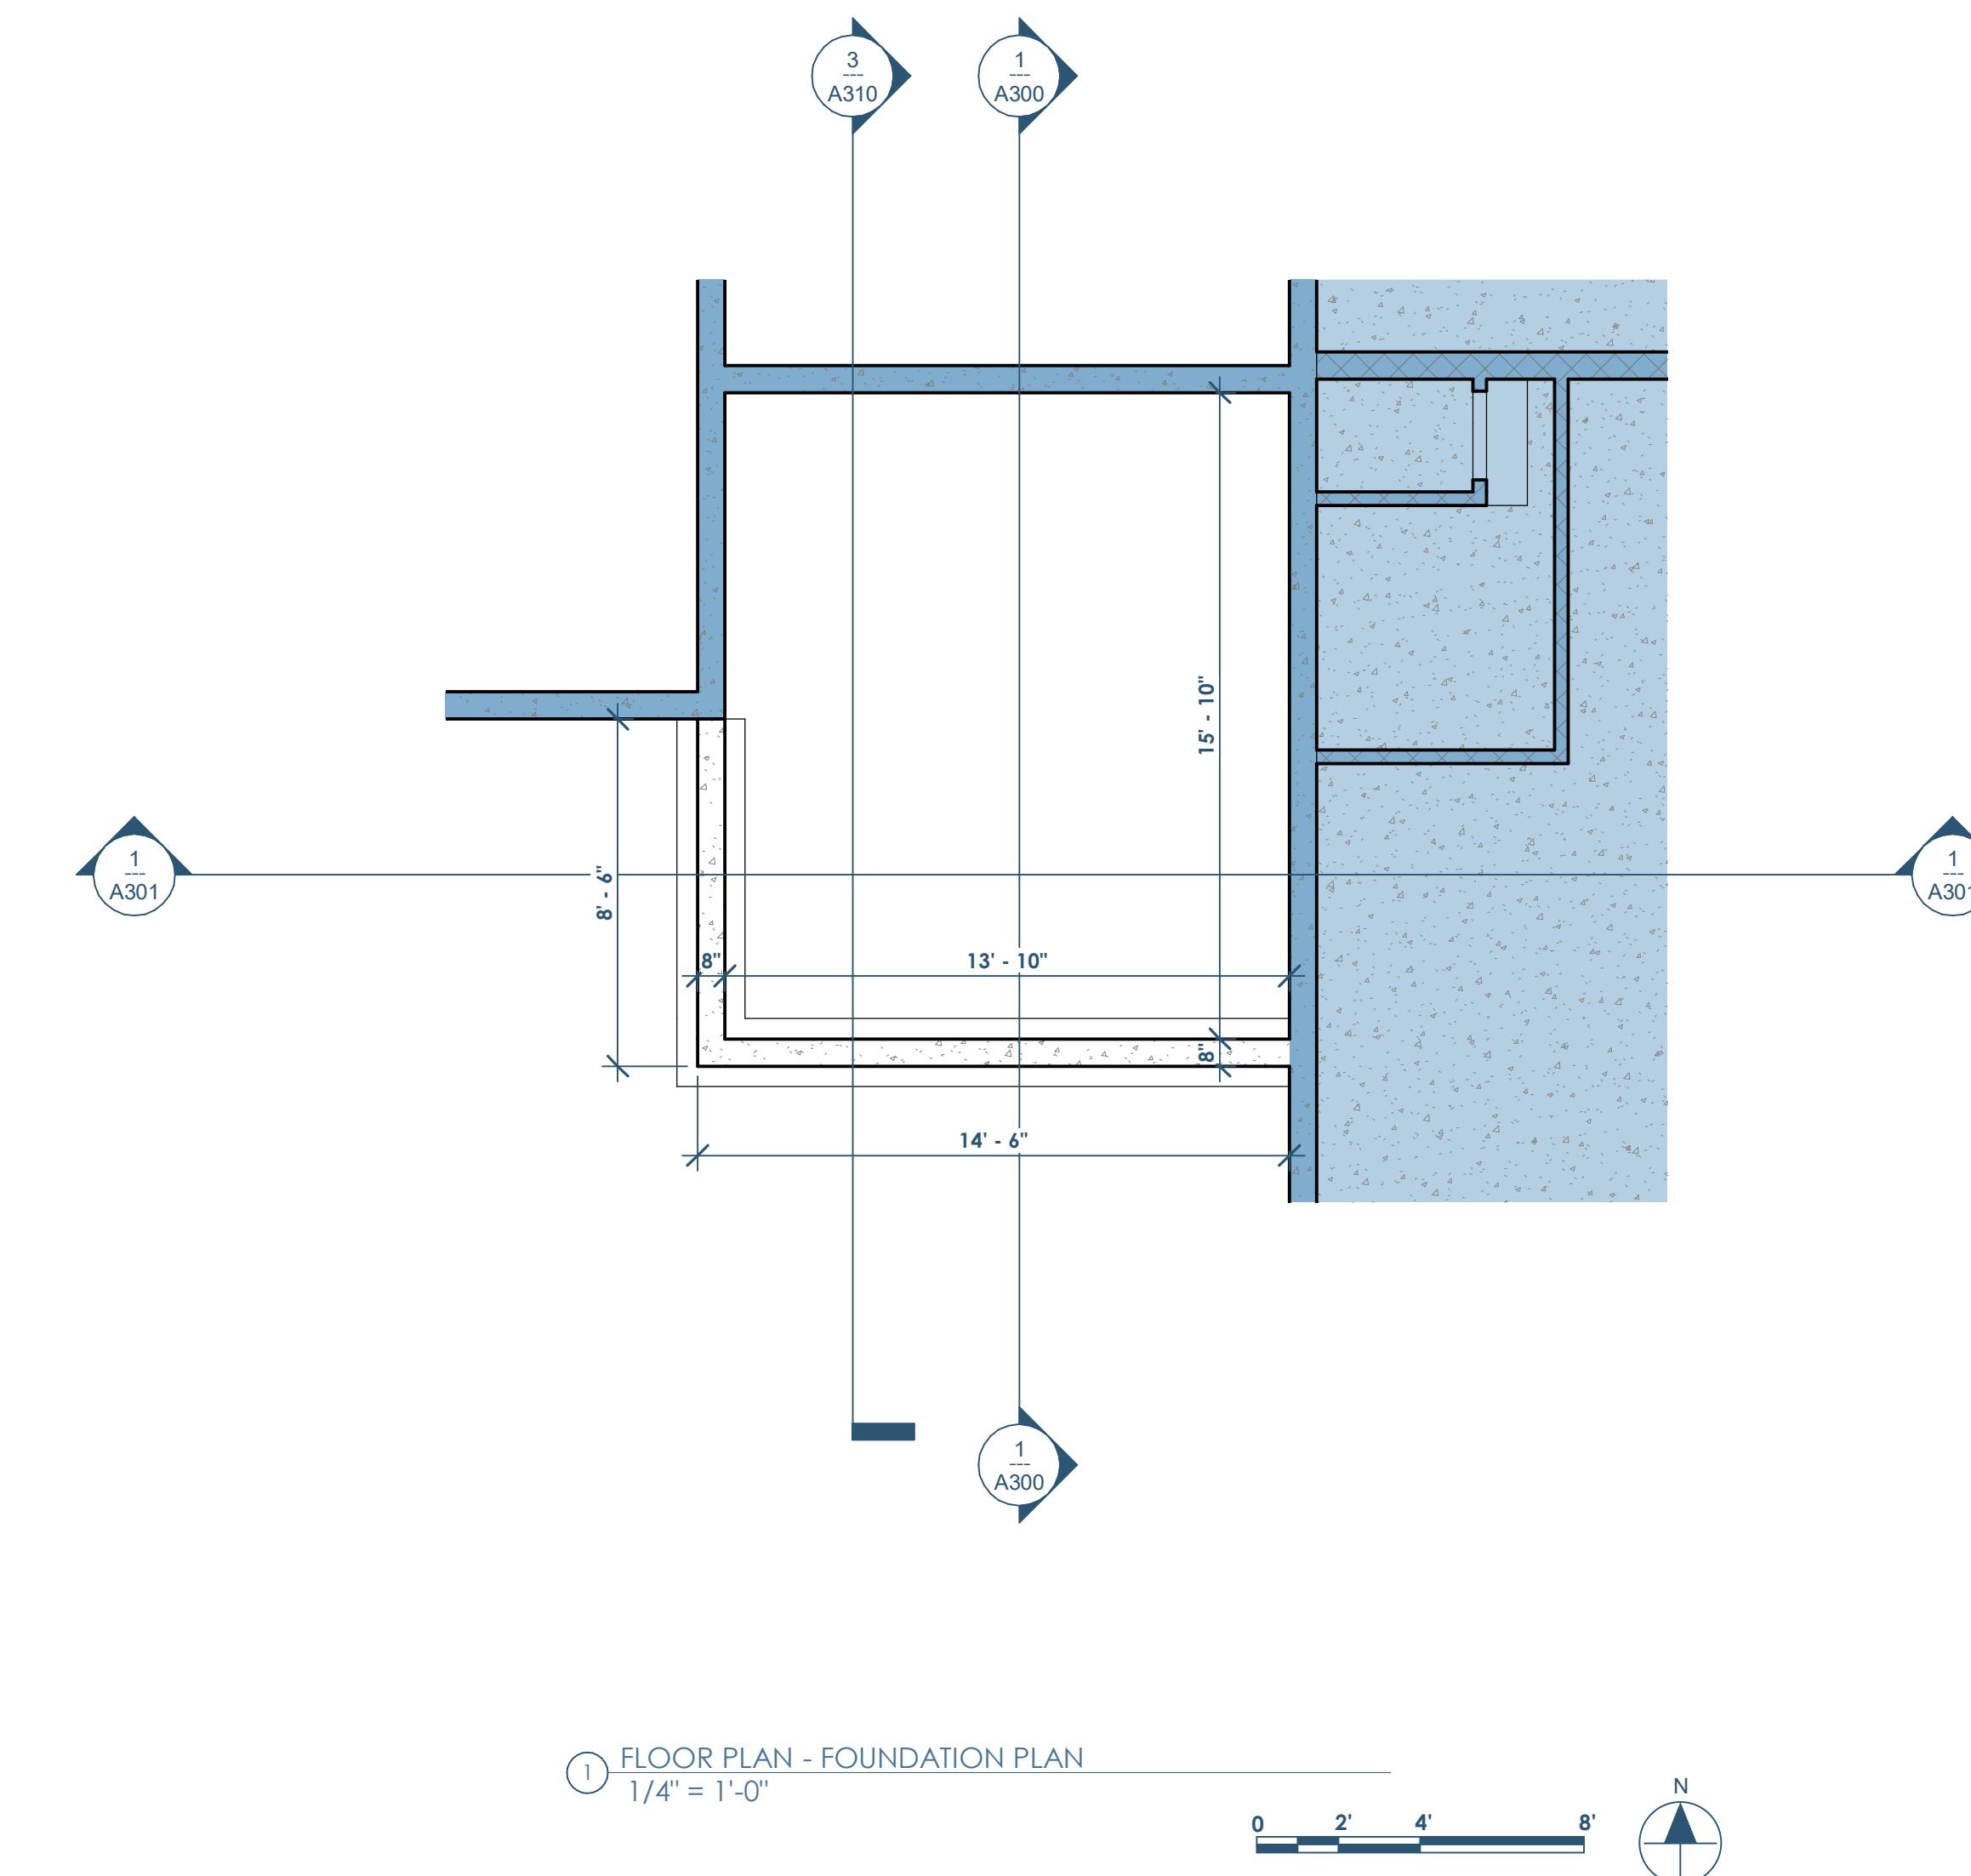

Architect: OpeningDesign
316 W Washington Ave | Suite 675
Madison, WI 53703
ryan@openingdesign.com | 773.425.6456

STRUCTURAL GENERAL NOTES & FOUNDATION PLAN - 08/16/2019
KERN RESIDENCE
N6790 SHOREWOOD HILLS RD - LAKE MILLS, WI 53551

S101

5

4

3

2

1

C


C

B


B

A

A

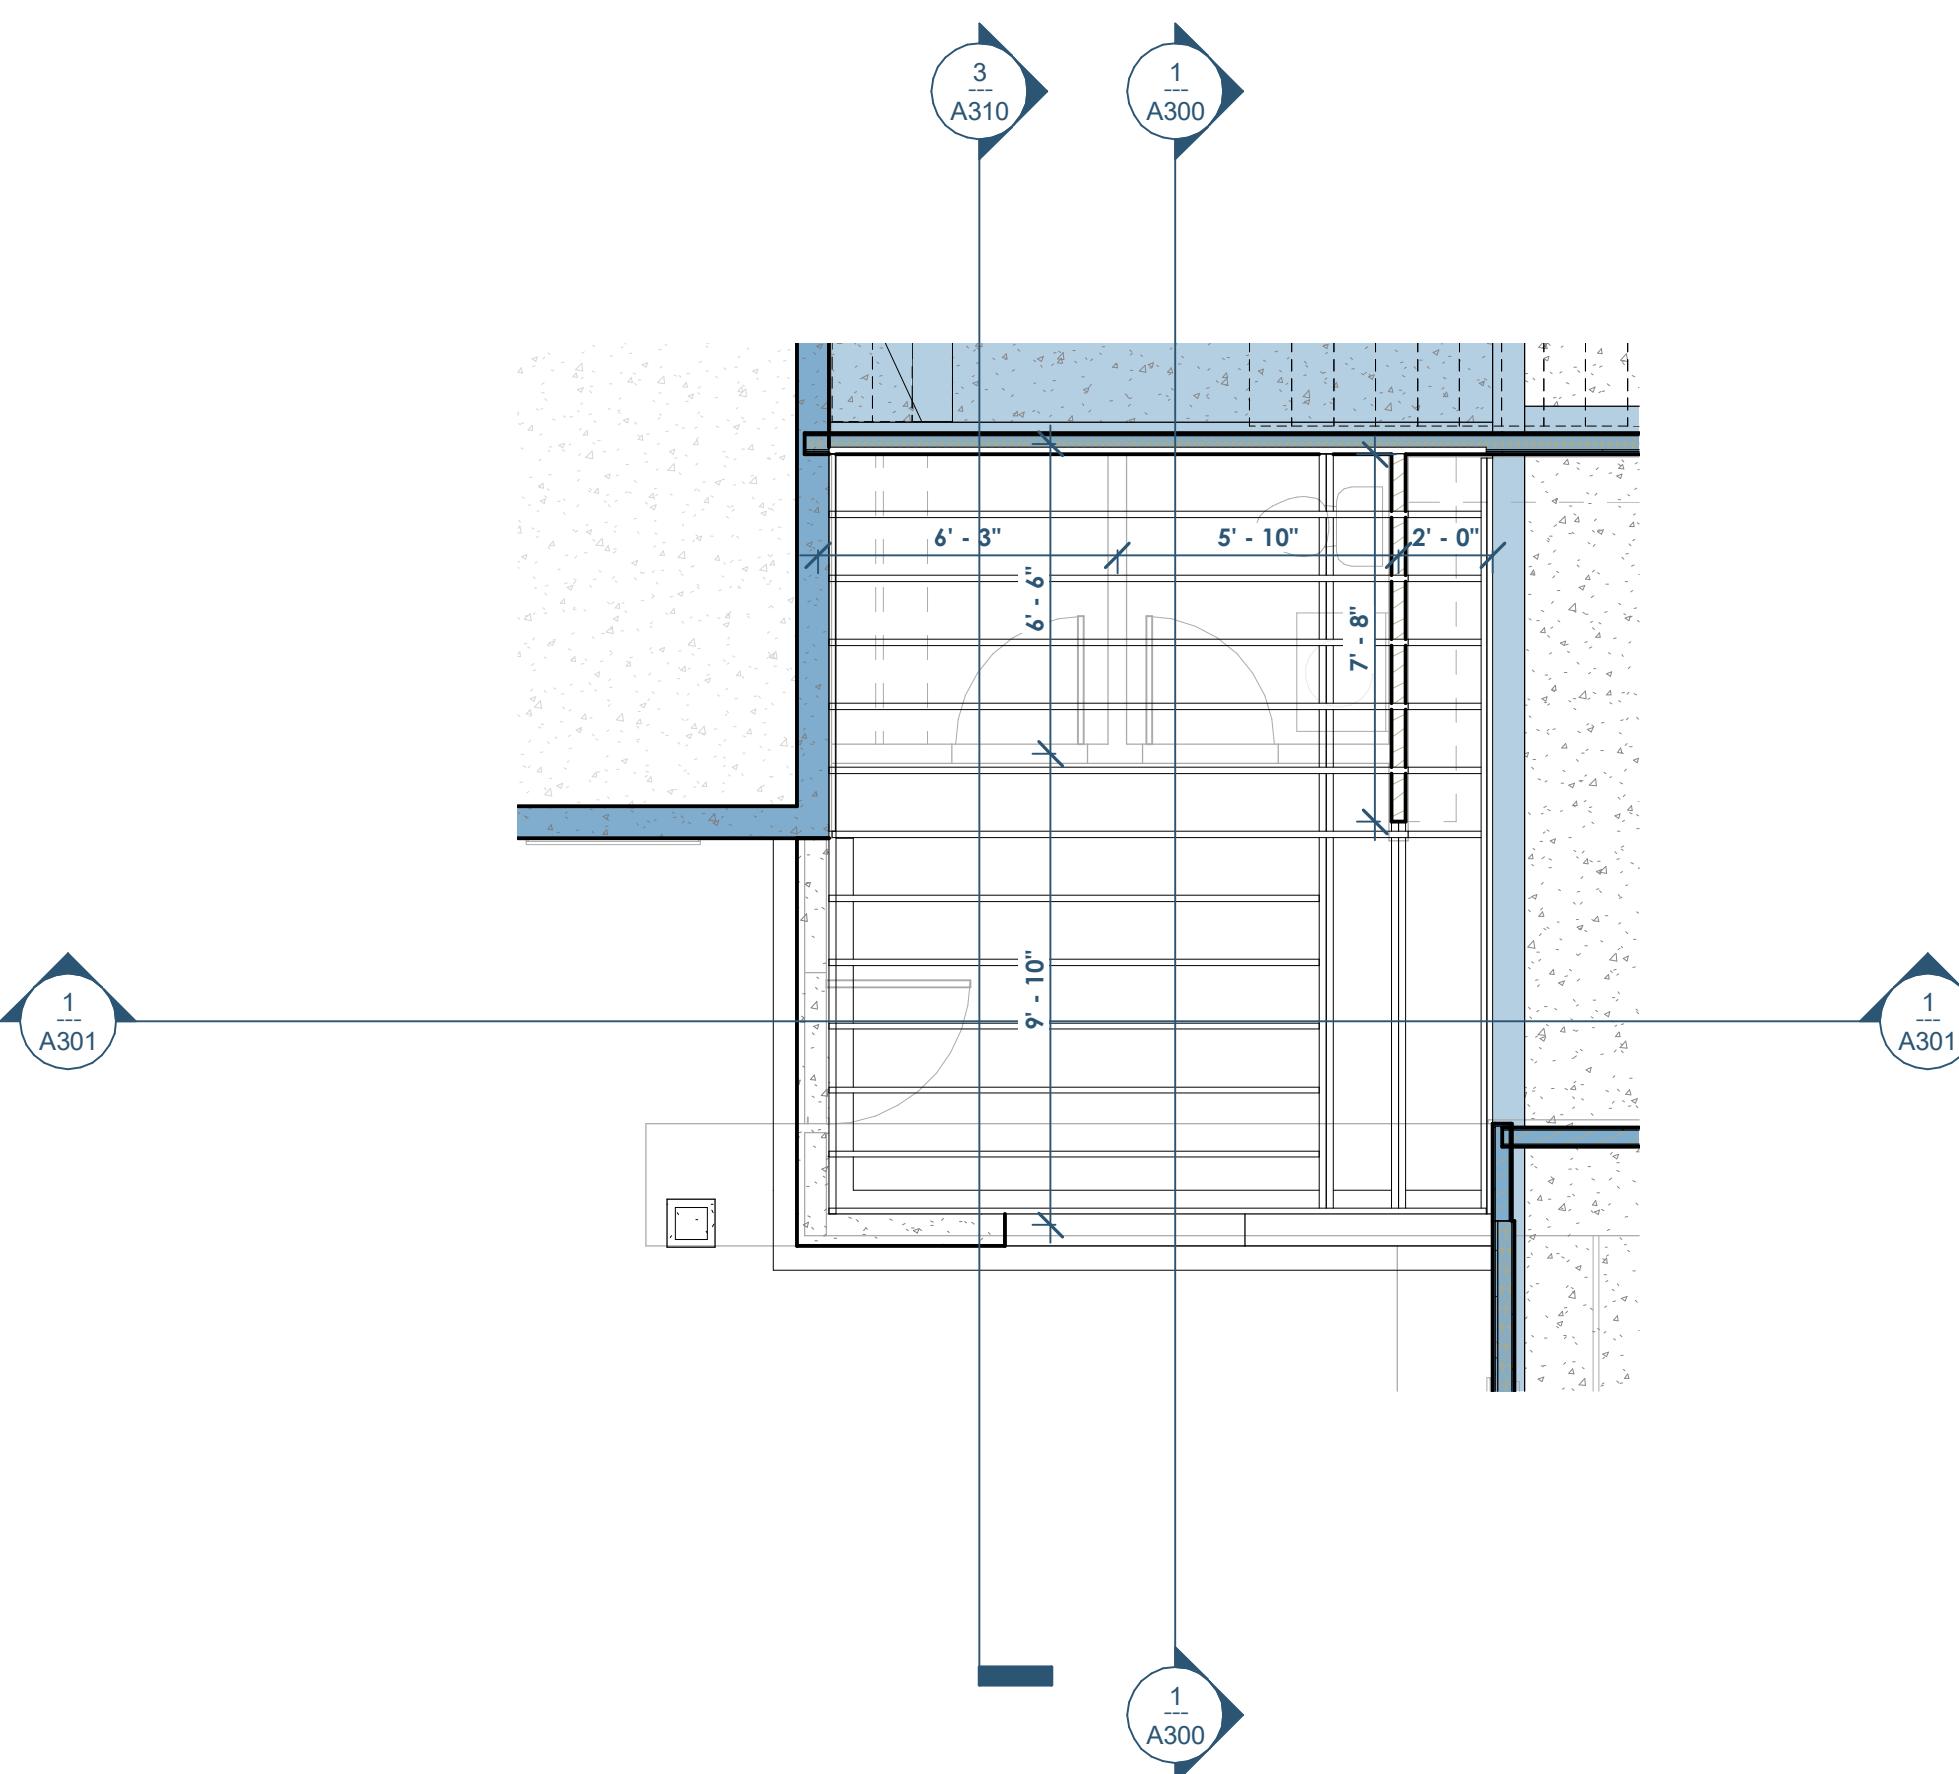

① FLOOR PLAN - 1ST FLOOR FRAMING PLAN
1/4" = 1'-0"

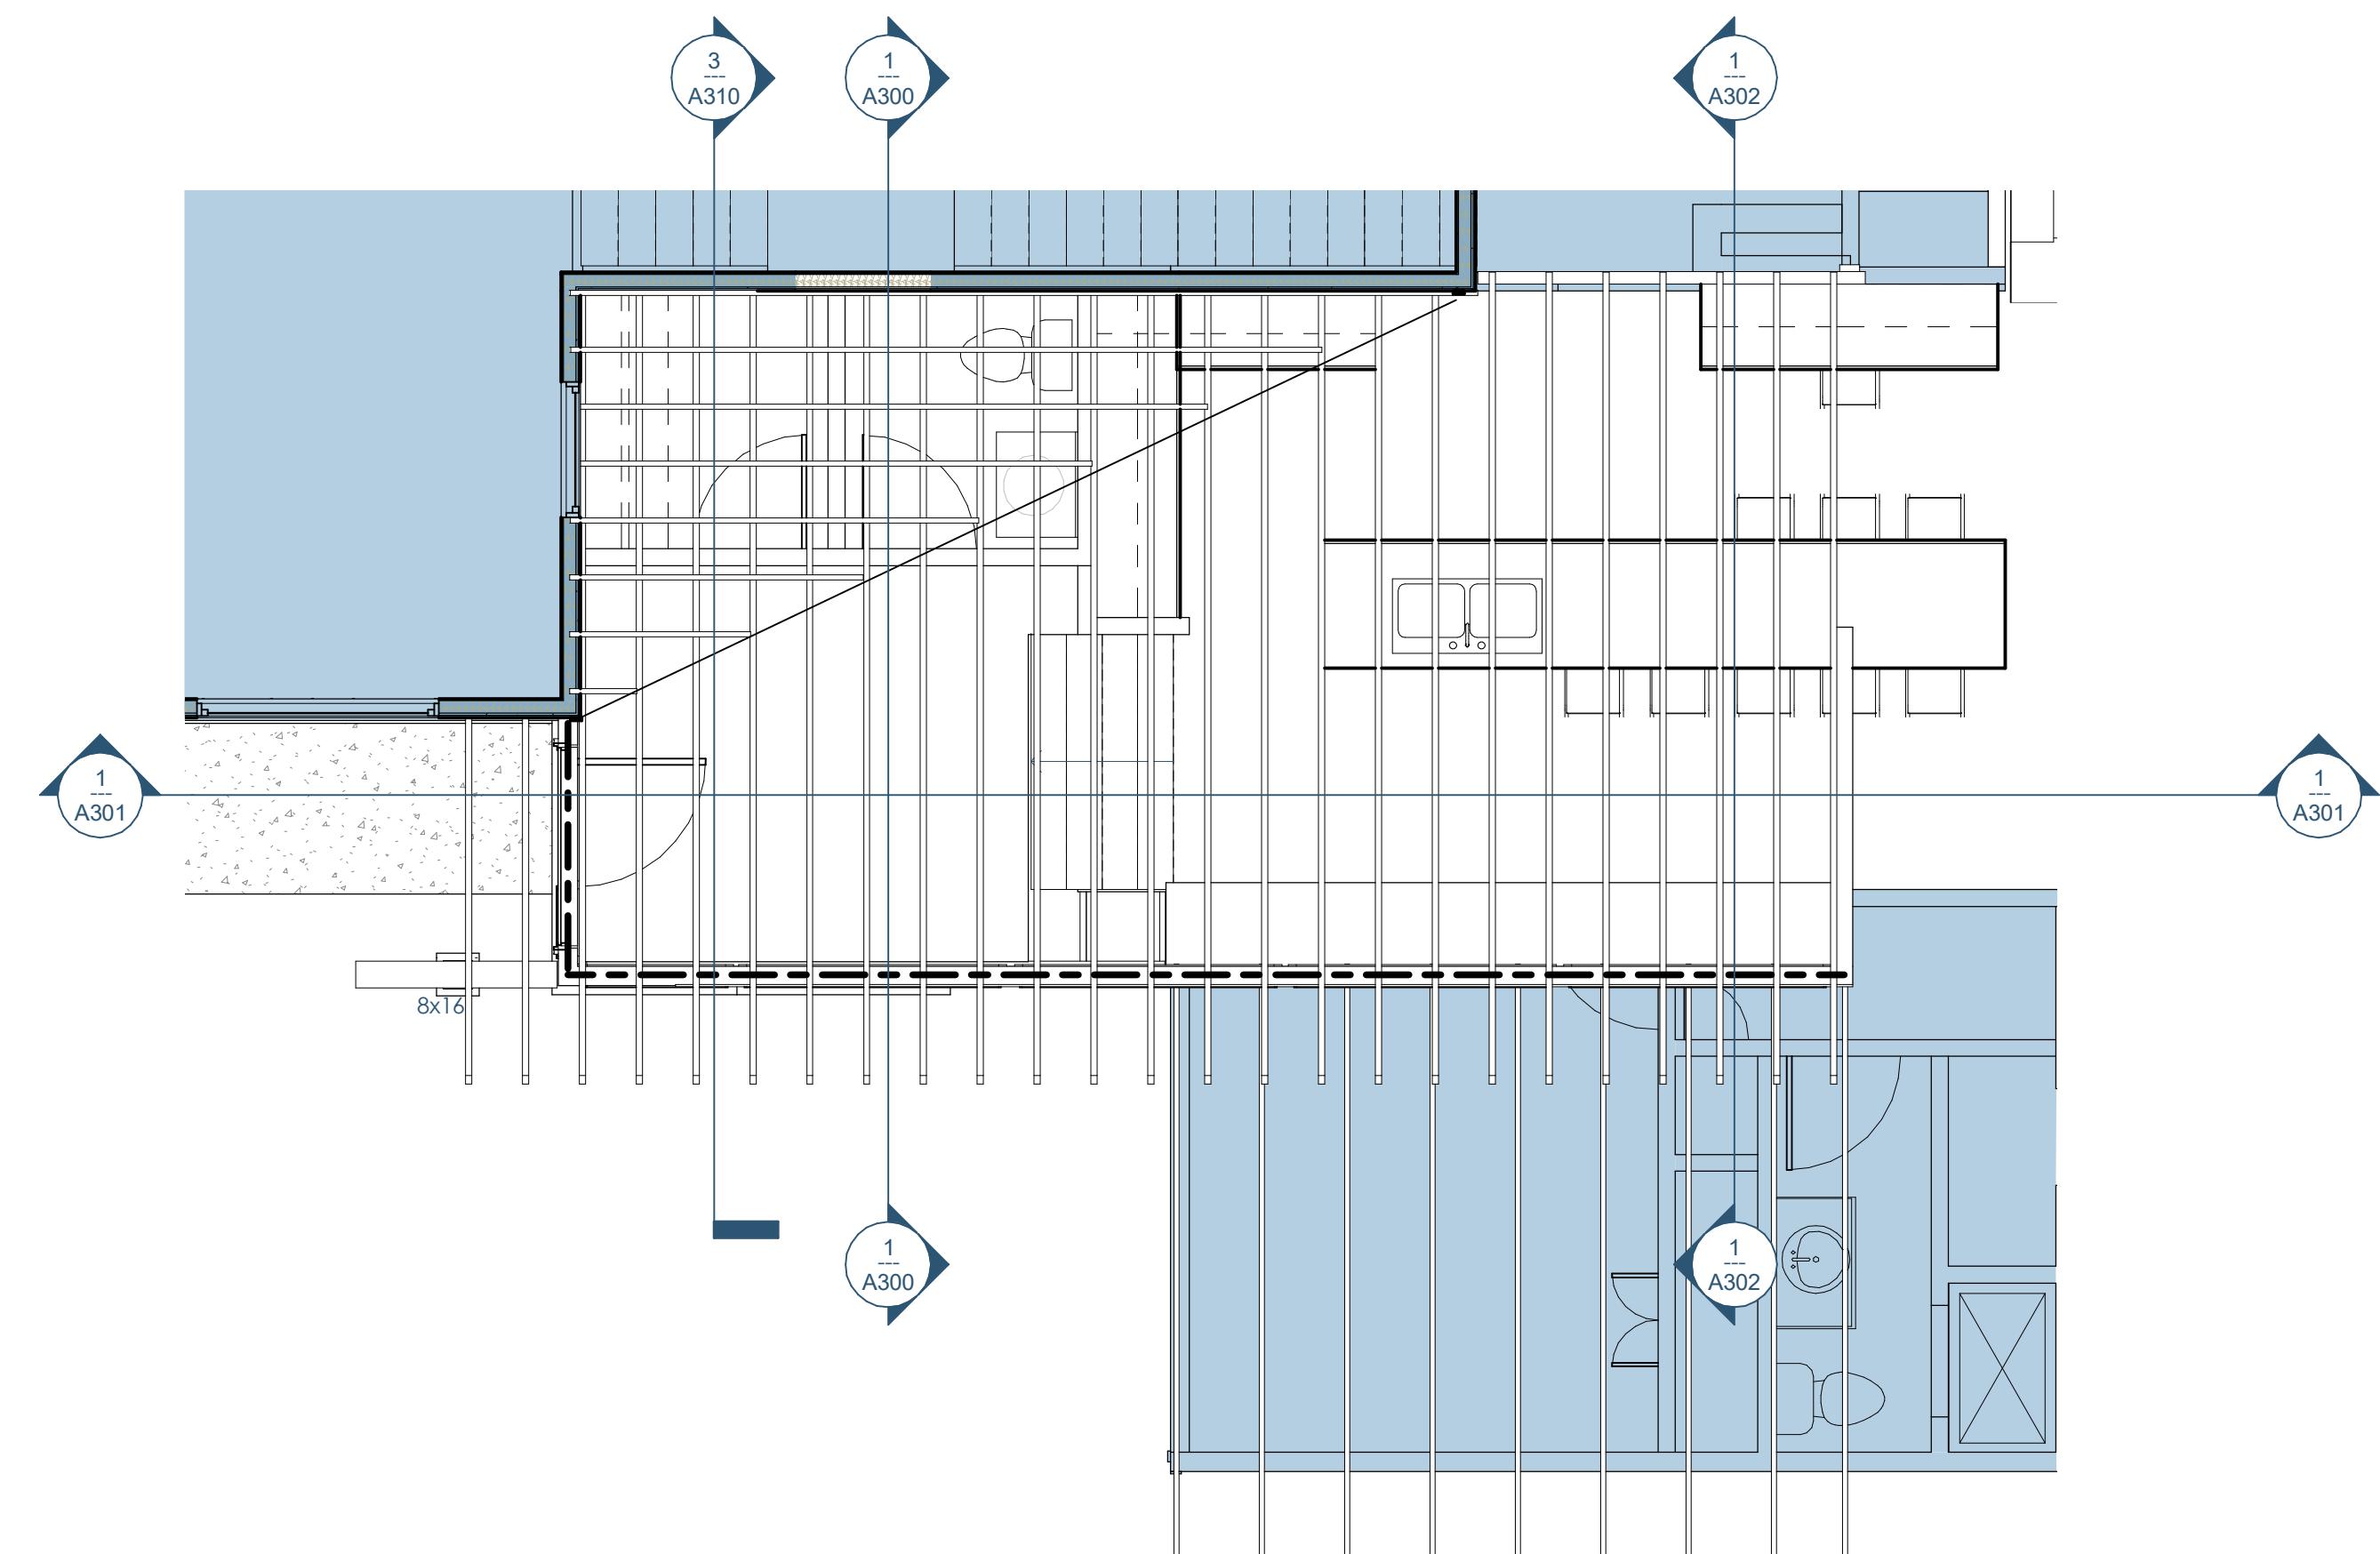

② FLOOR PLAN - ROOF FRAMING PLAN
1/4" = 1'-0"



Architect: OpeningDesign
316 W Washington Ave | Suite 675
Madison, WI 53703
ryan@openingdesign.com | 773.425.6456

STRUCTURAL FRAMING PLANS - 08/16/2019
KERN RESIDENCE
N6790 SHOREWOOD HILLS RD - LAKE MILLS, WI 53551

S102

5

4

3

2

1

C


C

B


B

A

A

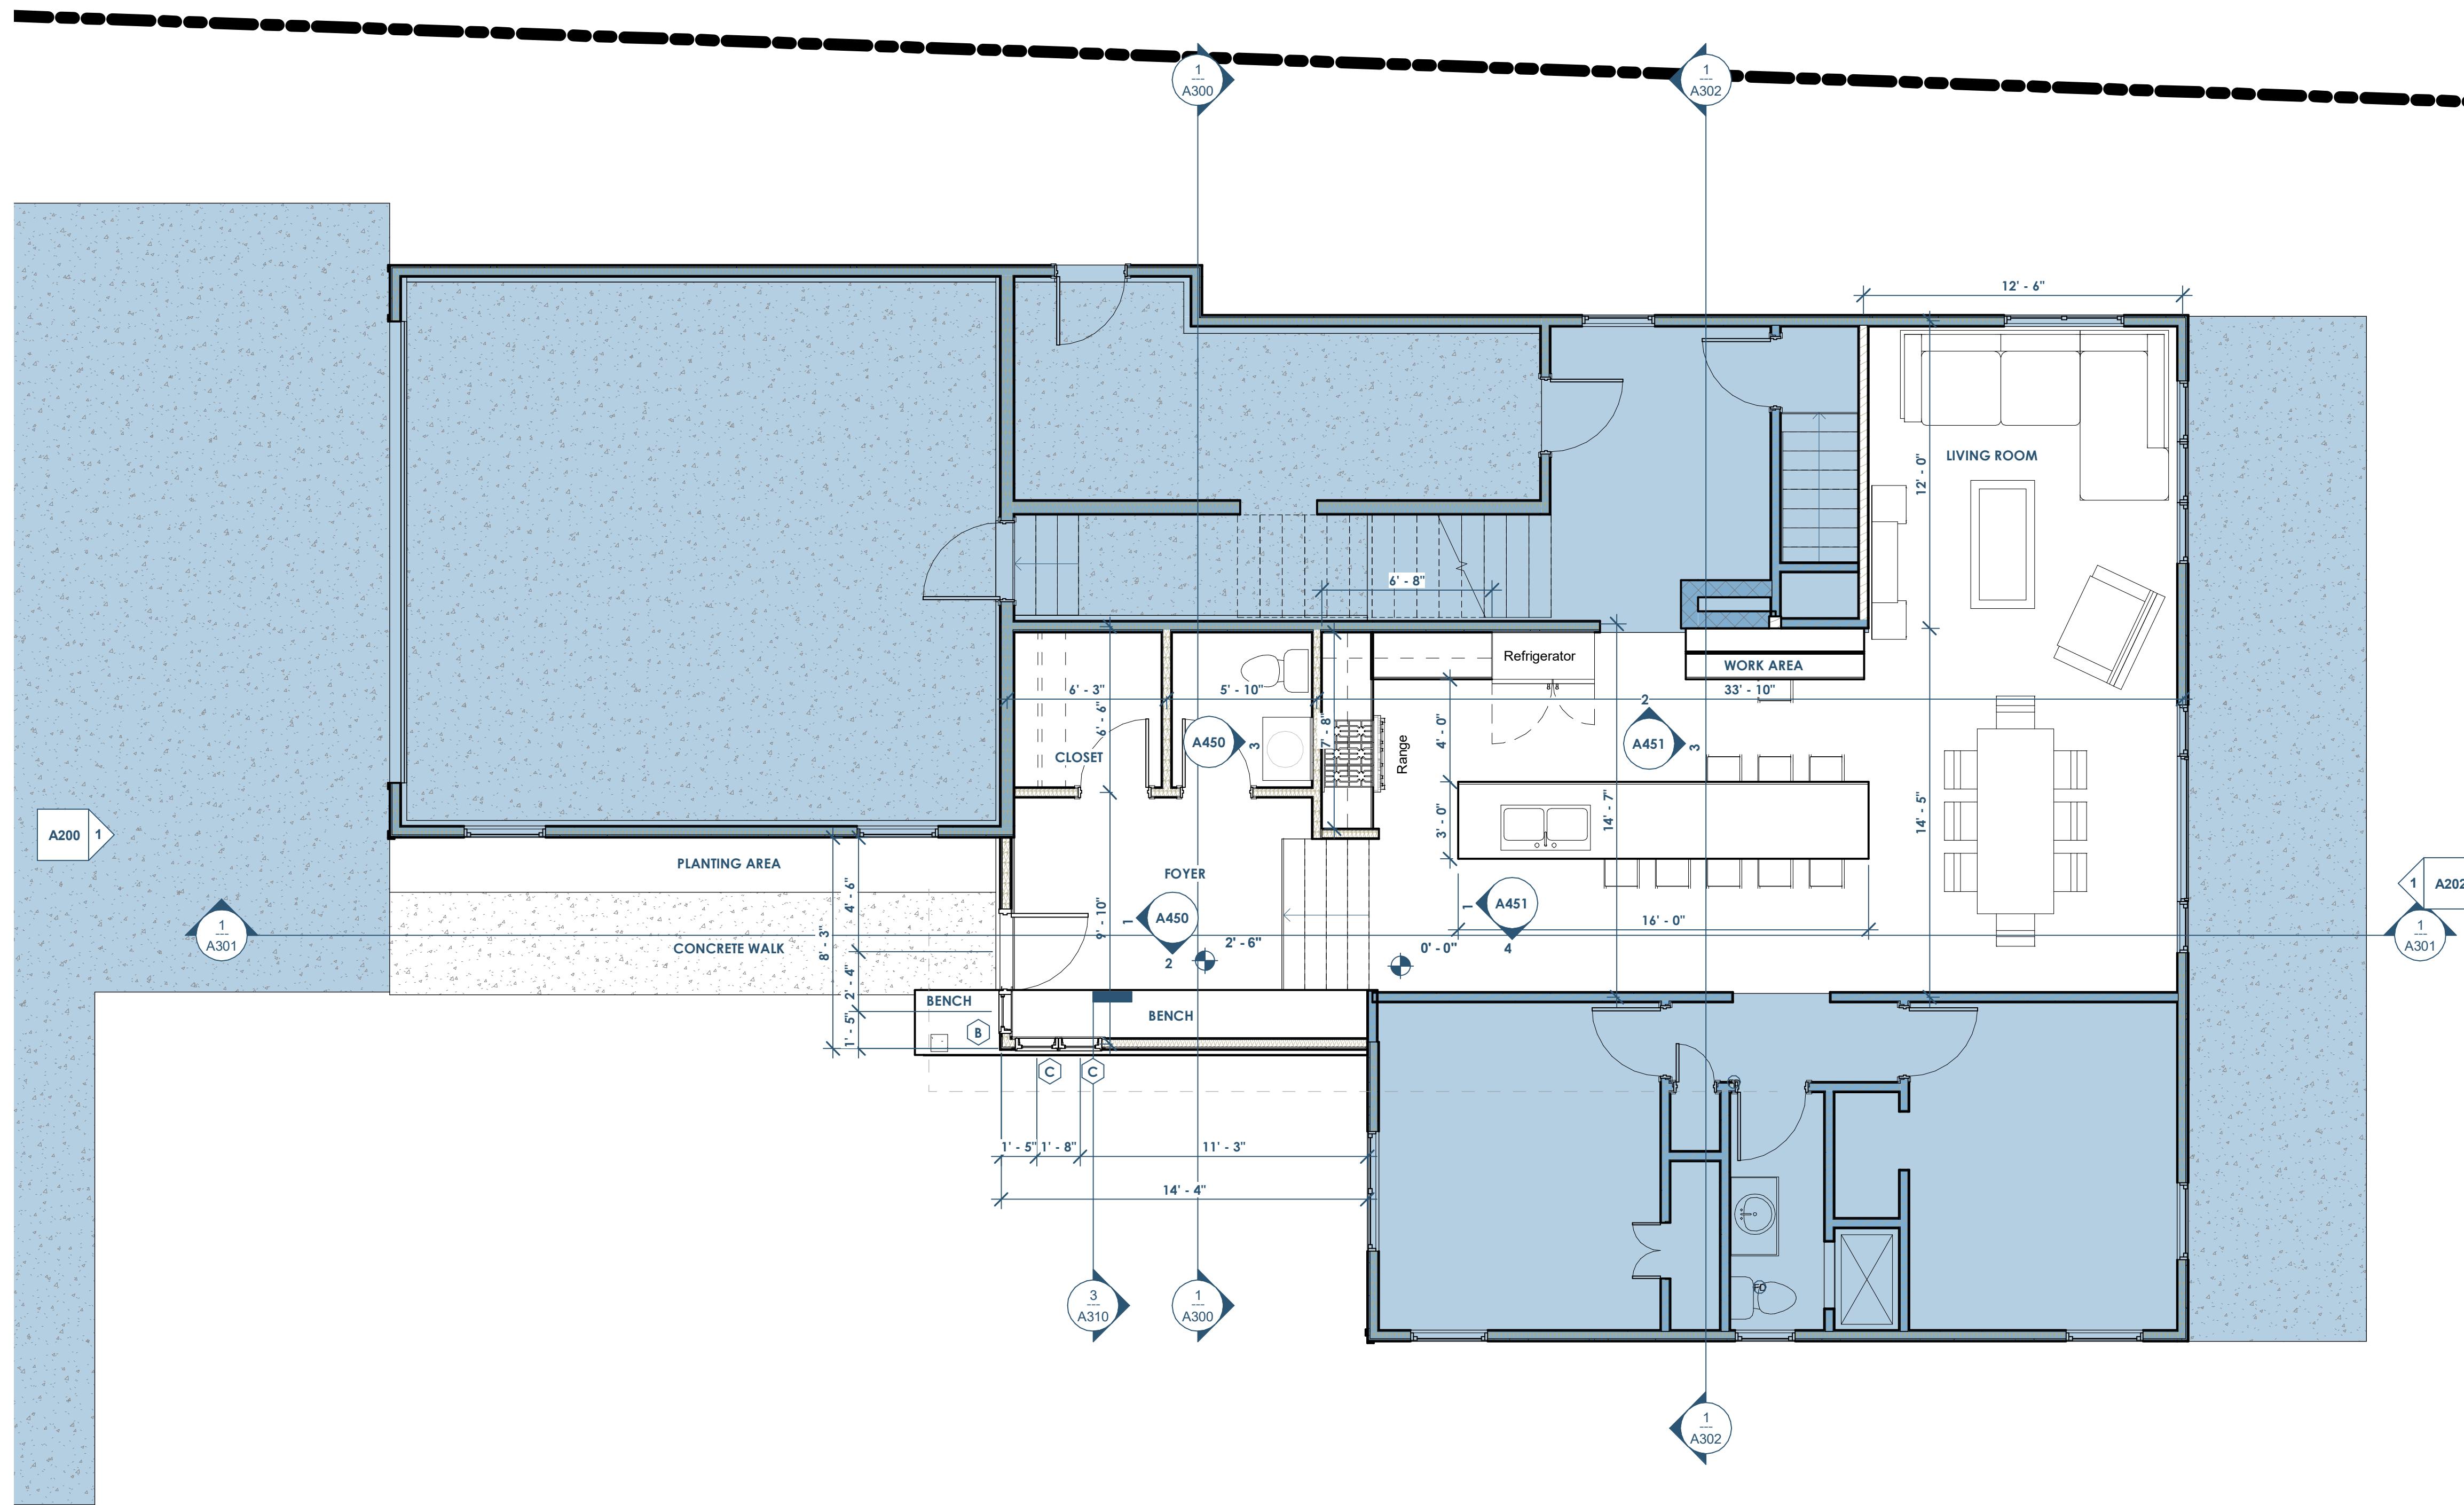

(1) FLOOR PLAN - 1ST
1/4" = 1'-0"

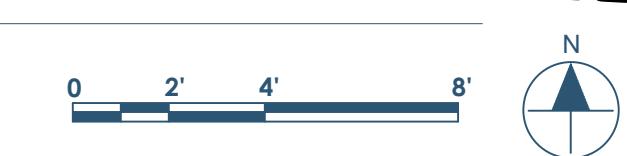

PROPOSED OVERALL FIRST FLOOR PLAN - 08/16/2019
KERN RESIDENCE
N6790 SHOREWOOD HILLS RD - LAKE MILLS, WI 53551




5 4 3 2 1

C C

B B

A A

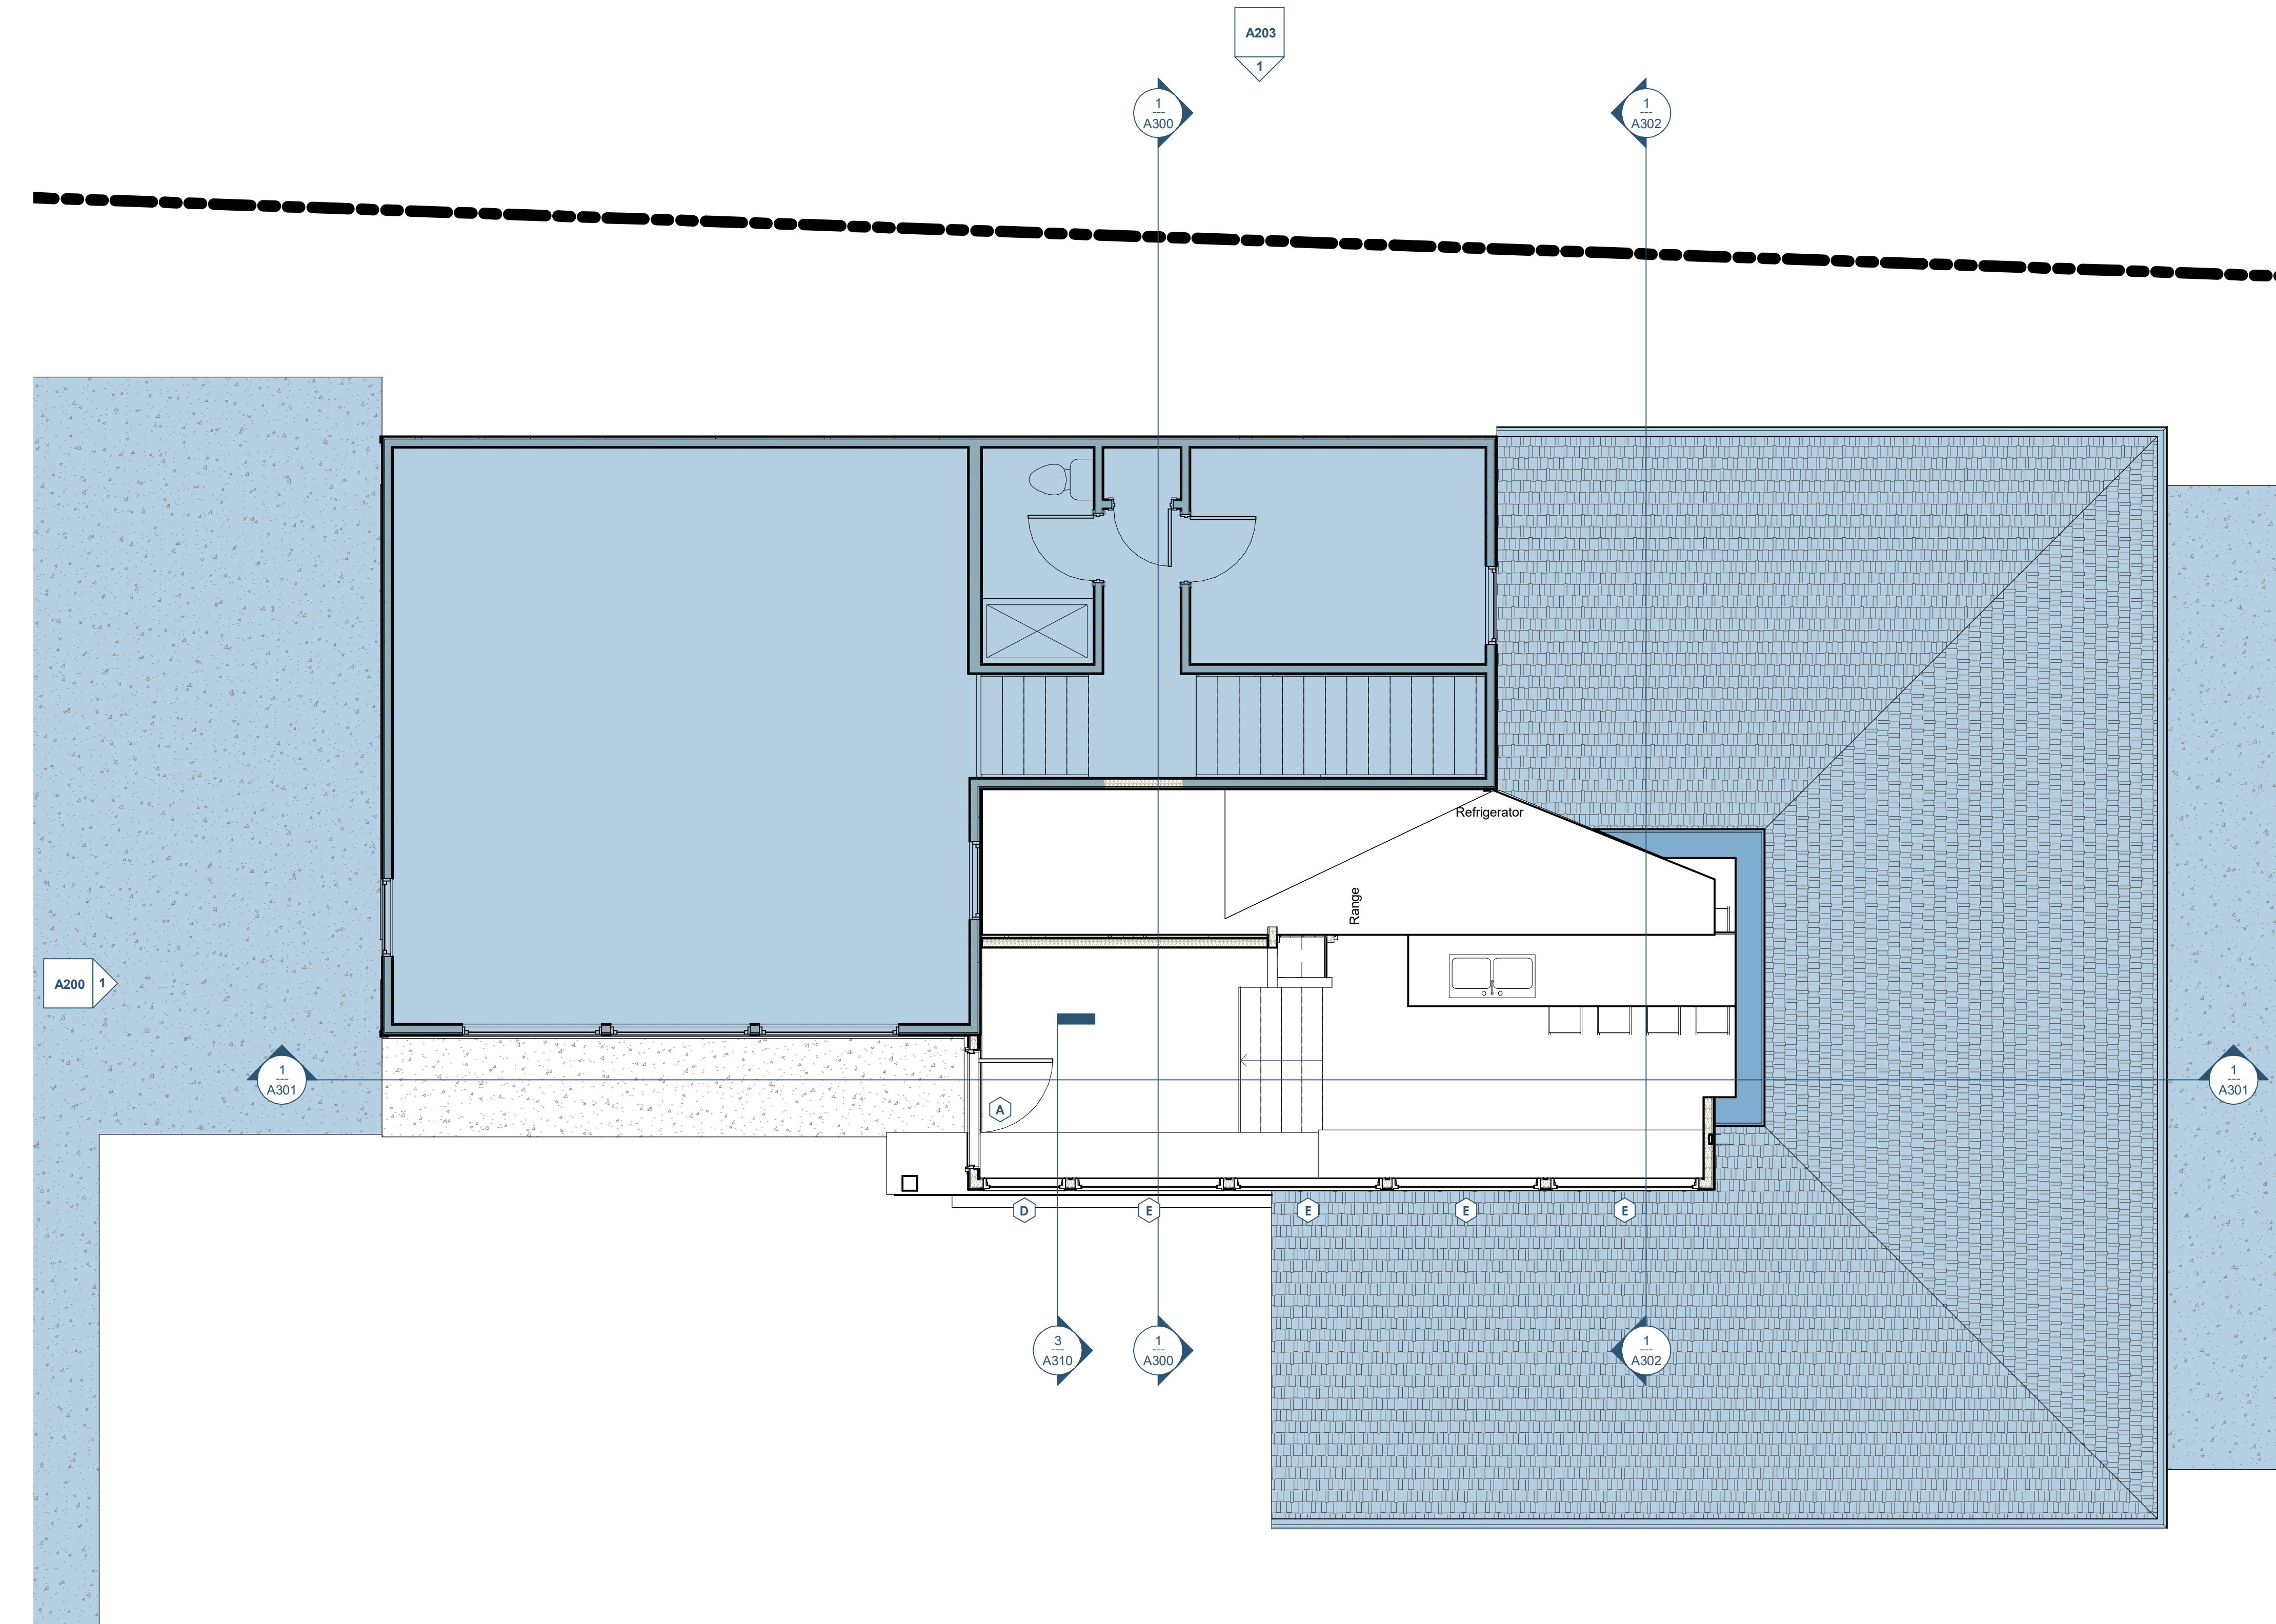

(1) FLOOR PLAN - 2ND FLOOR
1/4" = 1'-0"



PROPOSED OVERALL UPPER FLOOR PLAN - 08/16/2019
KERN RESIDENCE
N6790 SHOREWOOD HILLS RD - LAKE MILLS, WI 53551

A102

5

4

3

2

1

C

C

B

B

A

A


(1) FLOOR PLAN - ROOF
1/4" = 1'-0"



Architect: OpeningDesign
316 W Washington Ave | Suite 675
Madison, WI 53703
ryan@openingdesign.com | 773.425.6456

PROPOSED OVERALL ROOF PLAN - 08/16/2019
KERN RESIDENCE
N6790 SHOREWOOD HILLS RD - LAKE MILLS, WI 53551

A103

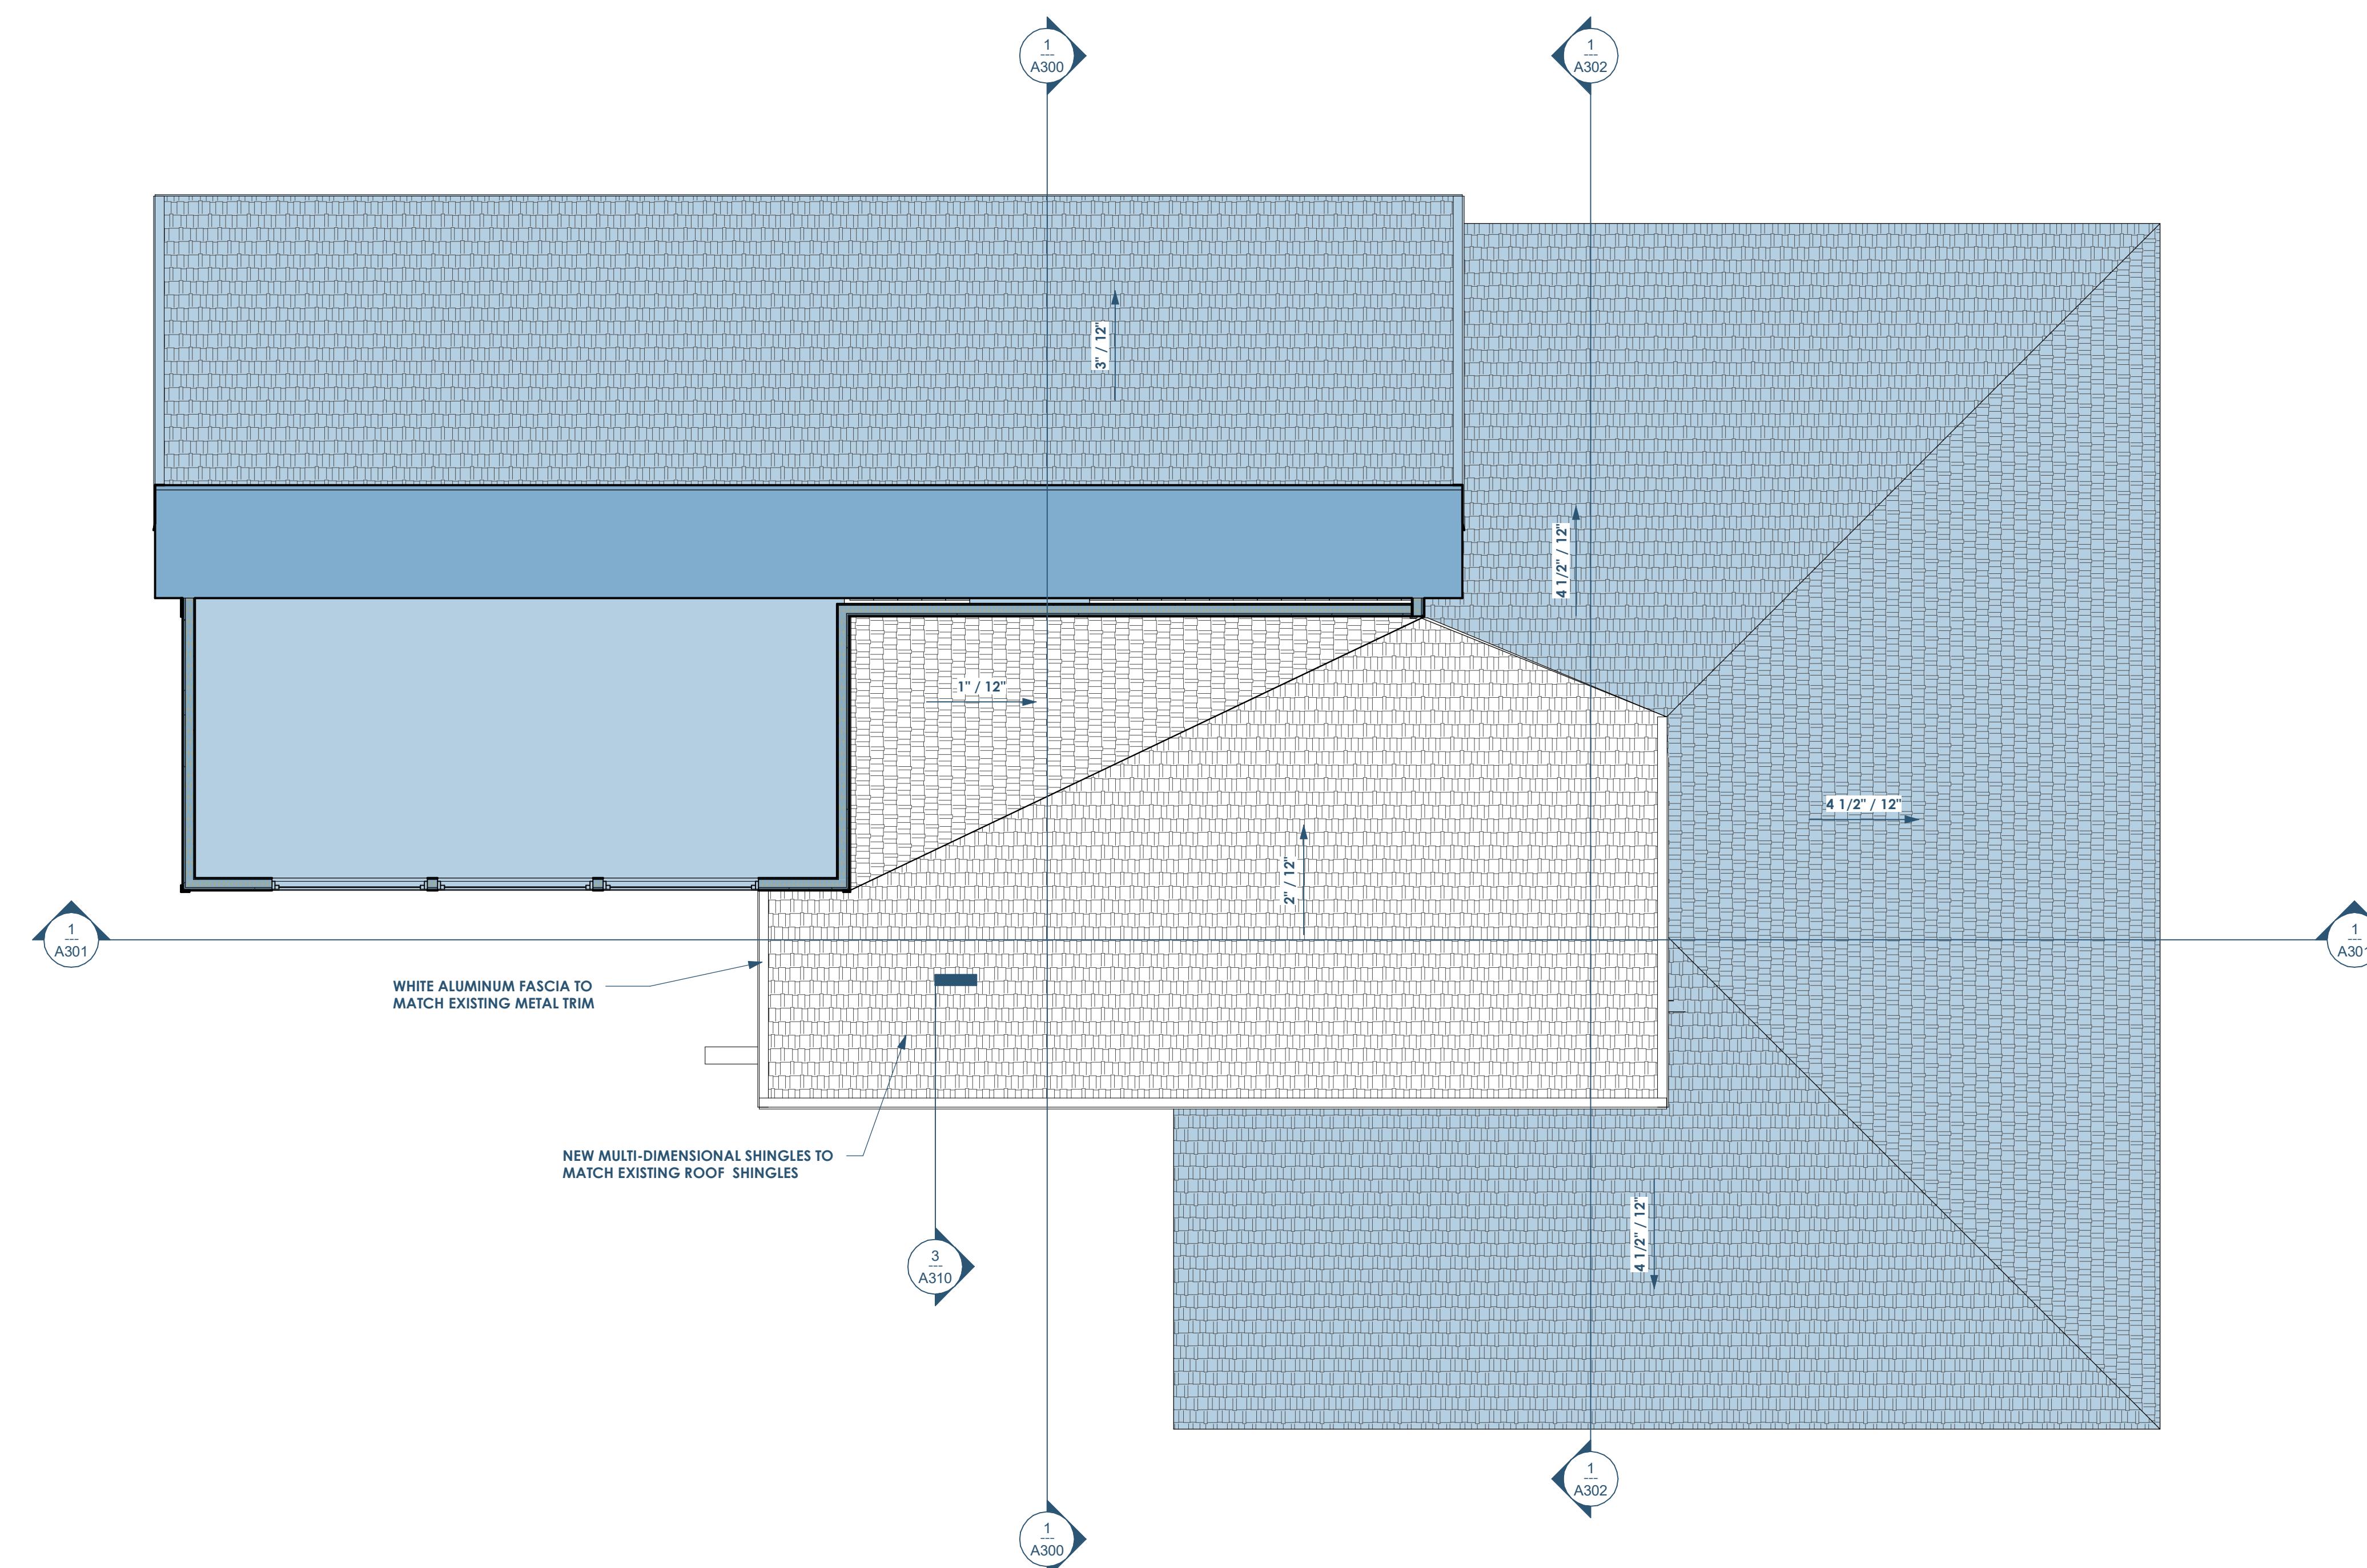

5

4

3

2

1

5

4

3

2

1

C


C

B

B

A

A

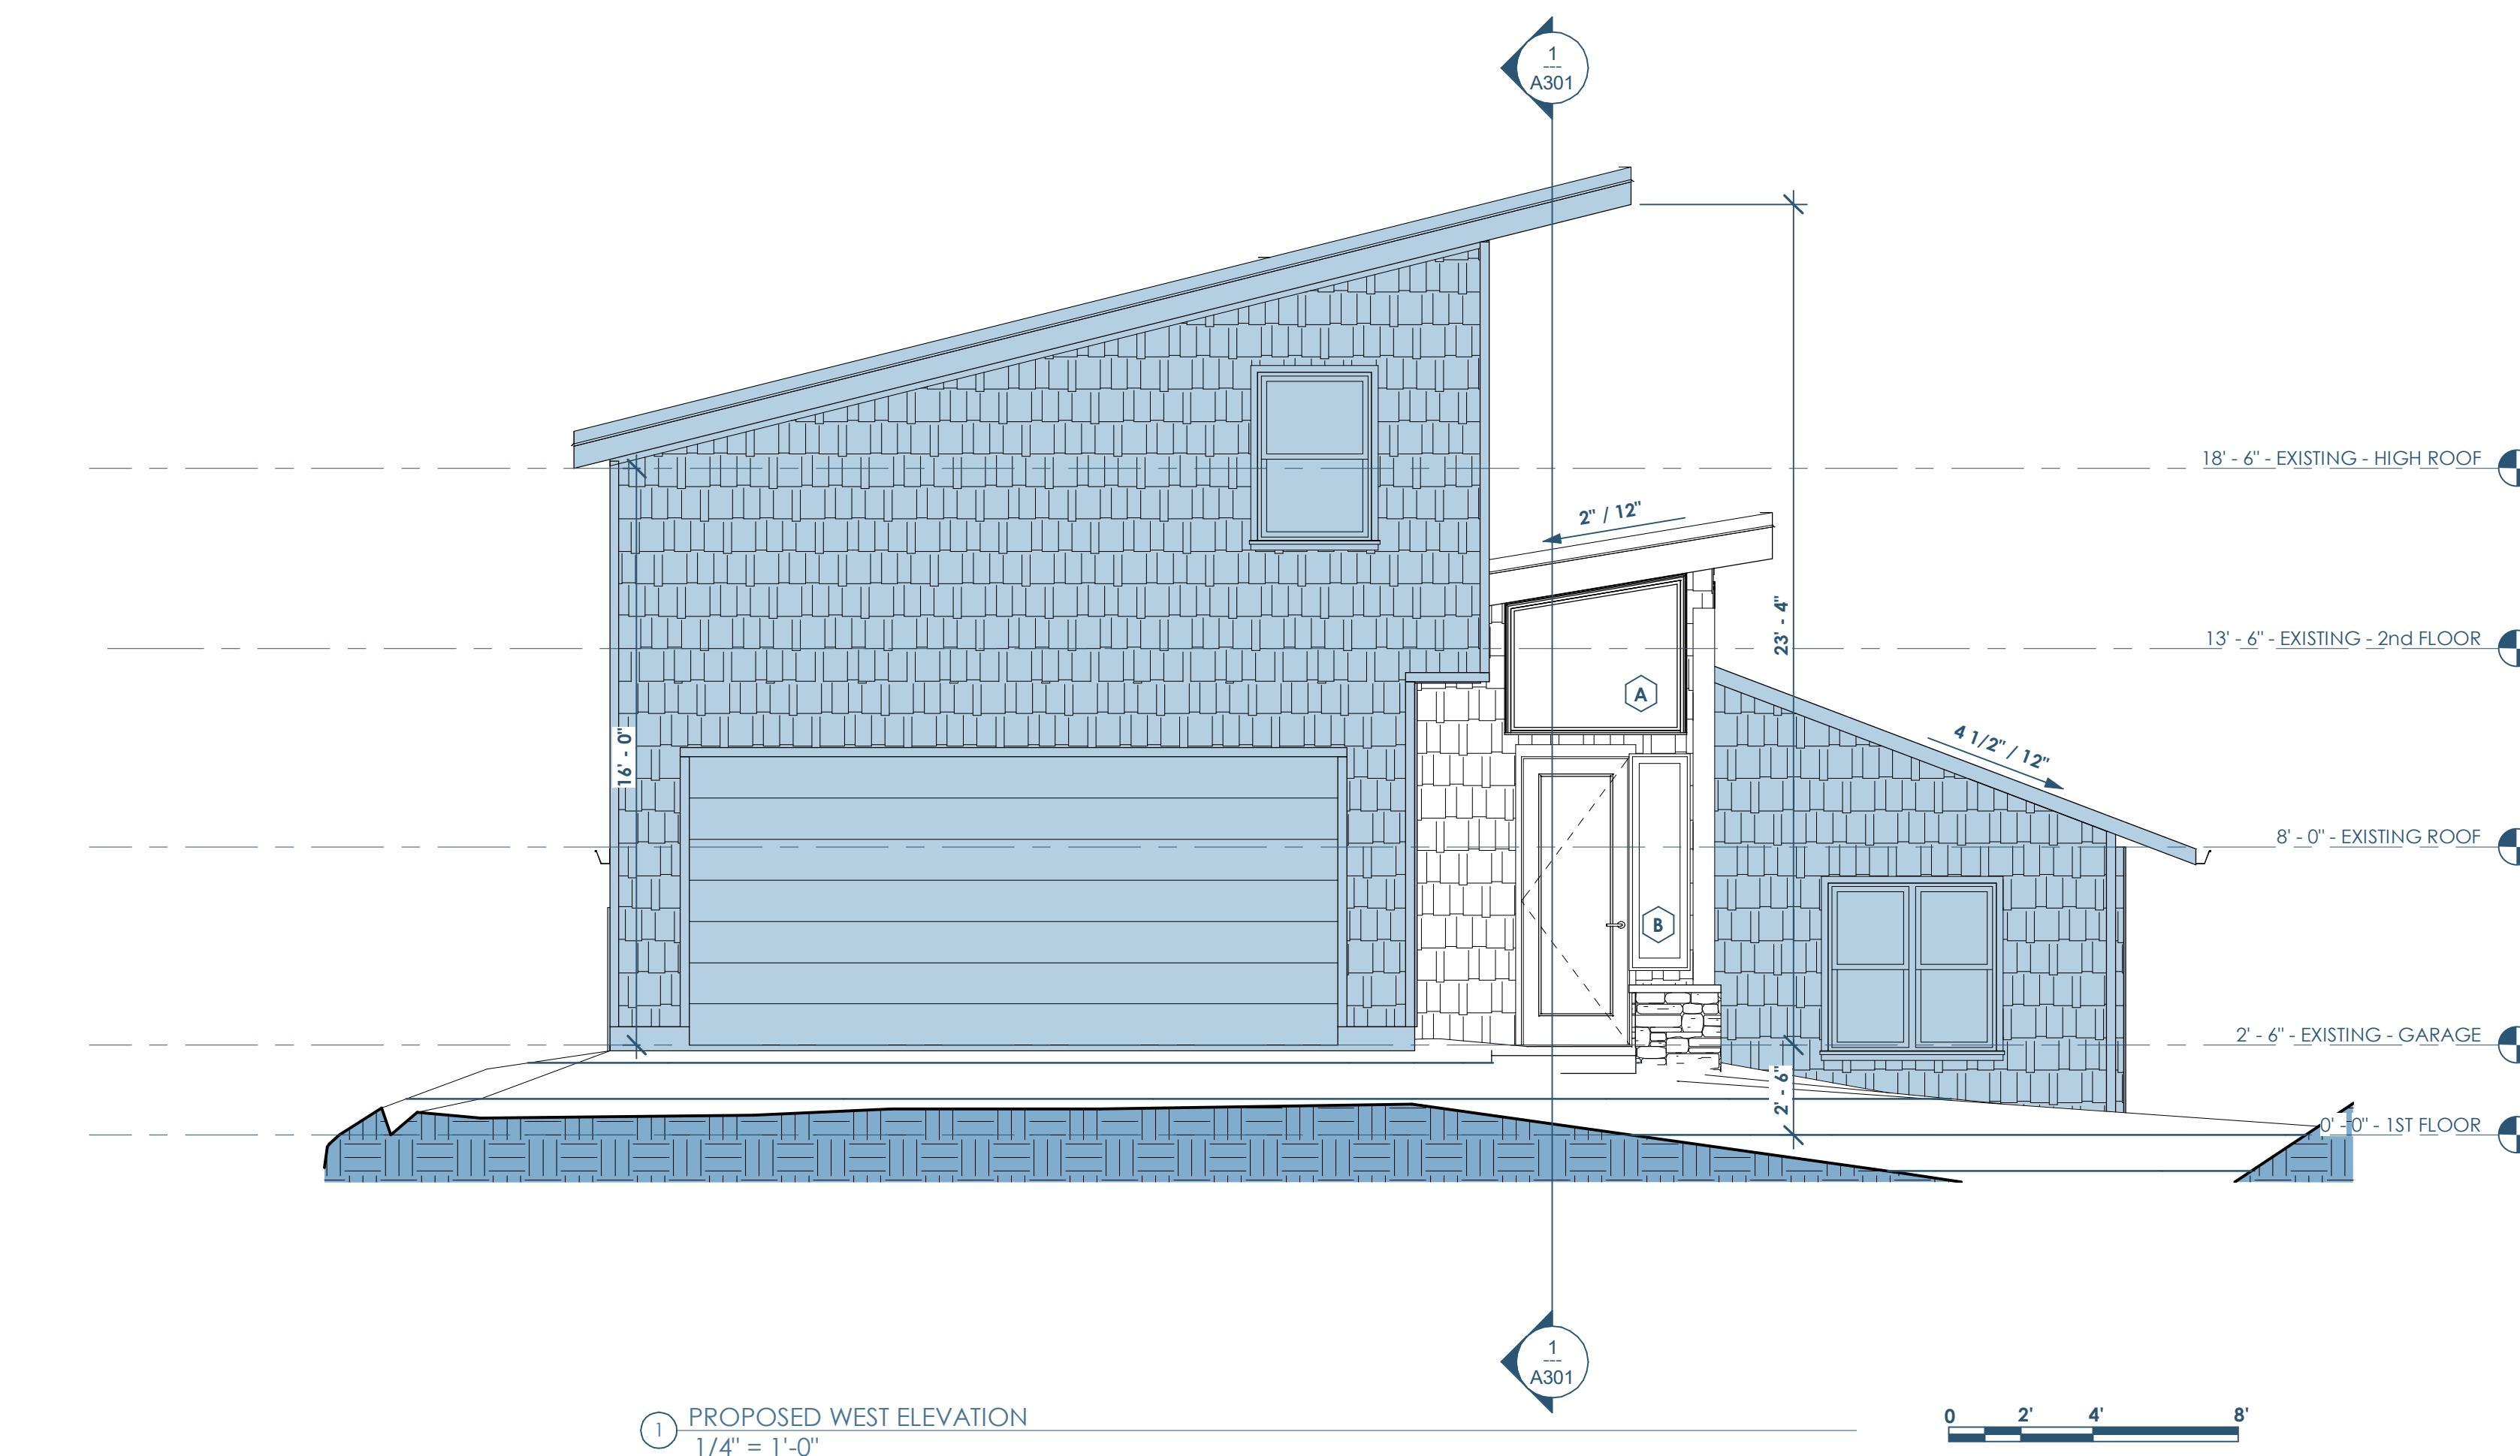

Architect: OpeningDesign
316 W Washington Ave | Suite 675
Madison, WI 53703
ryan@openingdesign.com | 773.425.6456

BUILDING ELEVATIONS - 08/16/2019
KERN RESIDENCE
N6790 SHOREWOOD HILLS RD - LAKE MILLS, WI 53551

A200

5

4

3

2

1

C


C

B

B

A

A

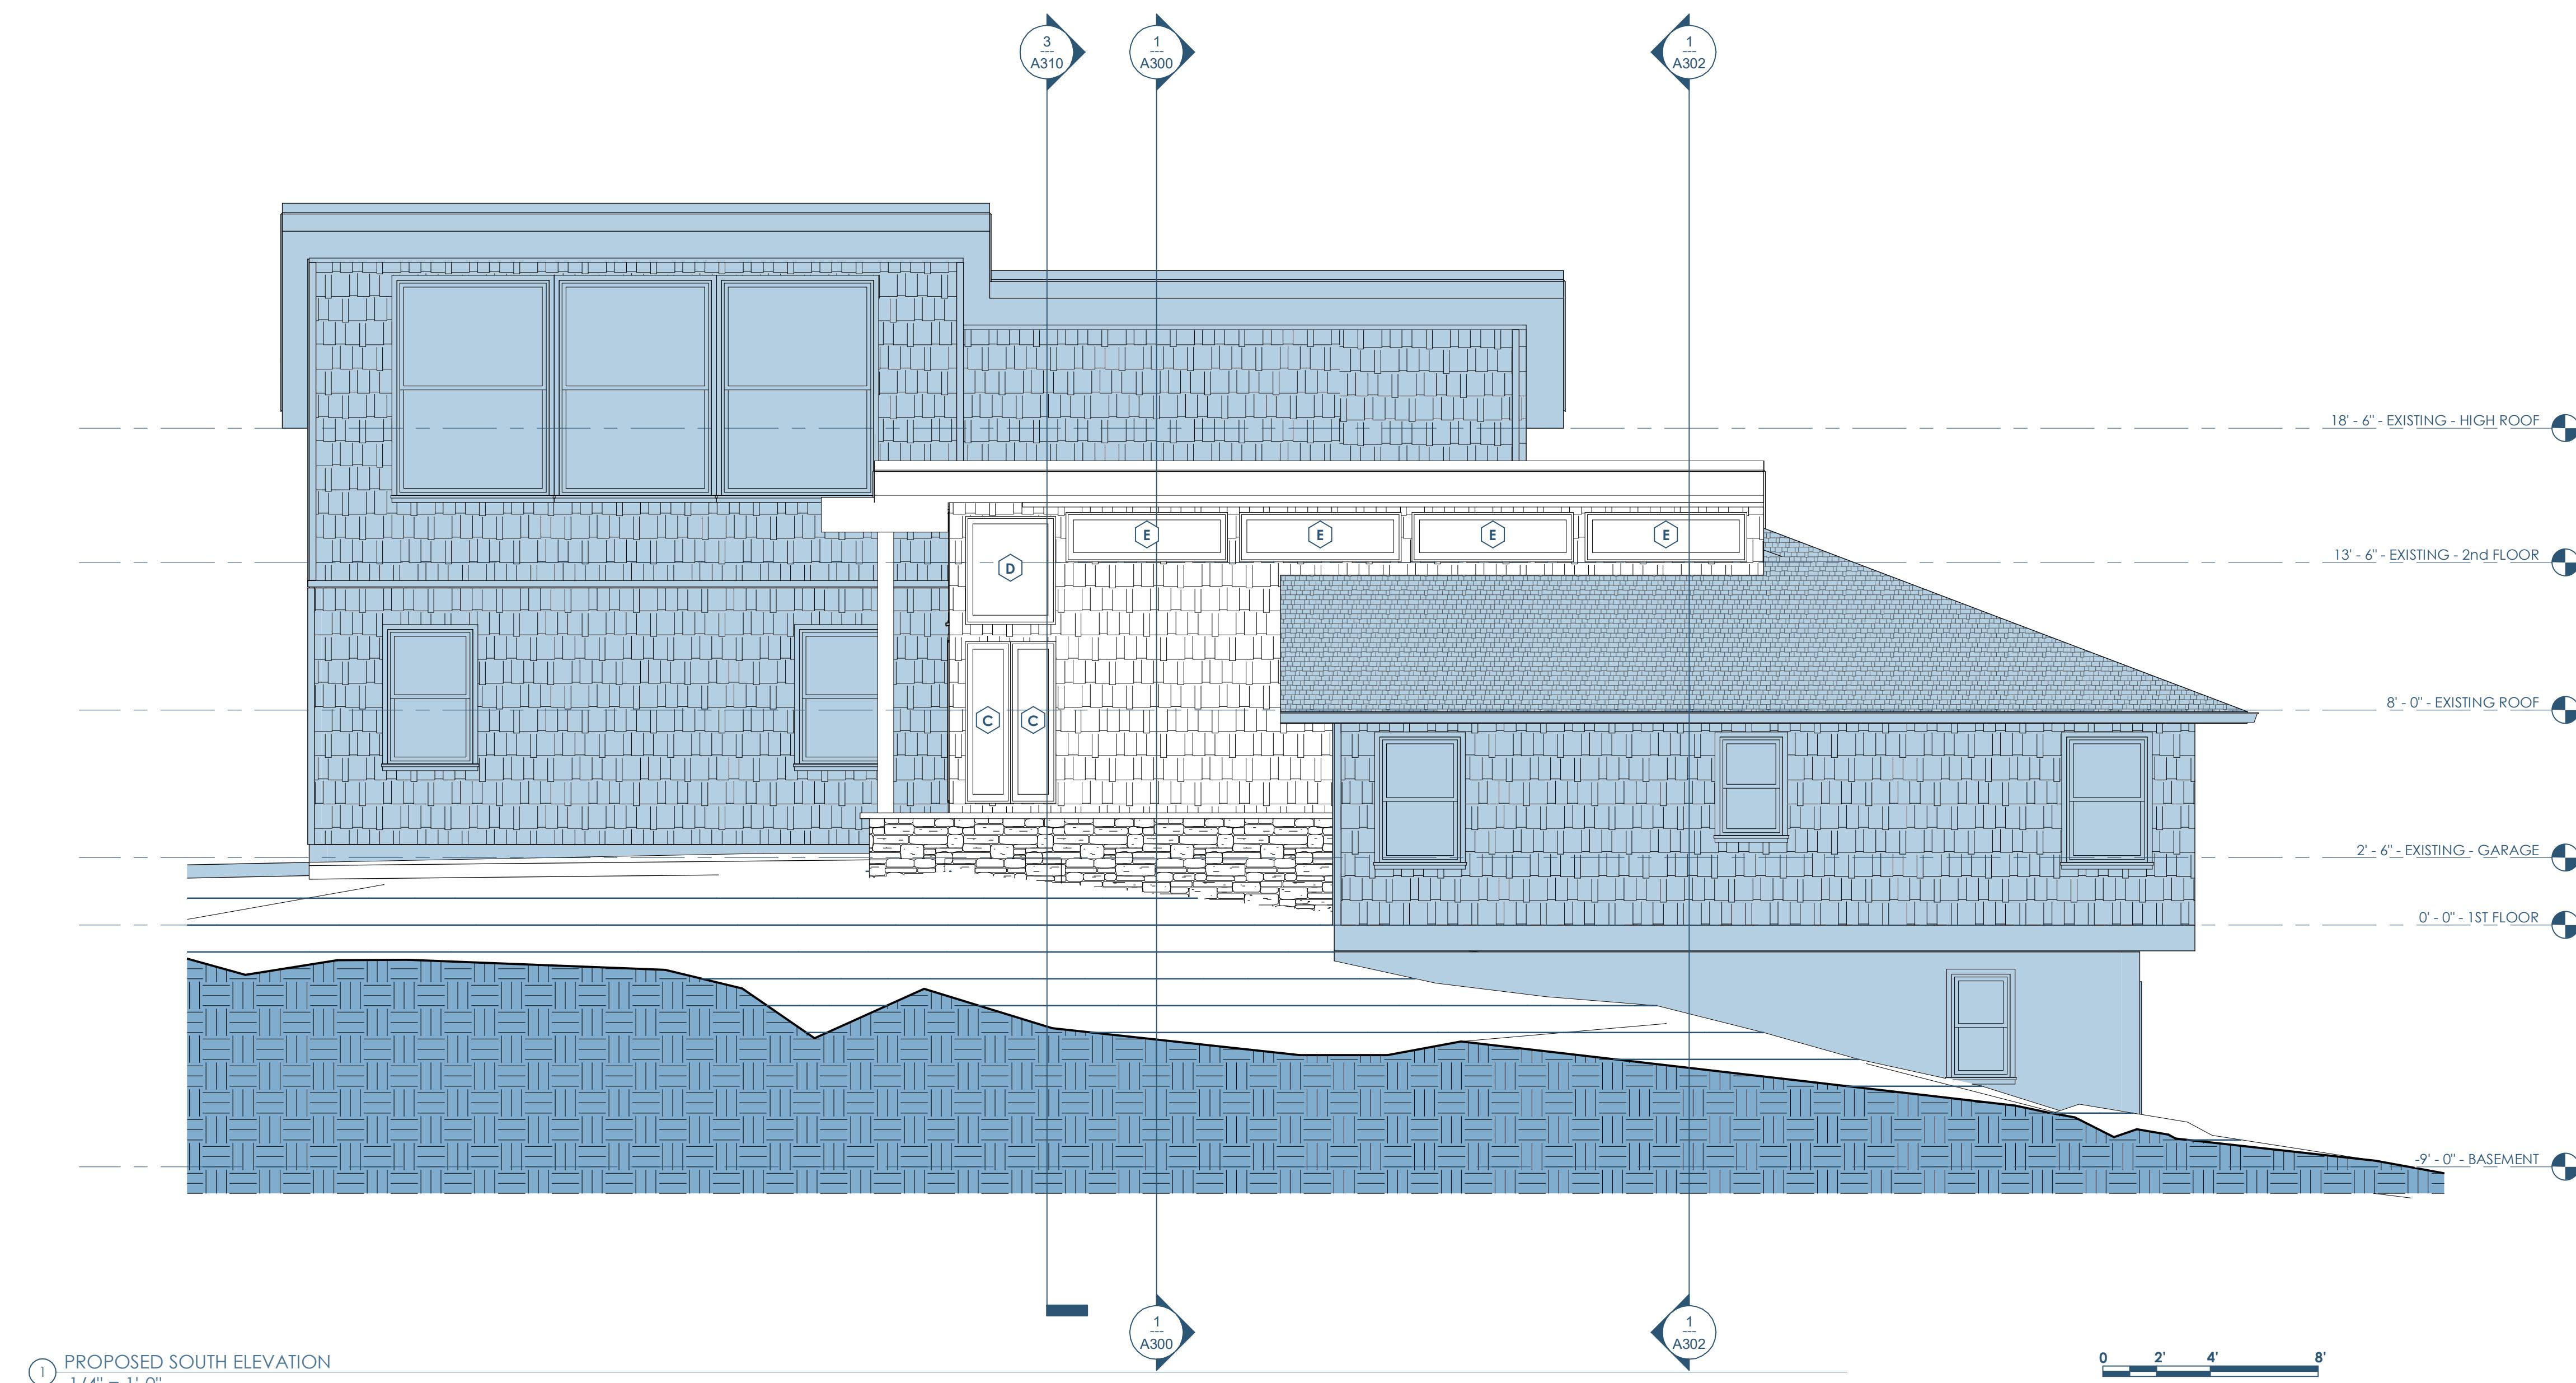

Architect: OpeningDesign
316 W Washington Ave | Suite 675
Madison, WI 53703
ryan@openingdesign.com | 773.425.6456

BUILDING ELEVATIONS - 08/16/2019
KERN RESIDENCE
N6790 SHOREWOOD HILLS RD - LAKE MILLS, WI 53551
A201

5

4

3

2

1

C

C

B


B

A

A

(1) PROPOSED EAST ELEVATION
 $1/4'' = 1'-0''$

0' 2' 4' 8'

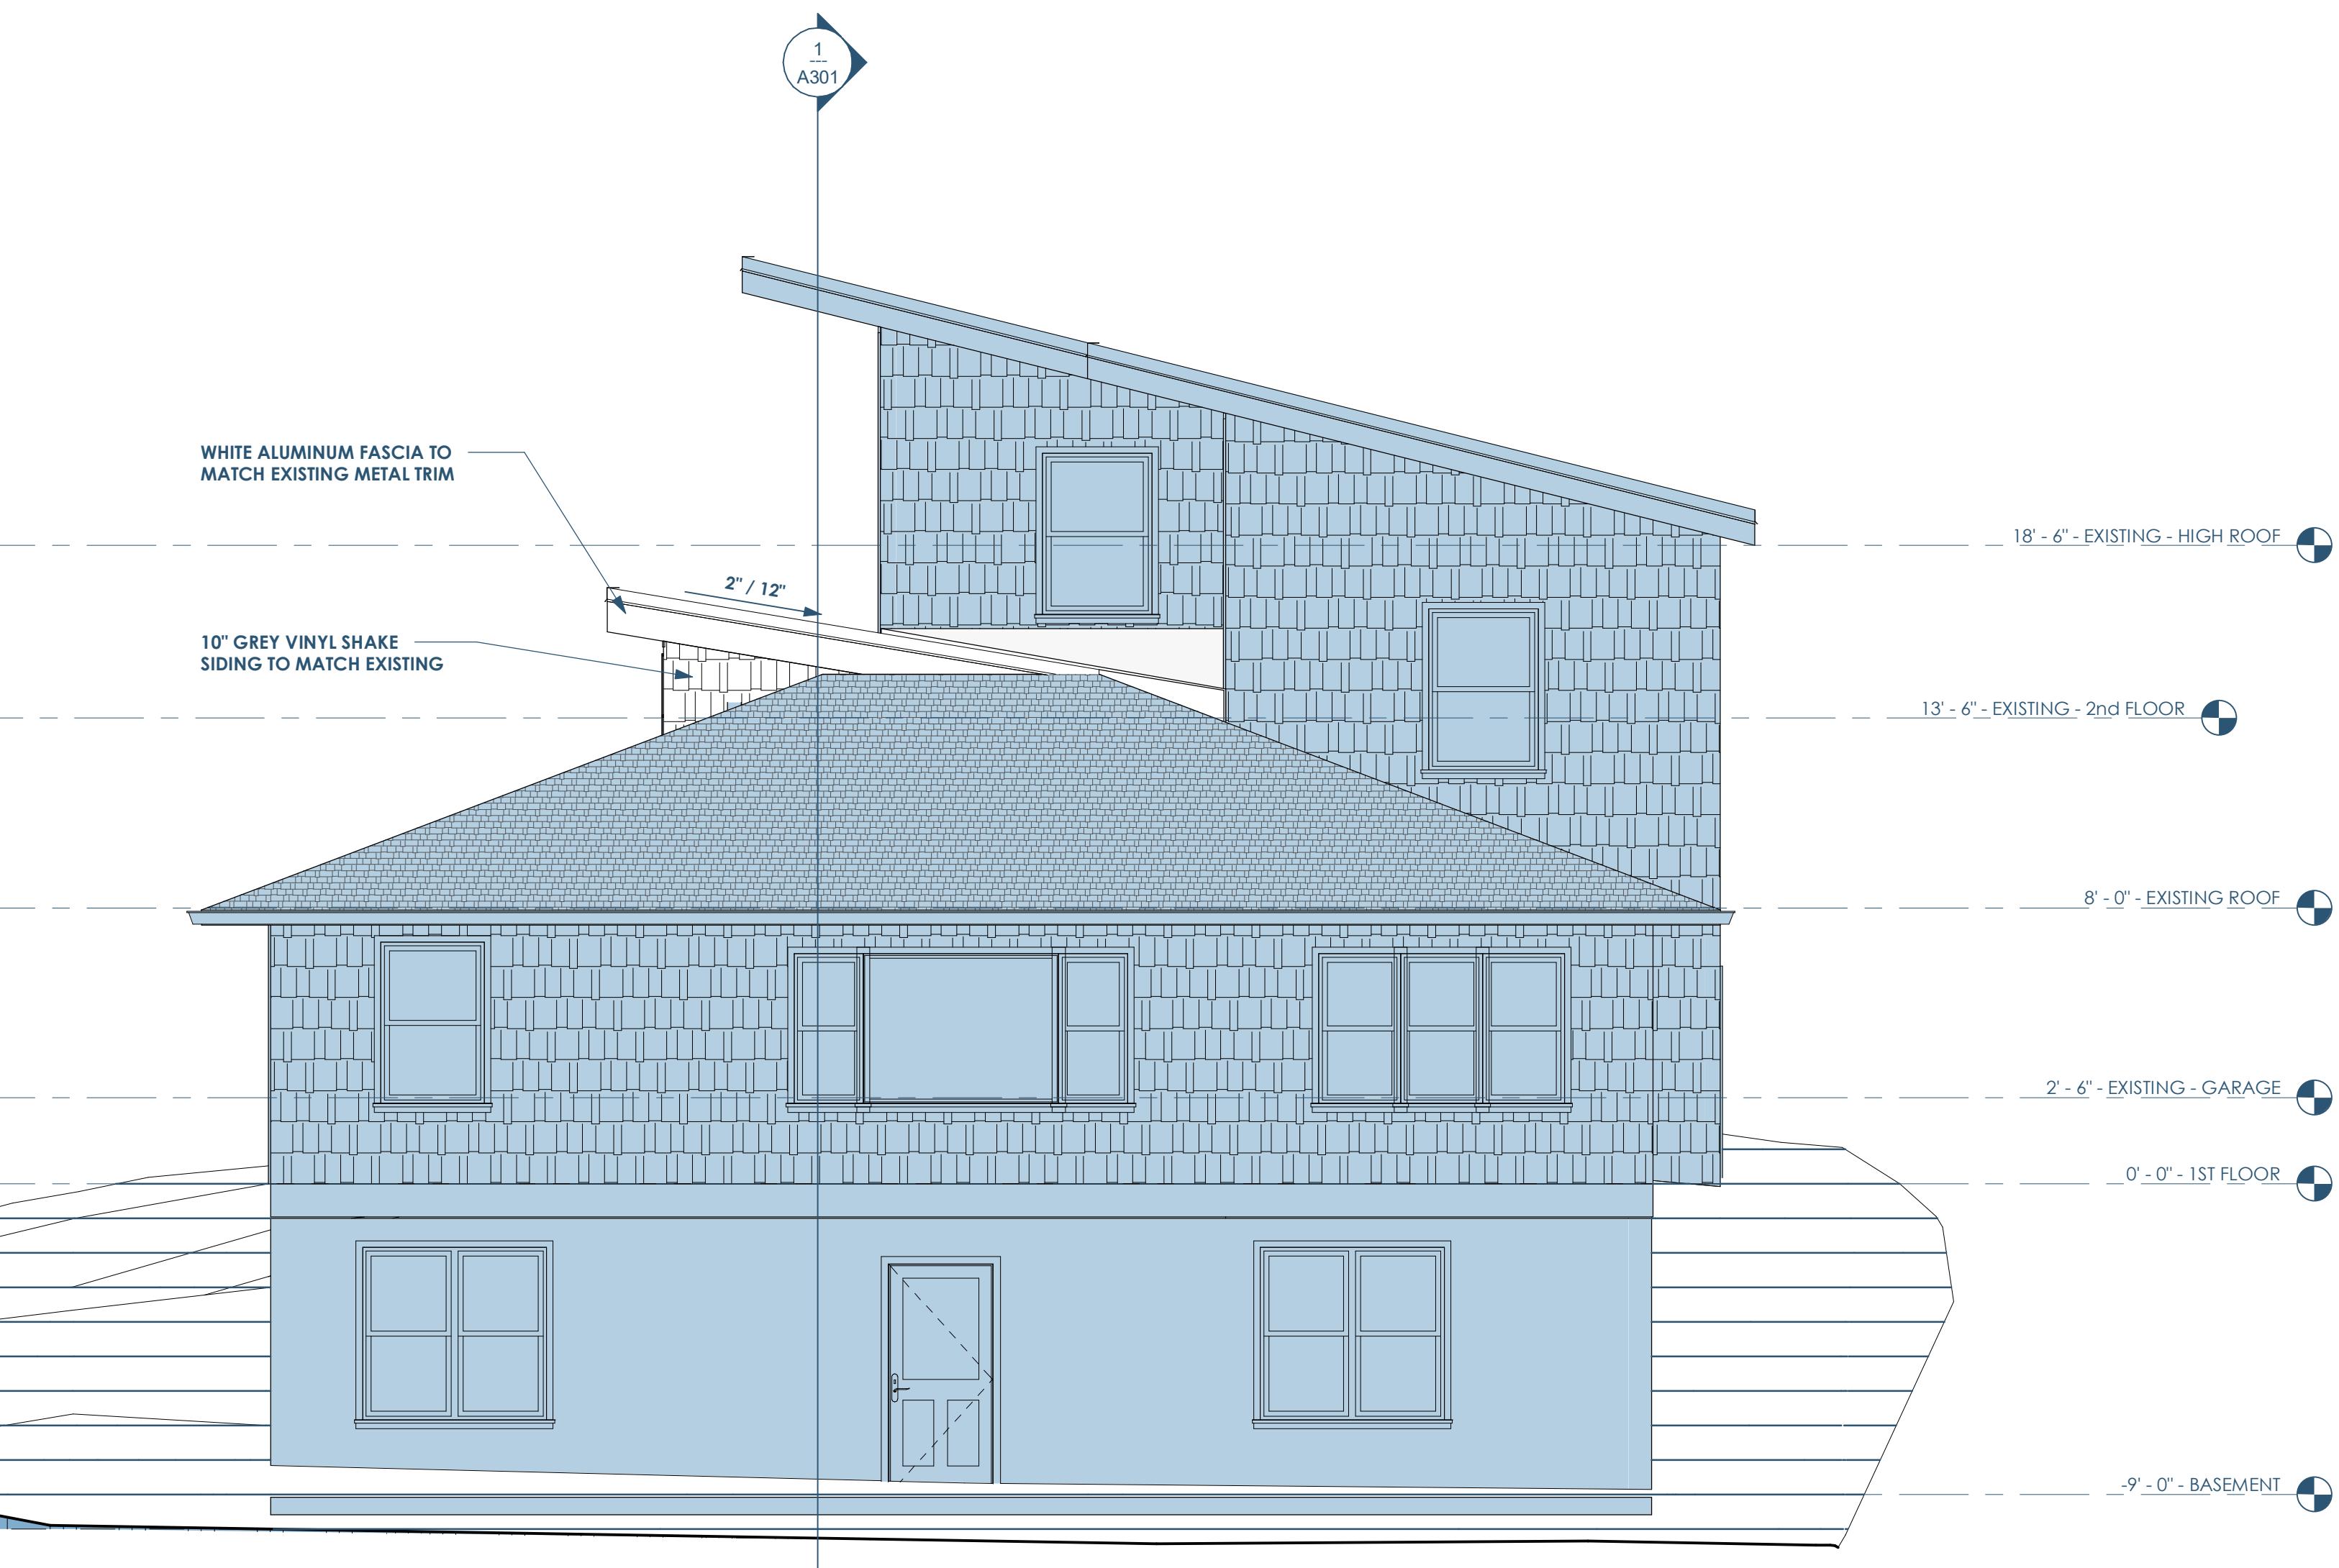

5

4

3

2

1

C


C

B

B

A

A

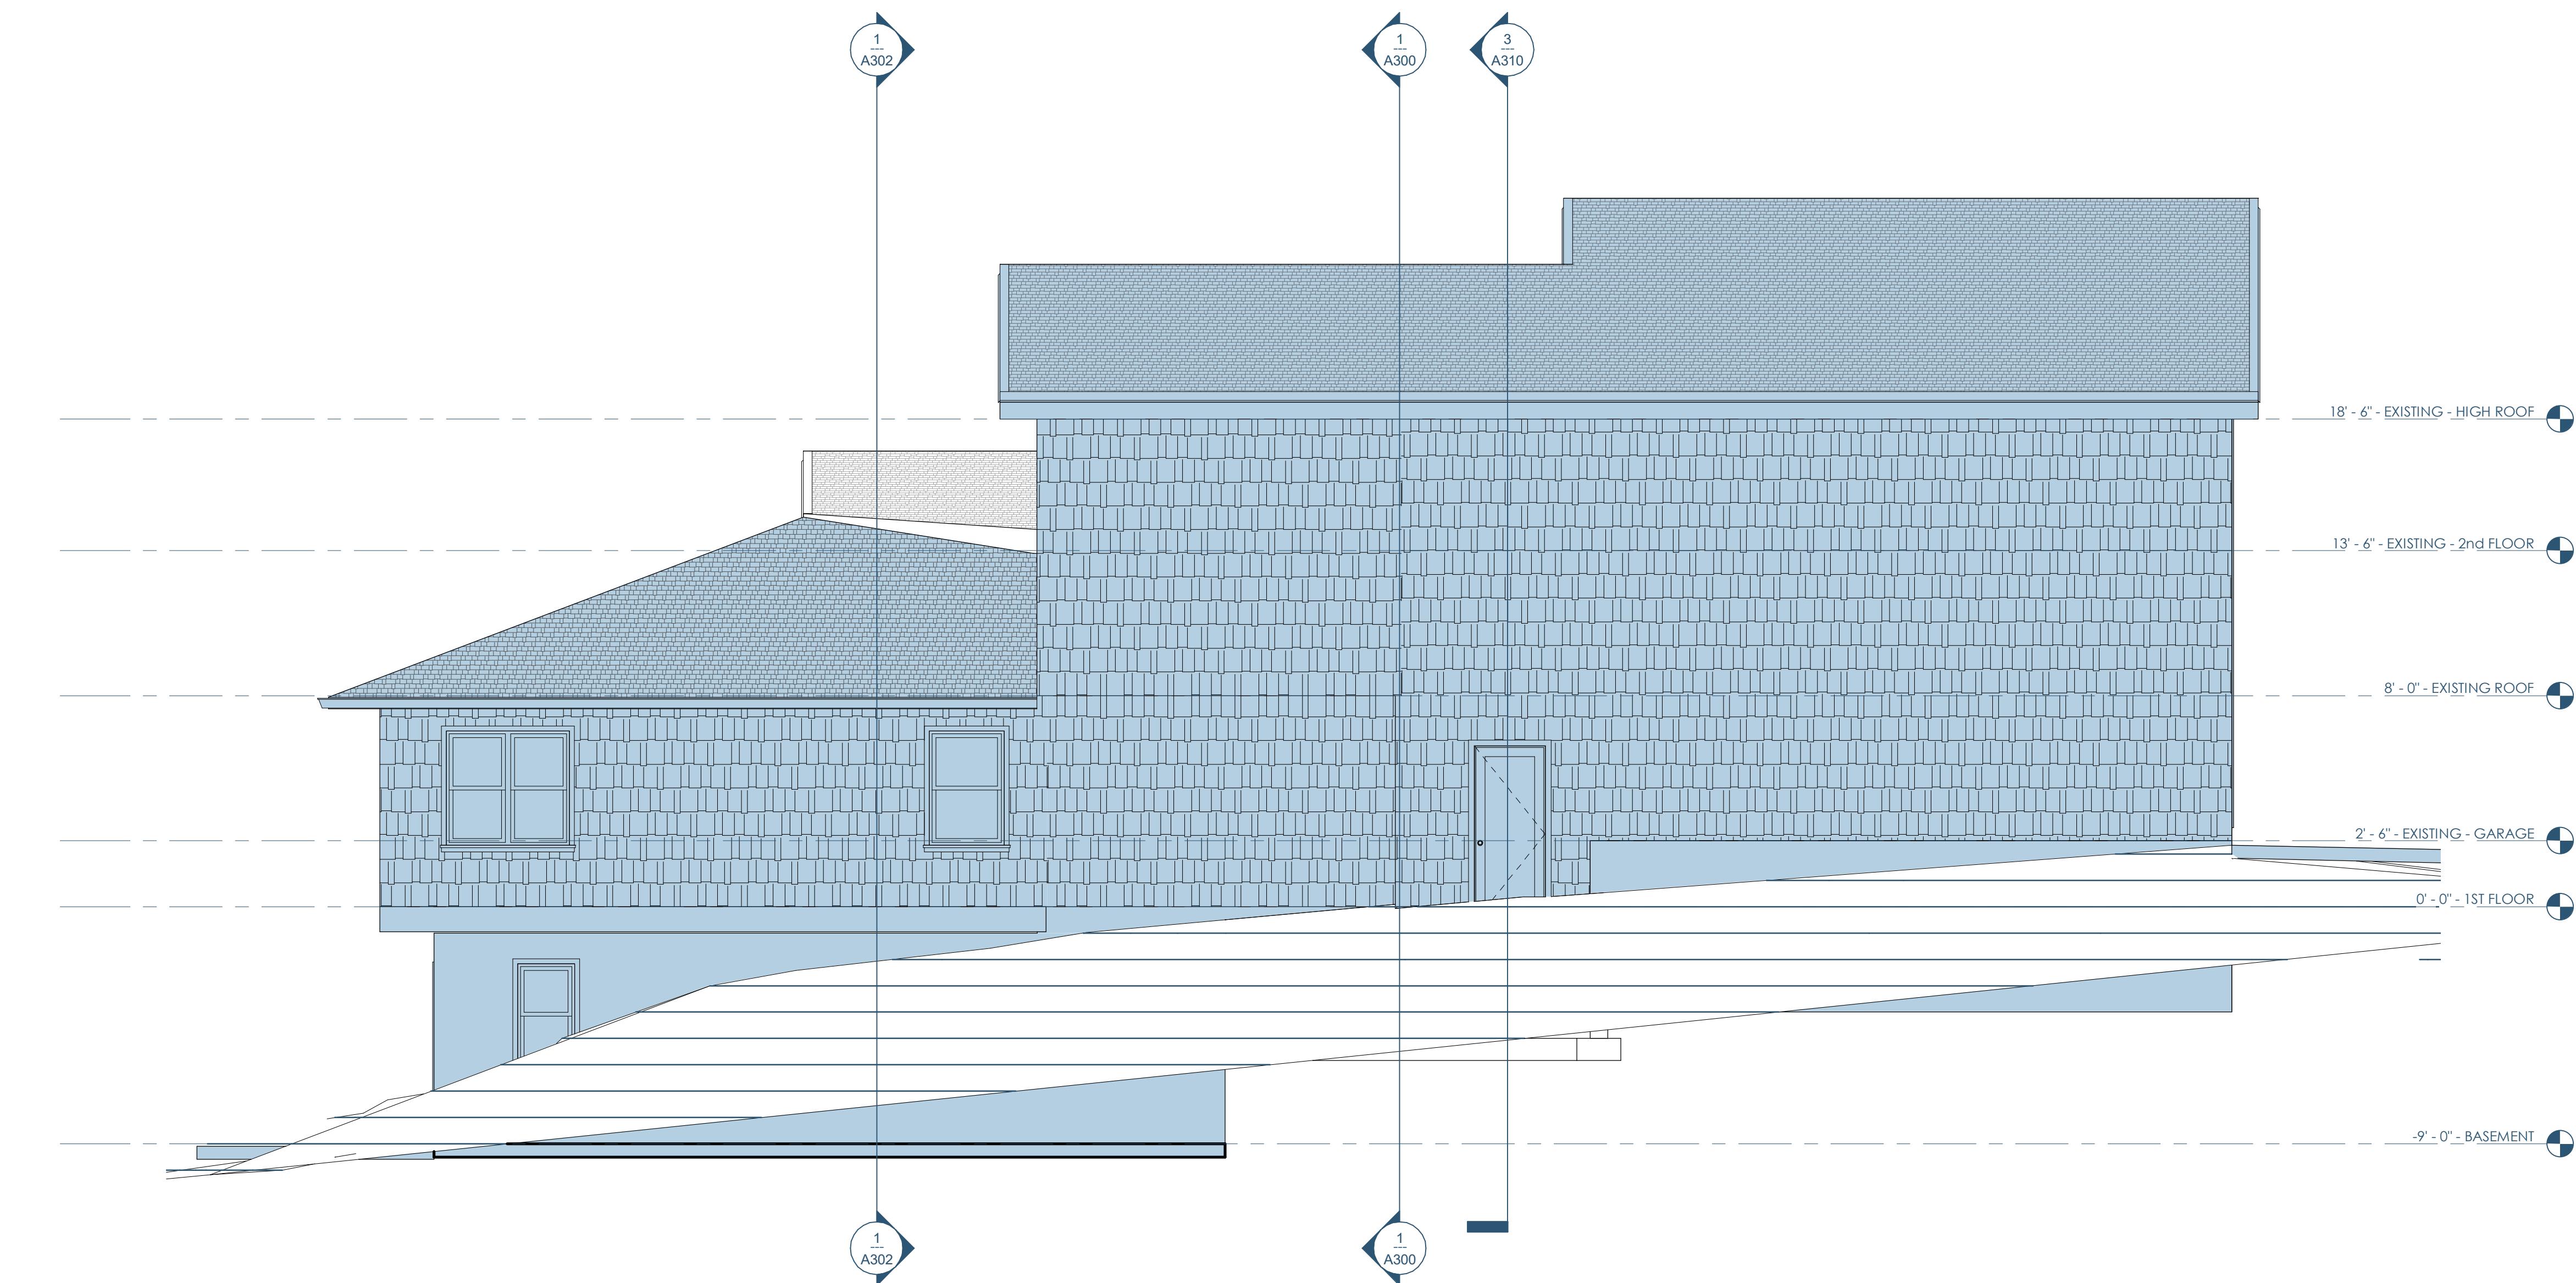

Architect: OpeningDesign
316 W Washington Ave | Suite 675
Madison, WI 53703
ryan@openingdesign.com | 773.425.6456


BUILDING ELEVATIONS - 08/16/2019
KERN RESIDENCE
N6790 SHOREWOOD HILLS RD - LAKE MILLS, WI 53551

A203

5 4 3 2 1

C

C

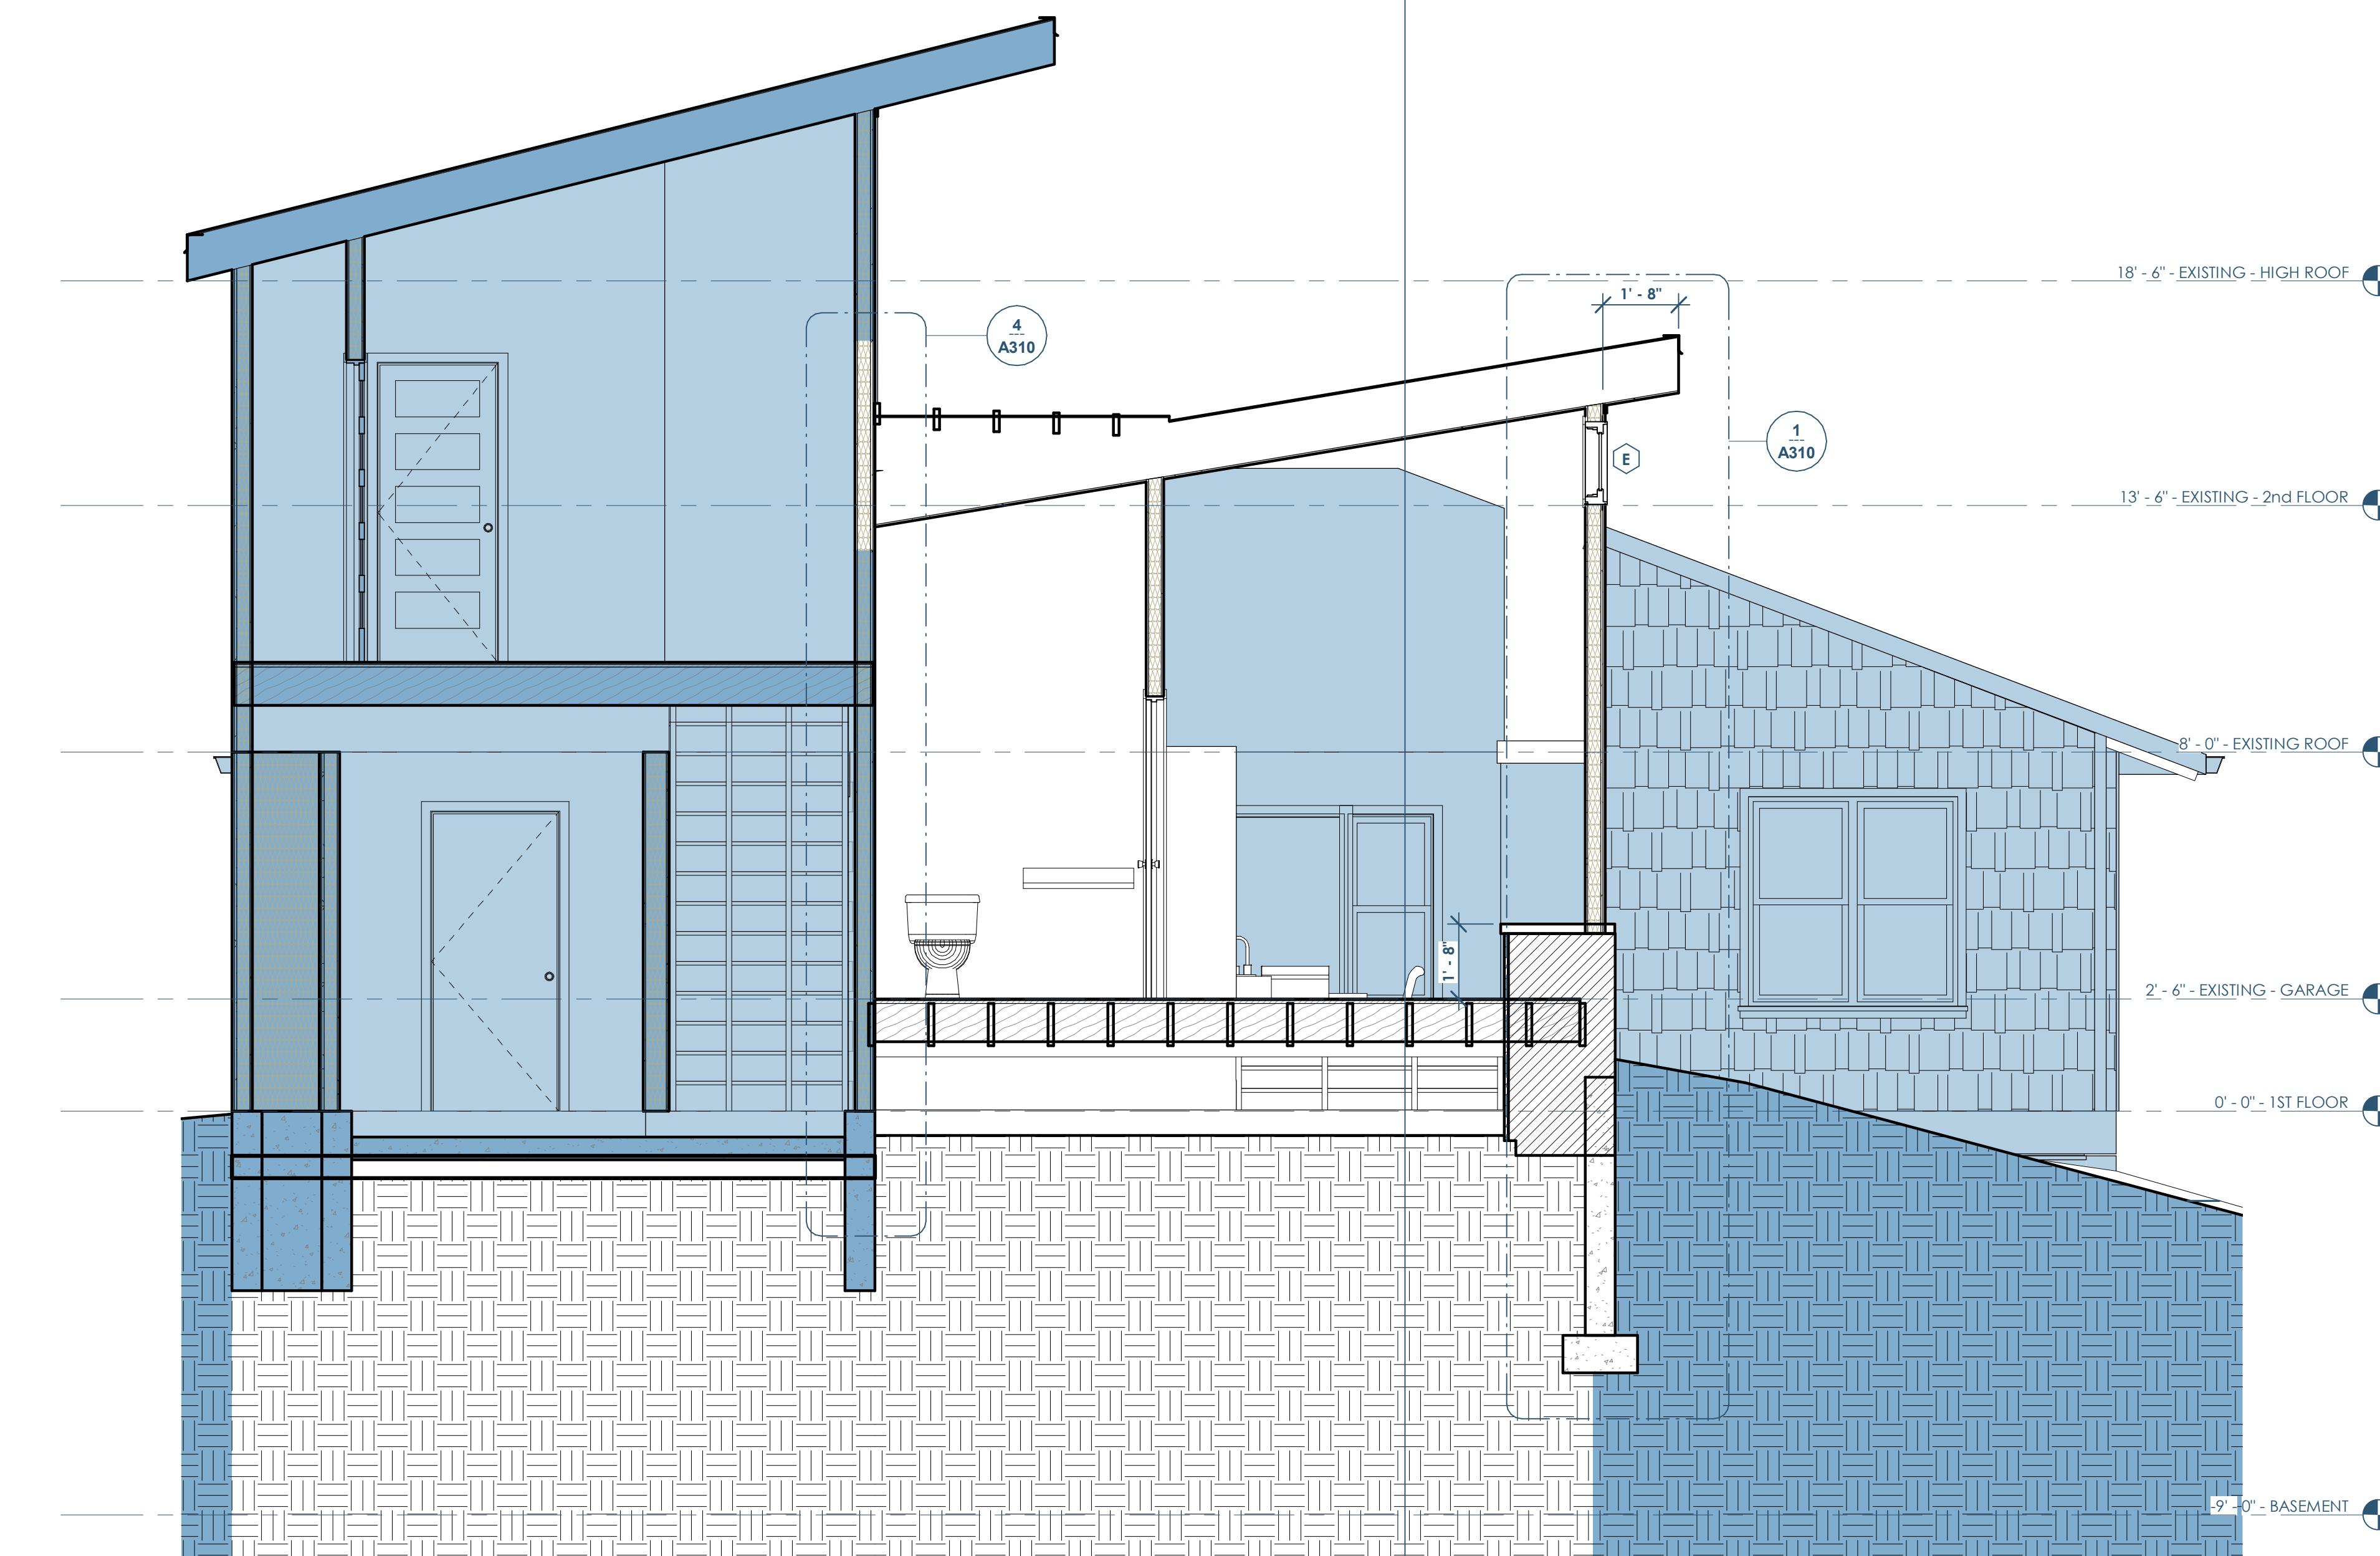


0 2' 4' 6'

BUILDING SECTION - 08/16/2019
KERN RESIDENCE
N6790 SHOREWOOD HILLS RD - LAKE MILLS, WI 53551

A300



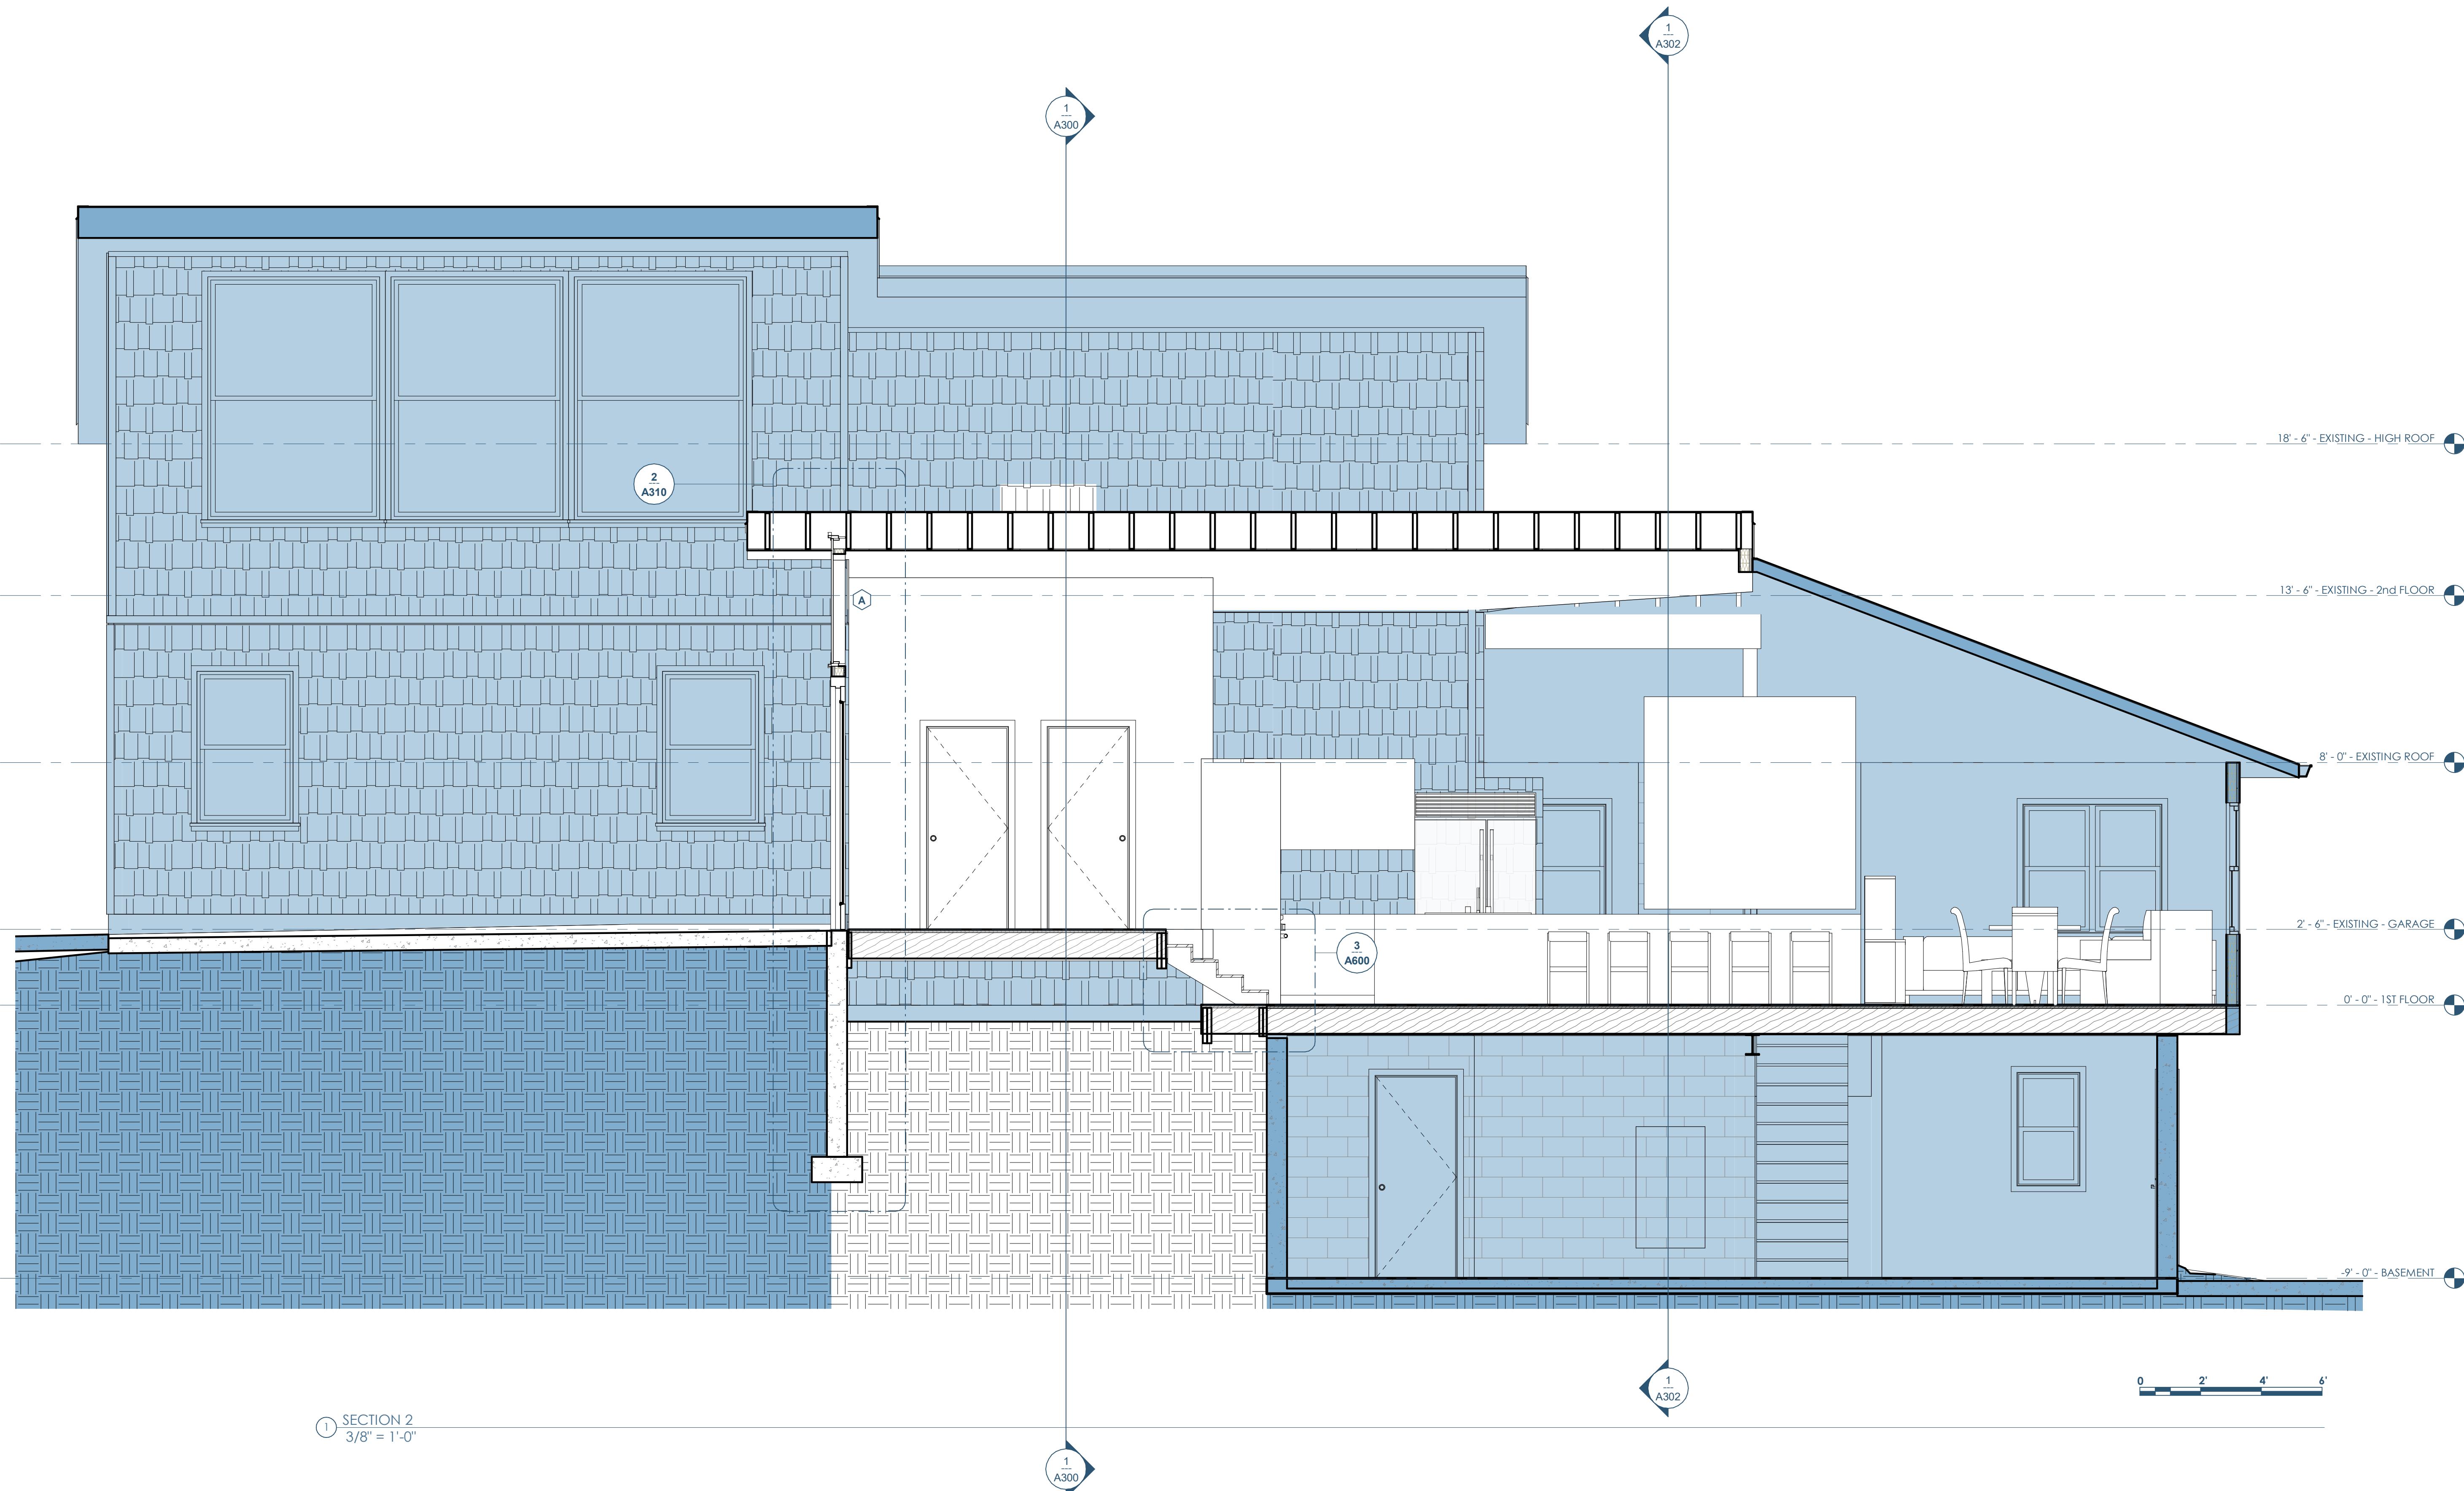

BUILDING SECTION - 08/16/2019
KERN RESIDENCE
N6790 SHOREWOOD HILLS RD - LAKE MILLS, WI 53551
A301



5

4

3

2

1

C


C

B

B

A

A

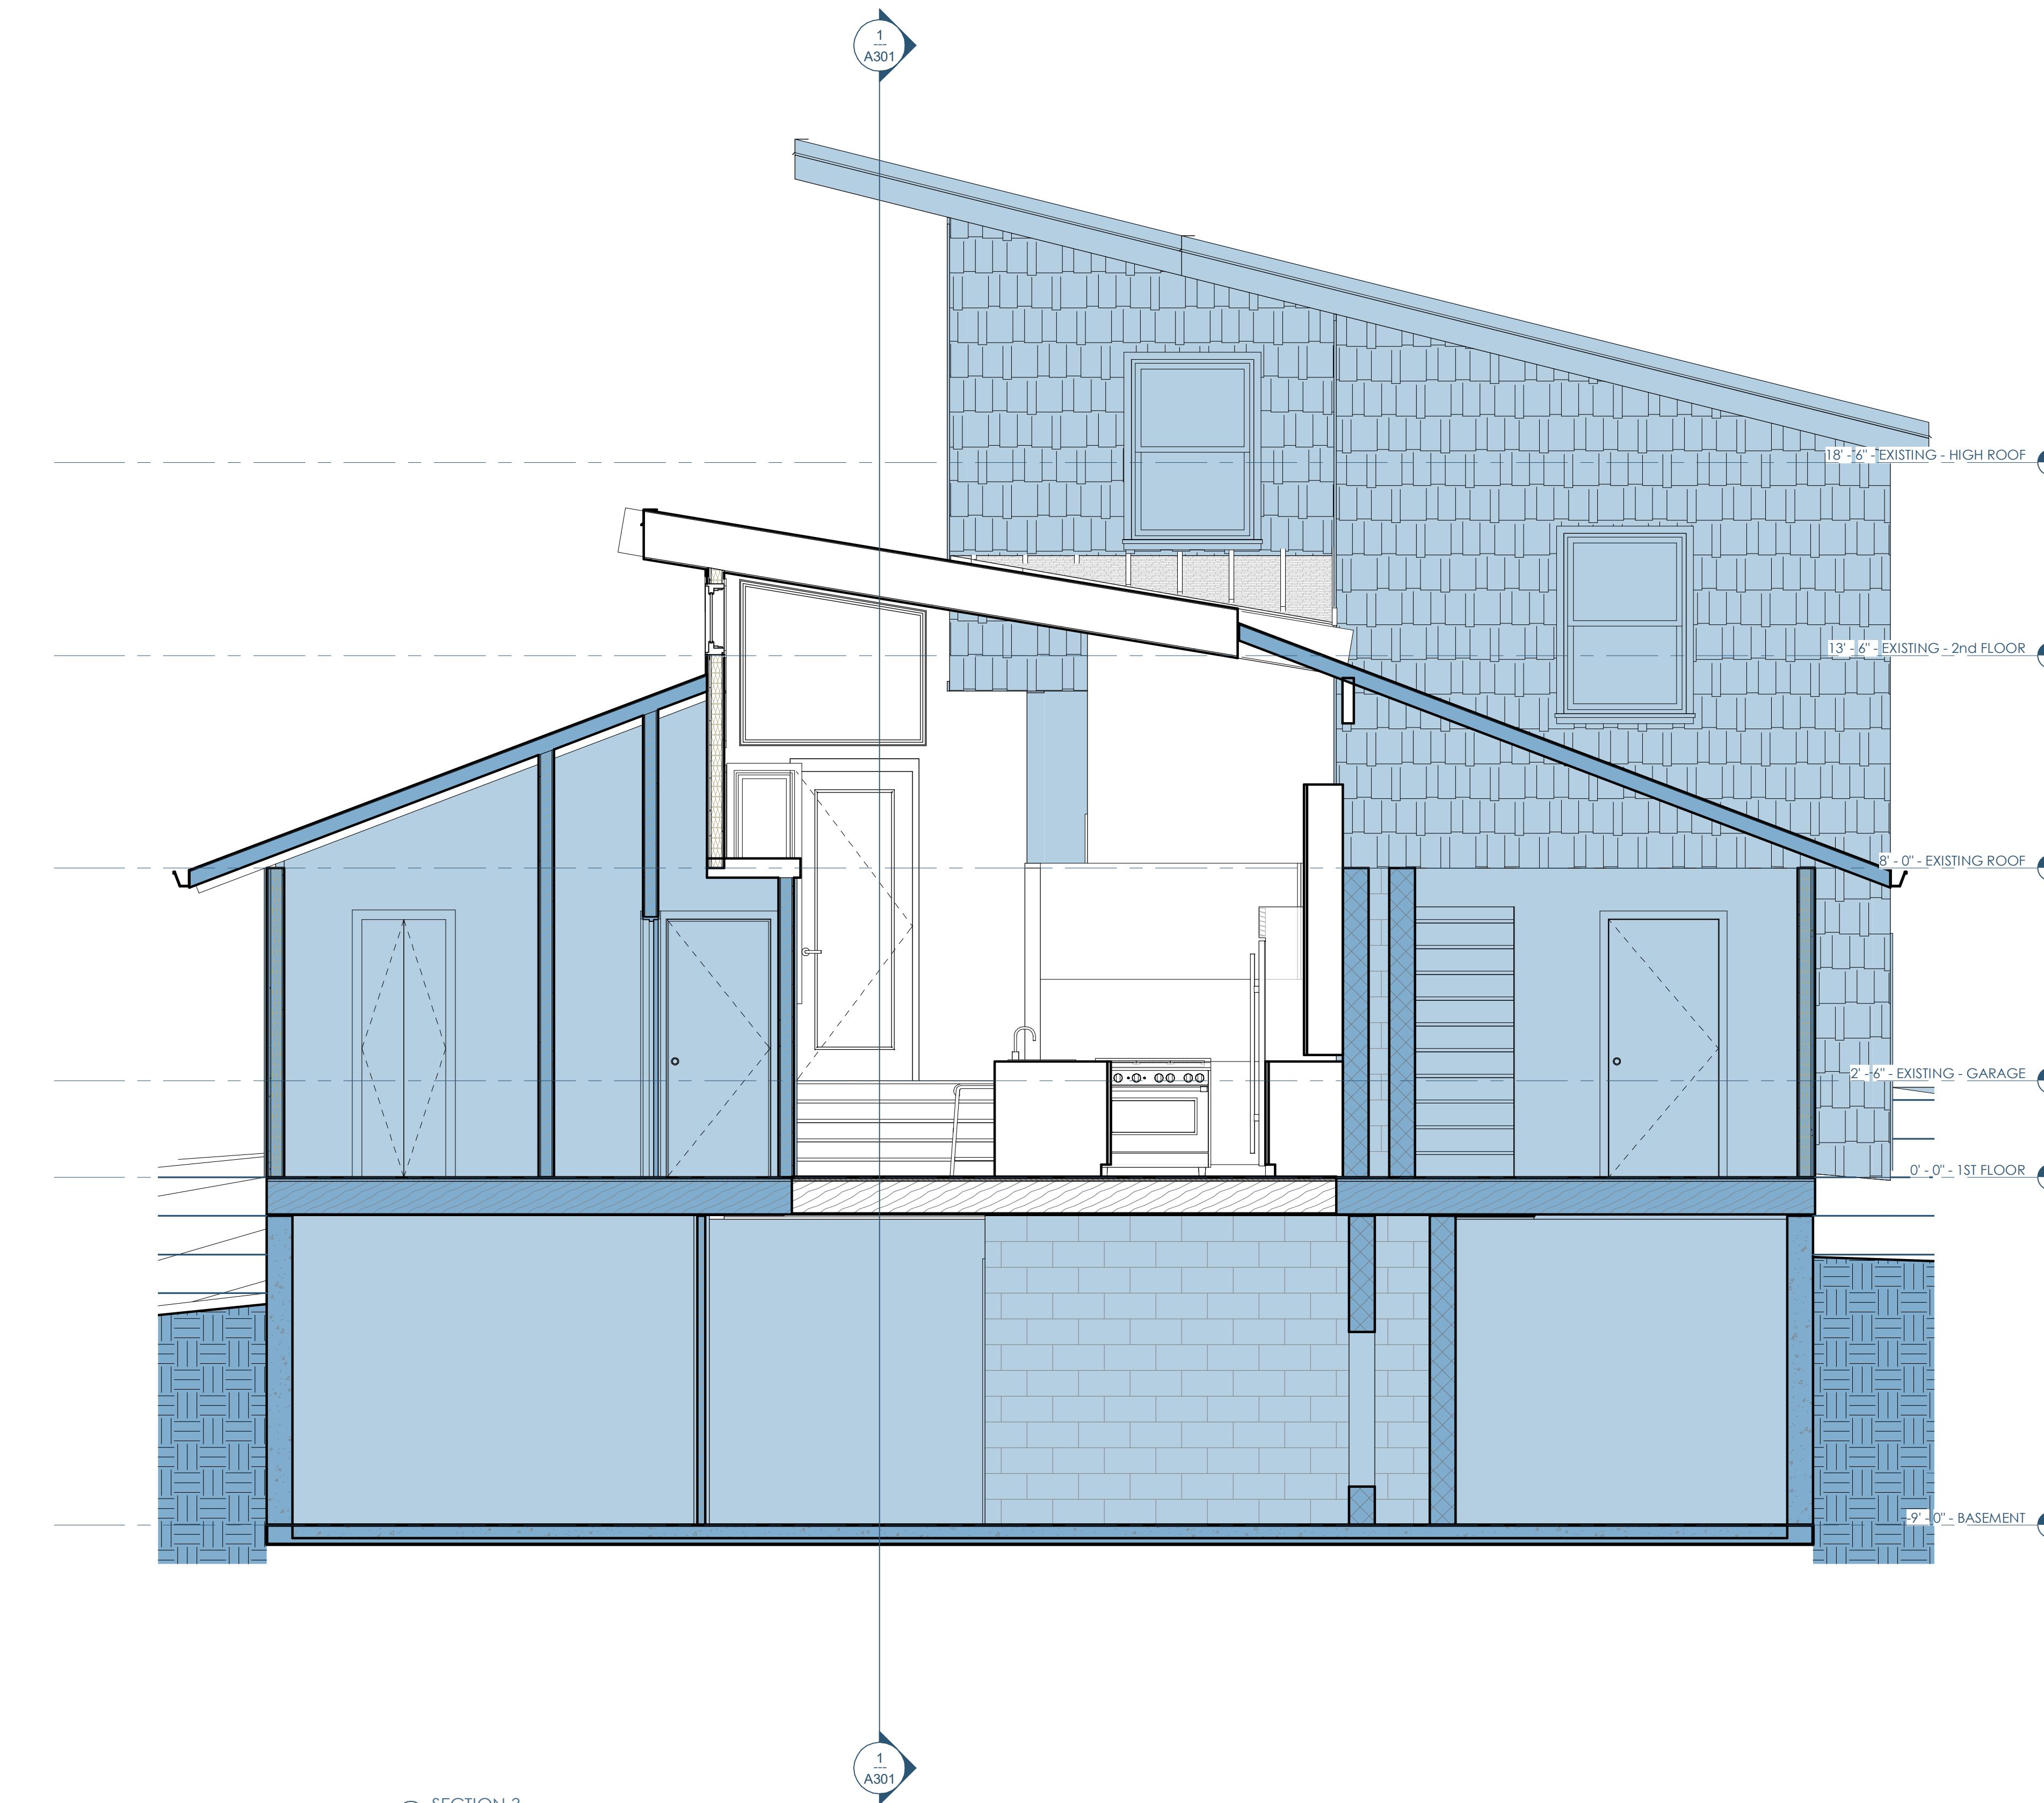

① SECTION 3
3/8" = 1'-0"

0 2' 4' 6'

BUILDING SECTION - 08/16/2019
KERN RESIDENCE
N6790 SHOREWOOD HILLS RD - LAKE MILLS, WI 53551

A302

5

4






3

2

1

C

C

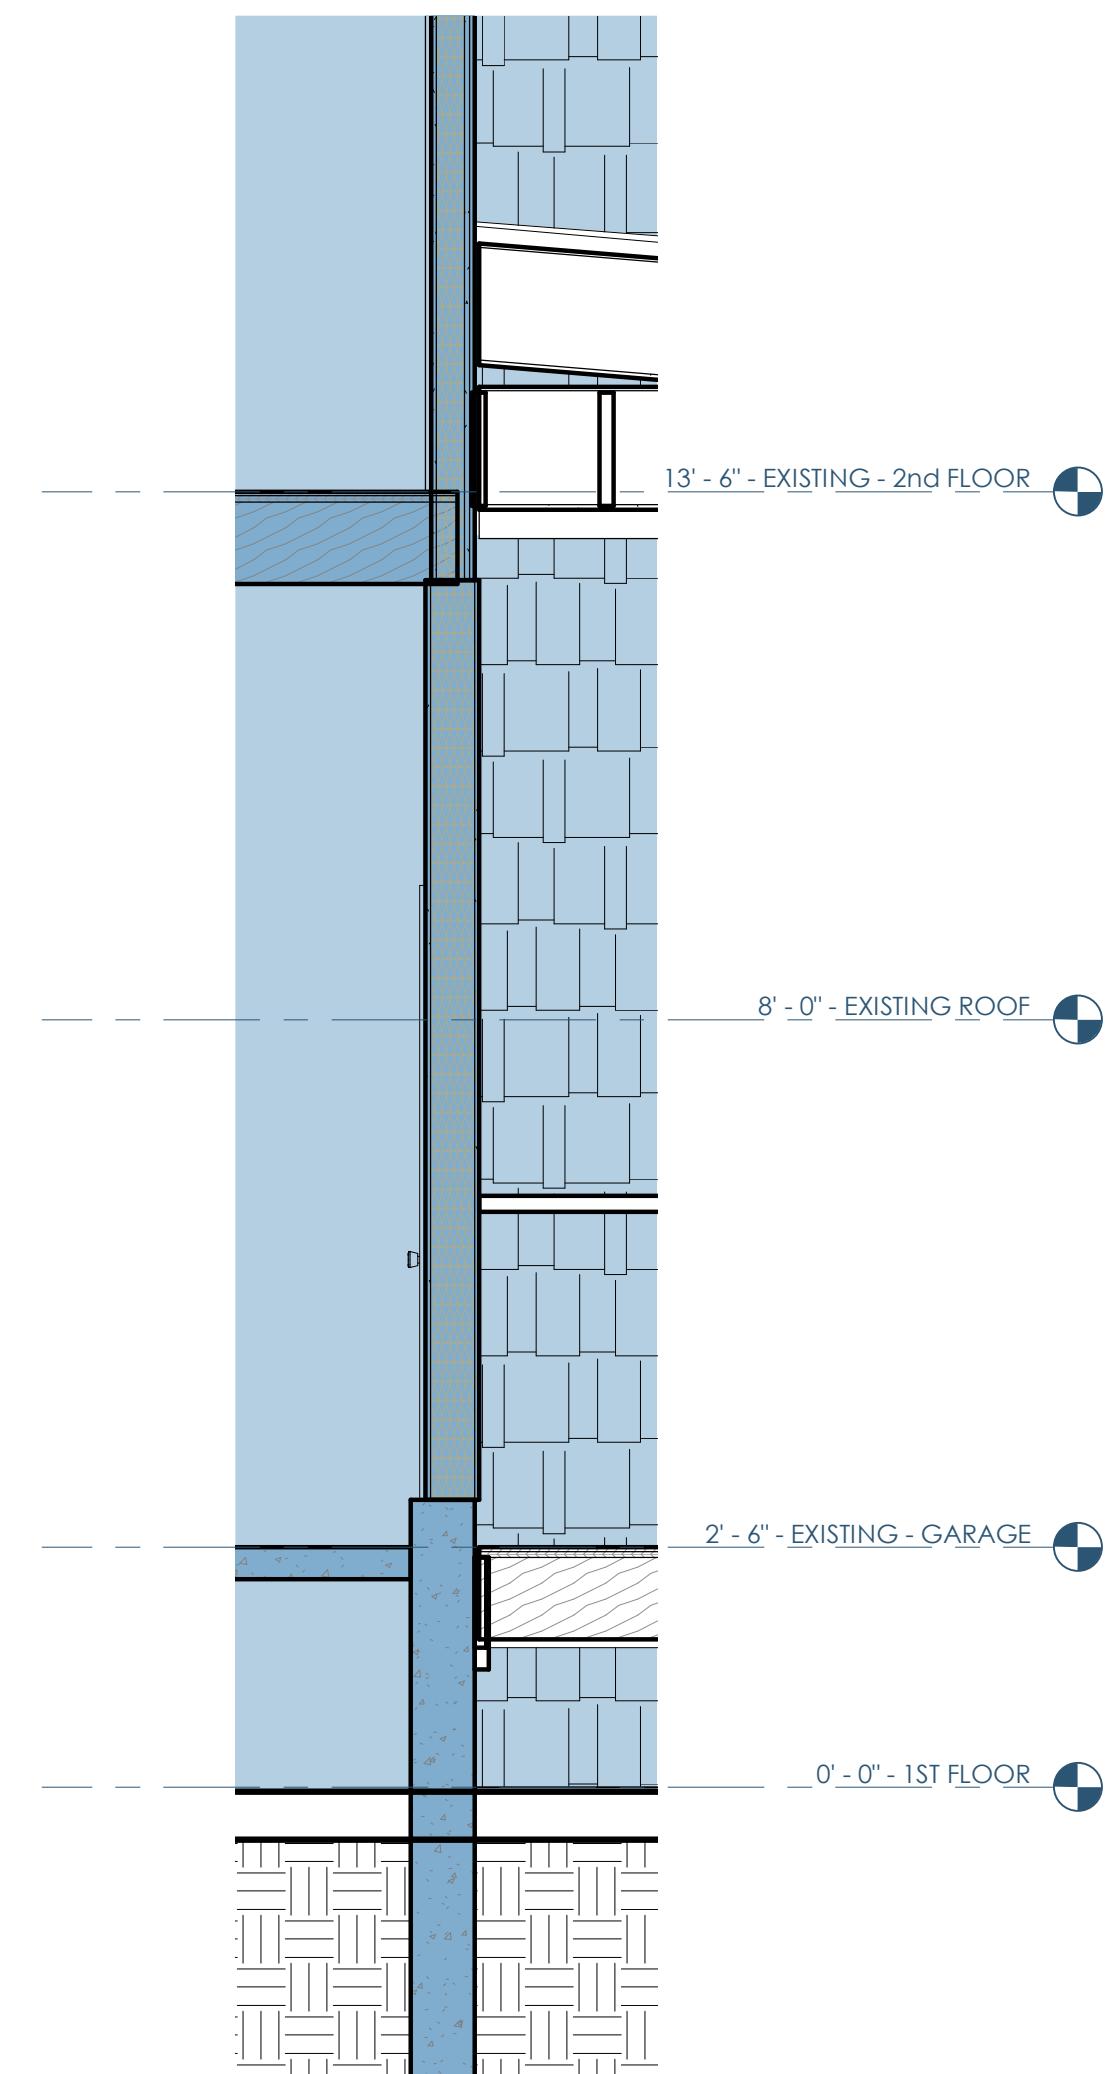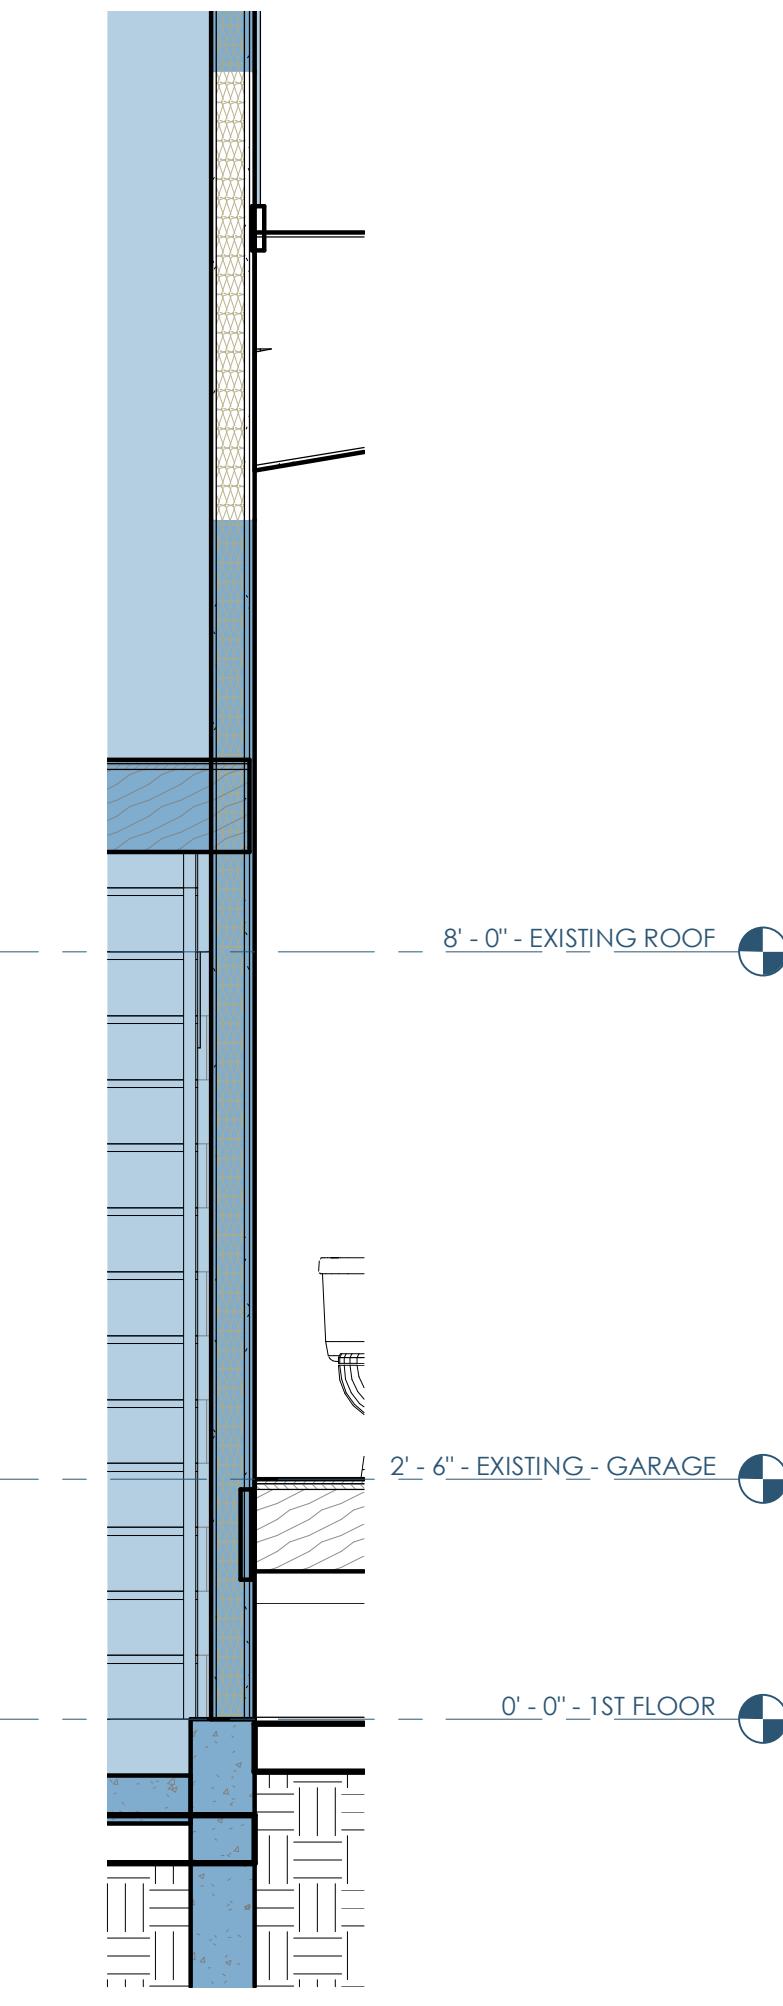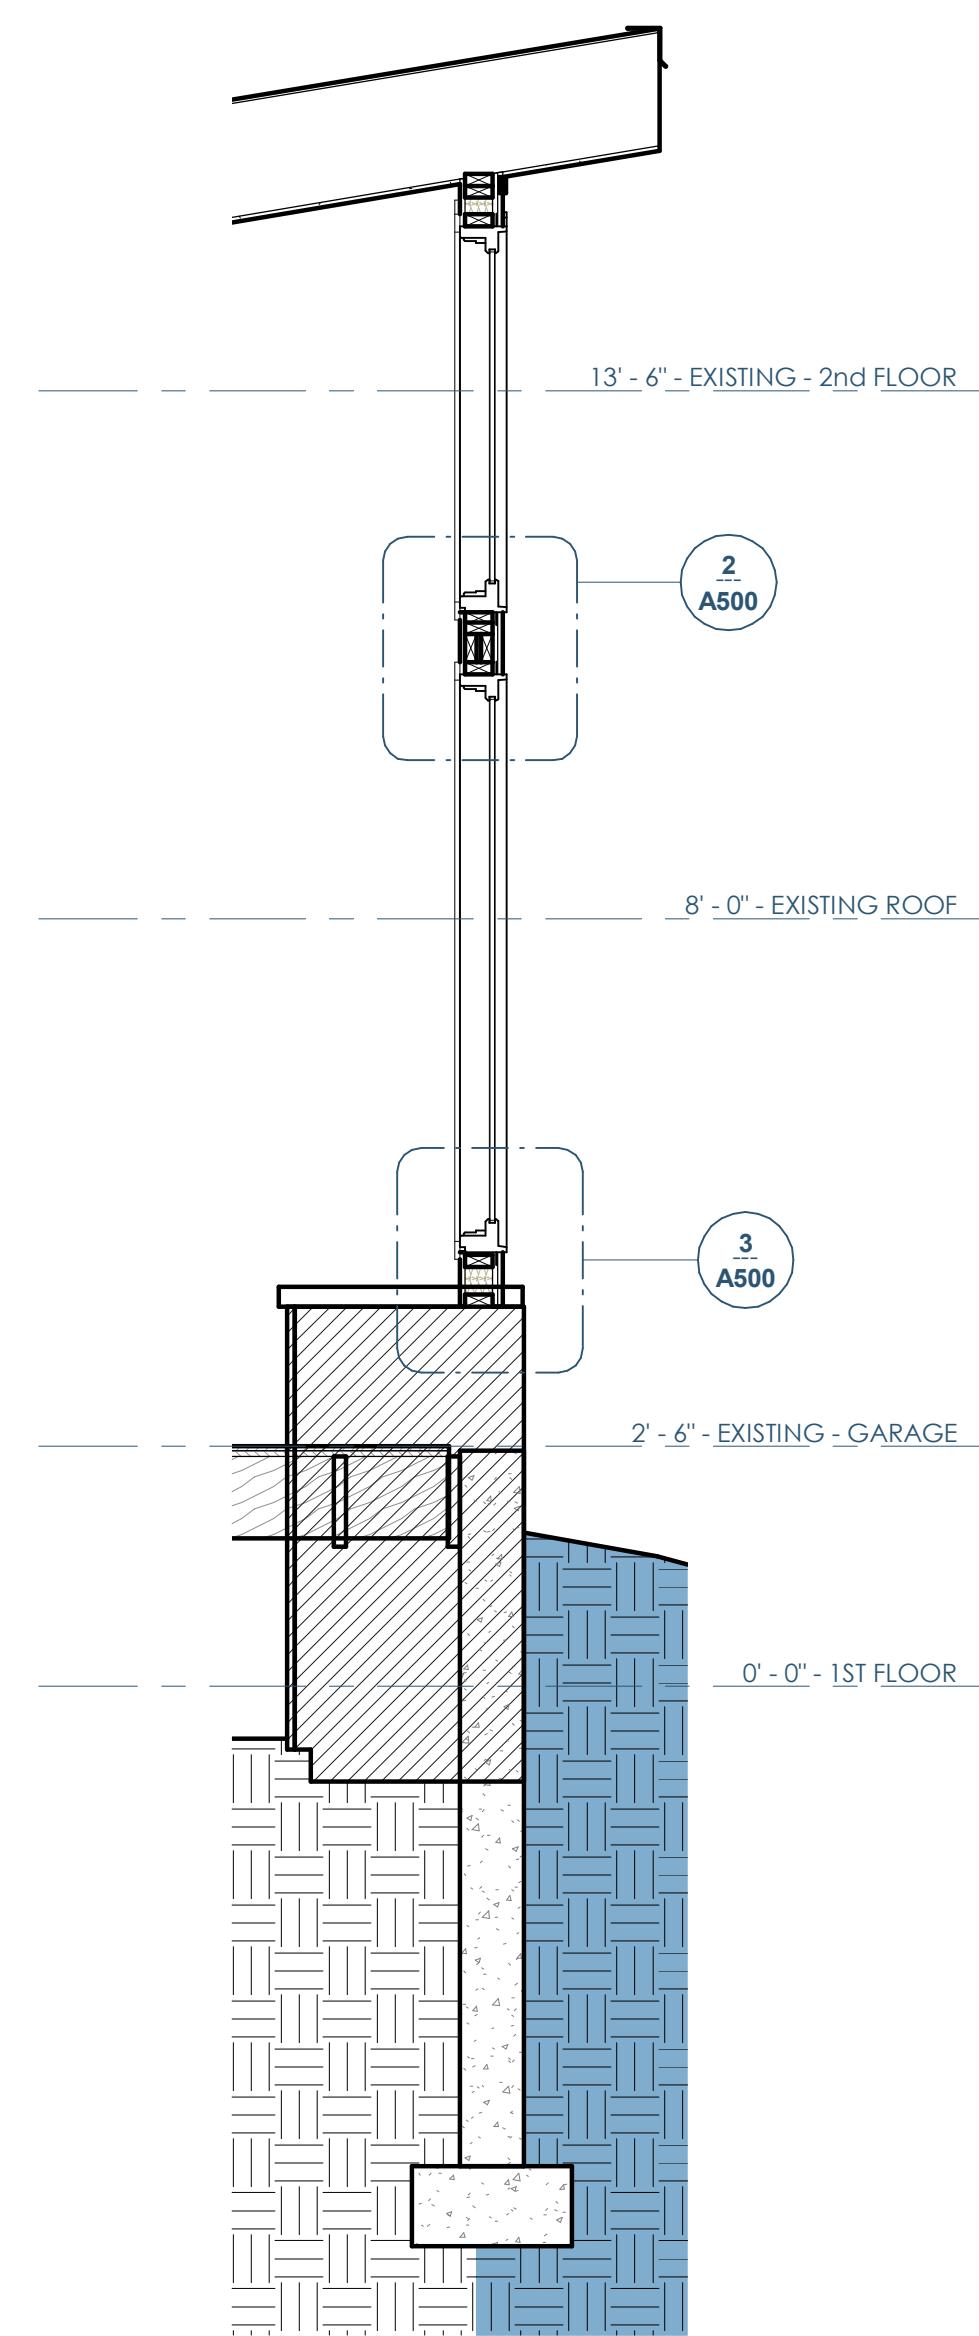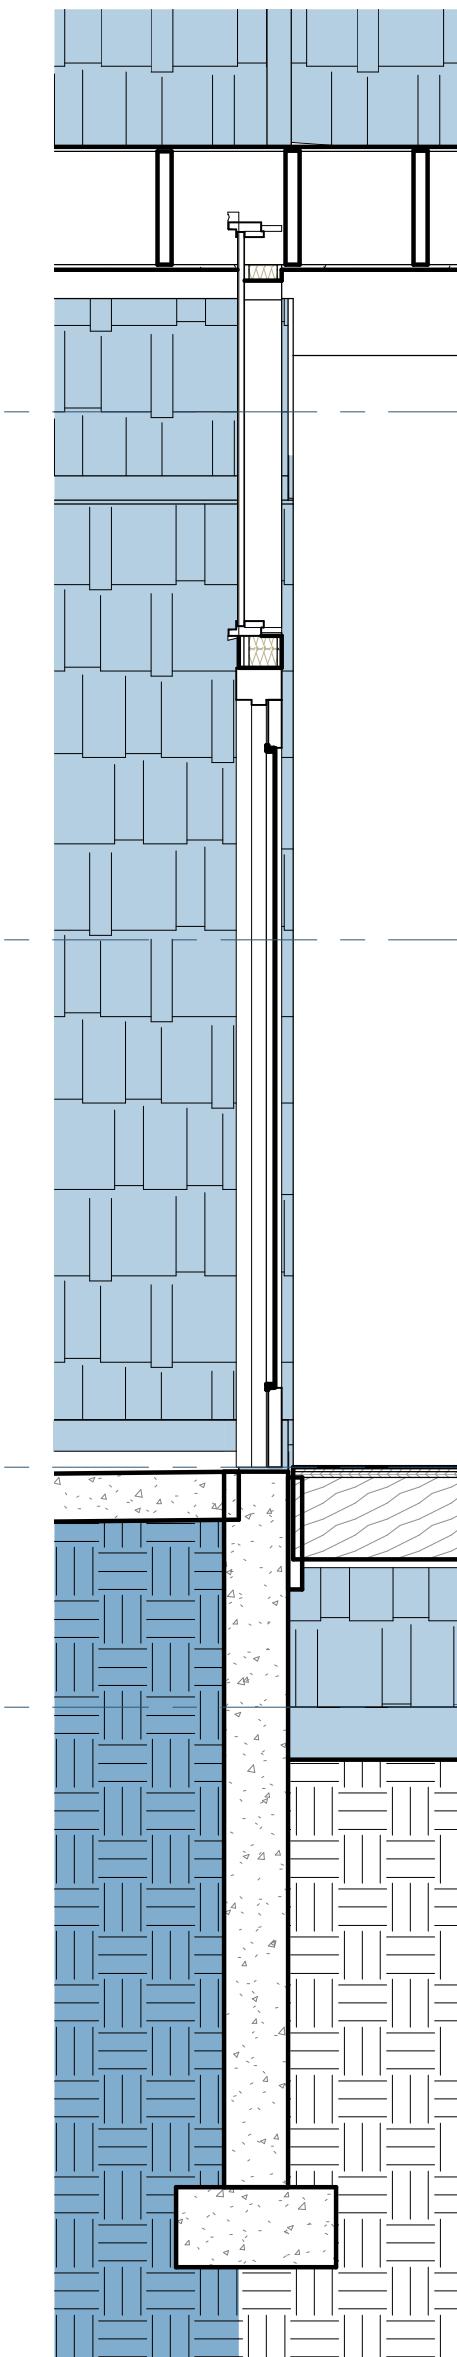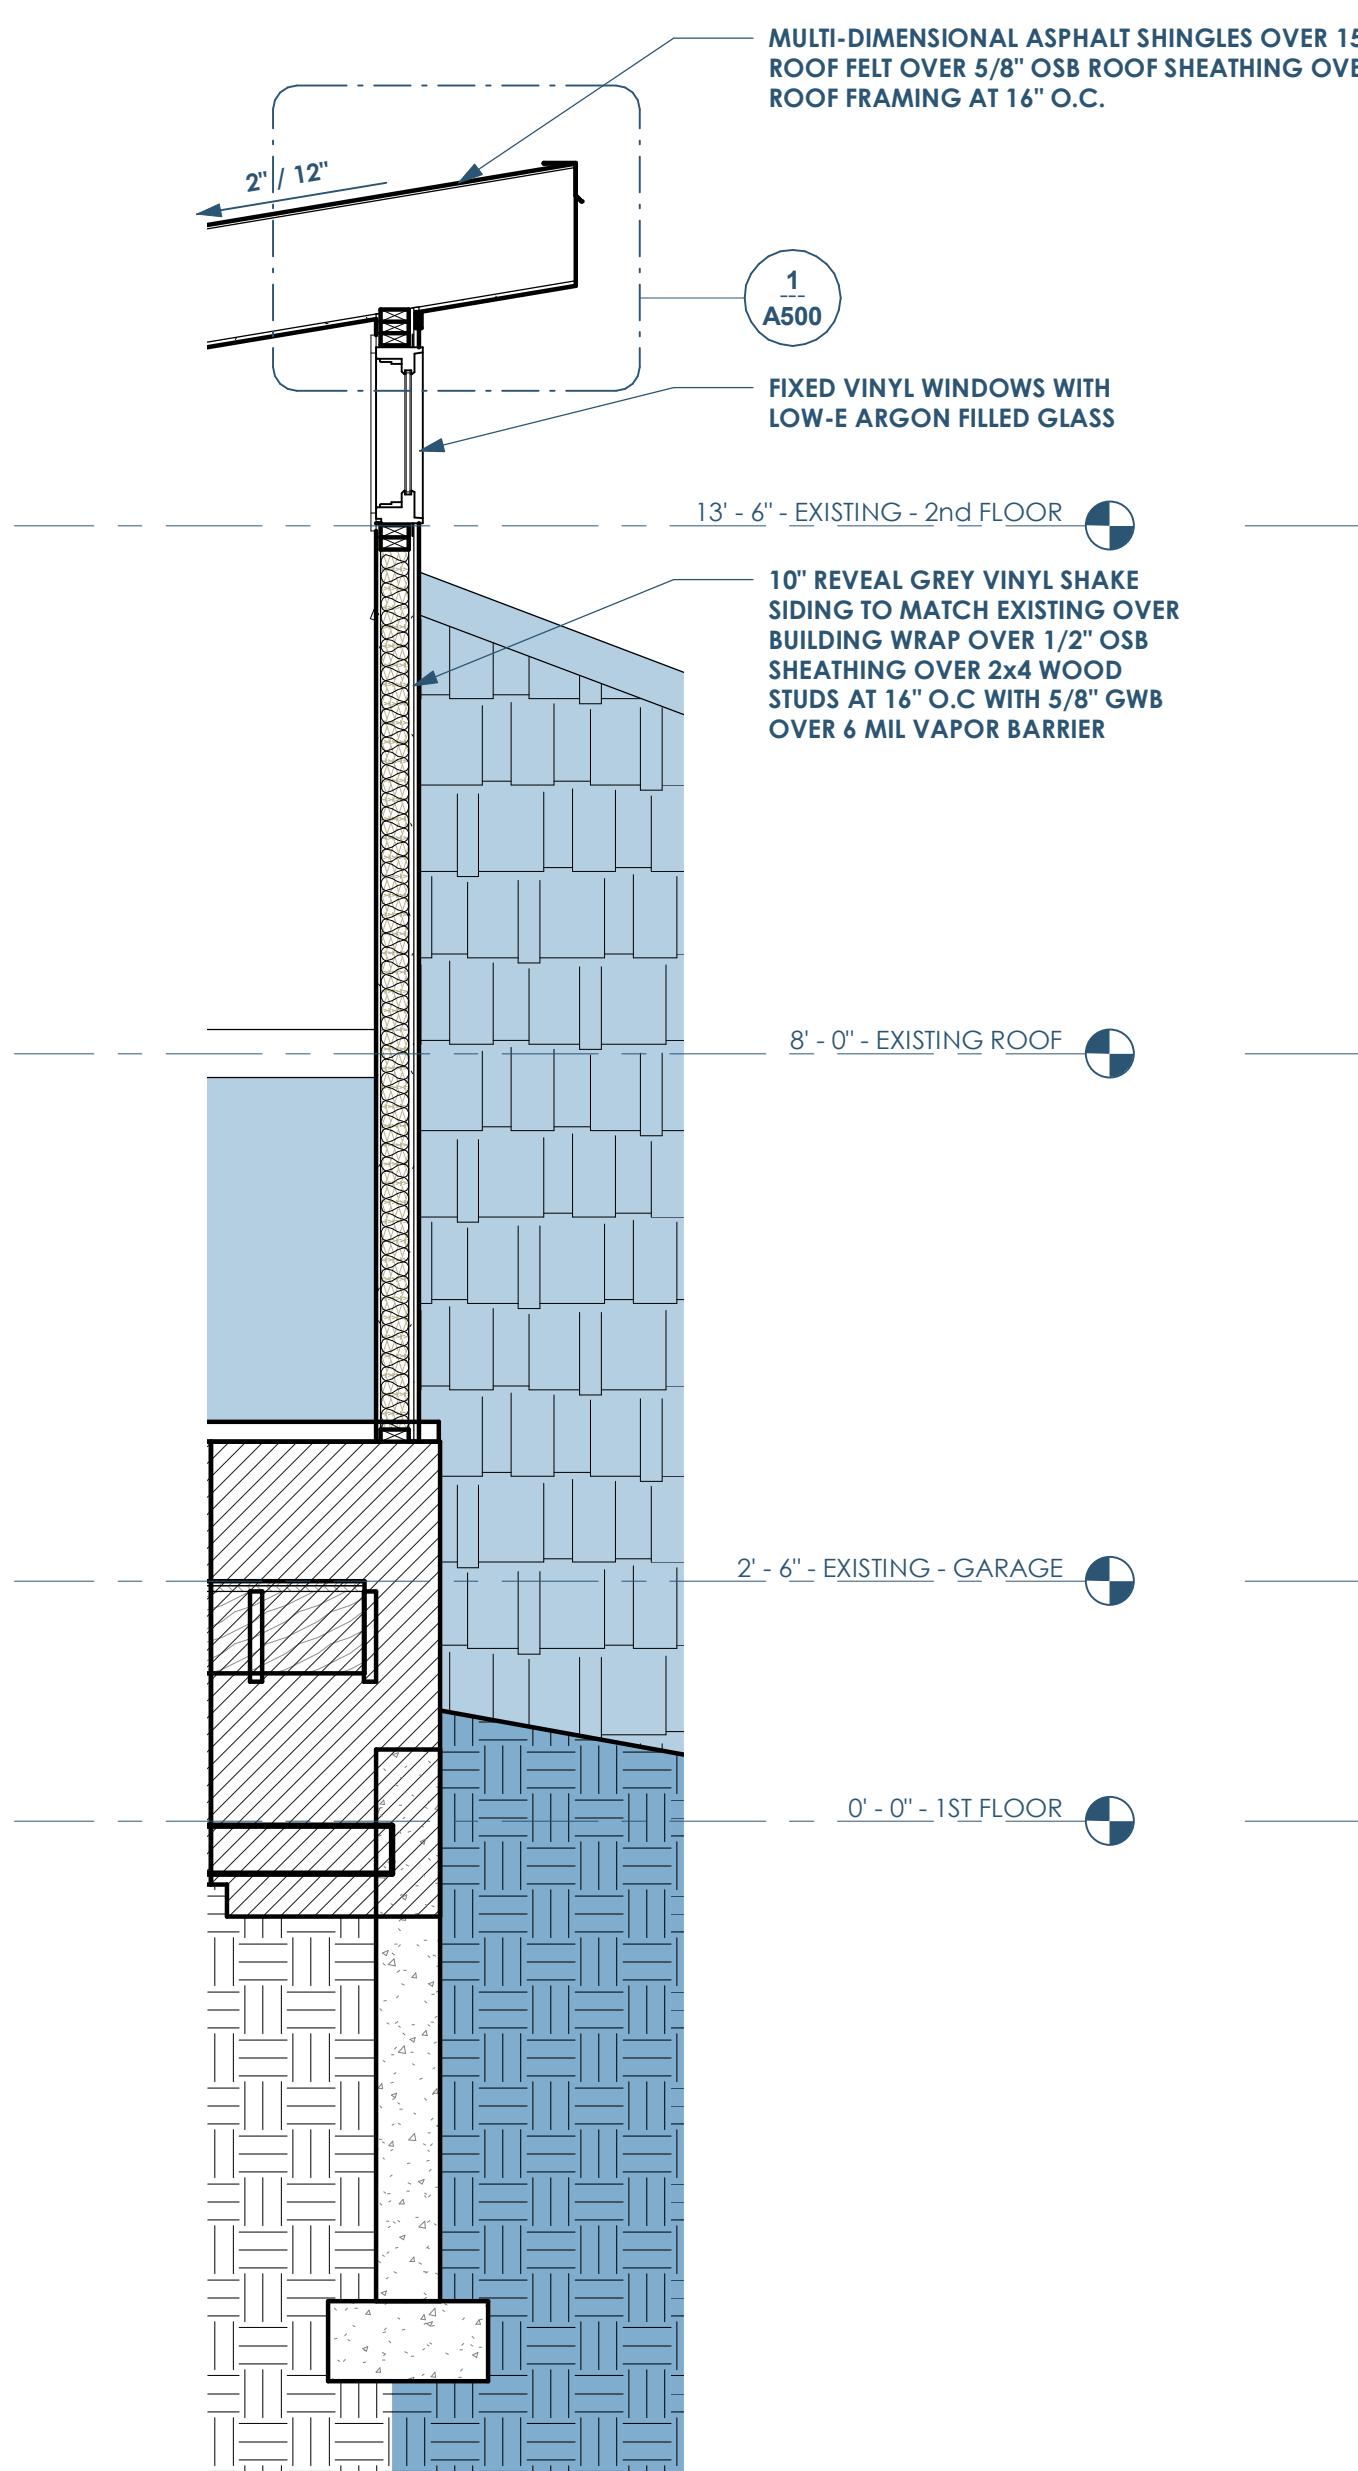

① WALL SECTION A
1/2" = 1'-0"

② WALL SECTION B
1/2" = 1'-0"

③ WALL SECTION C
1/2" = 1'-0"

④ WALL SECTION D
1/2" = 1'-0"

⑤ WALL SECTION E
1/2" = 1'-0"


0 1' 2' 4'




Architect: OpeningDesign
316 W Washington Ave | Suite 675
Madison, WI 53703
ryan@openingdesign.com | 773.425.6456

WALL SECTIONS - 08/16/2019
KERN RESIDENCE
N6790 SHOREWOOD HILLS RD - LAKE MILLS, WI 53551


A310

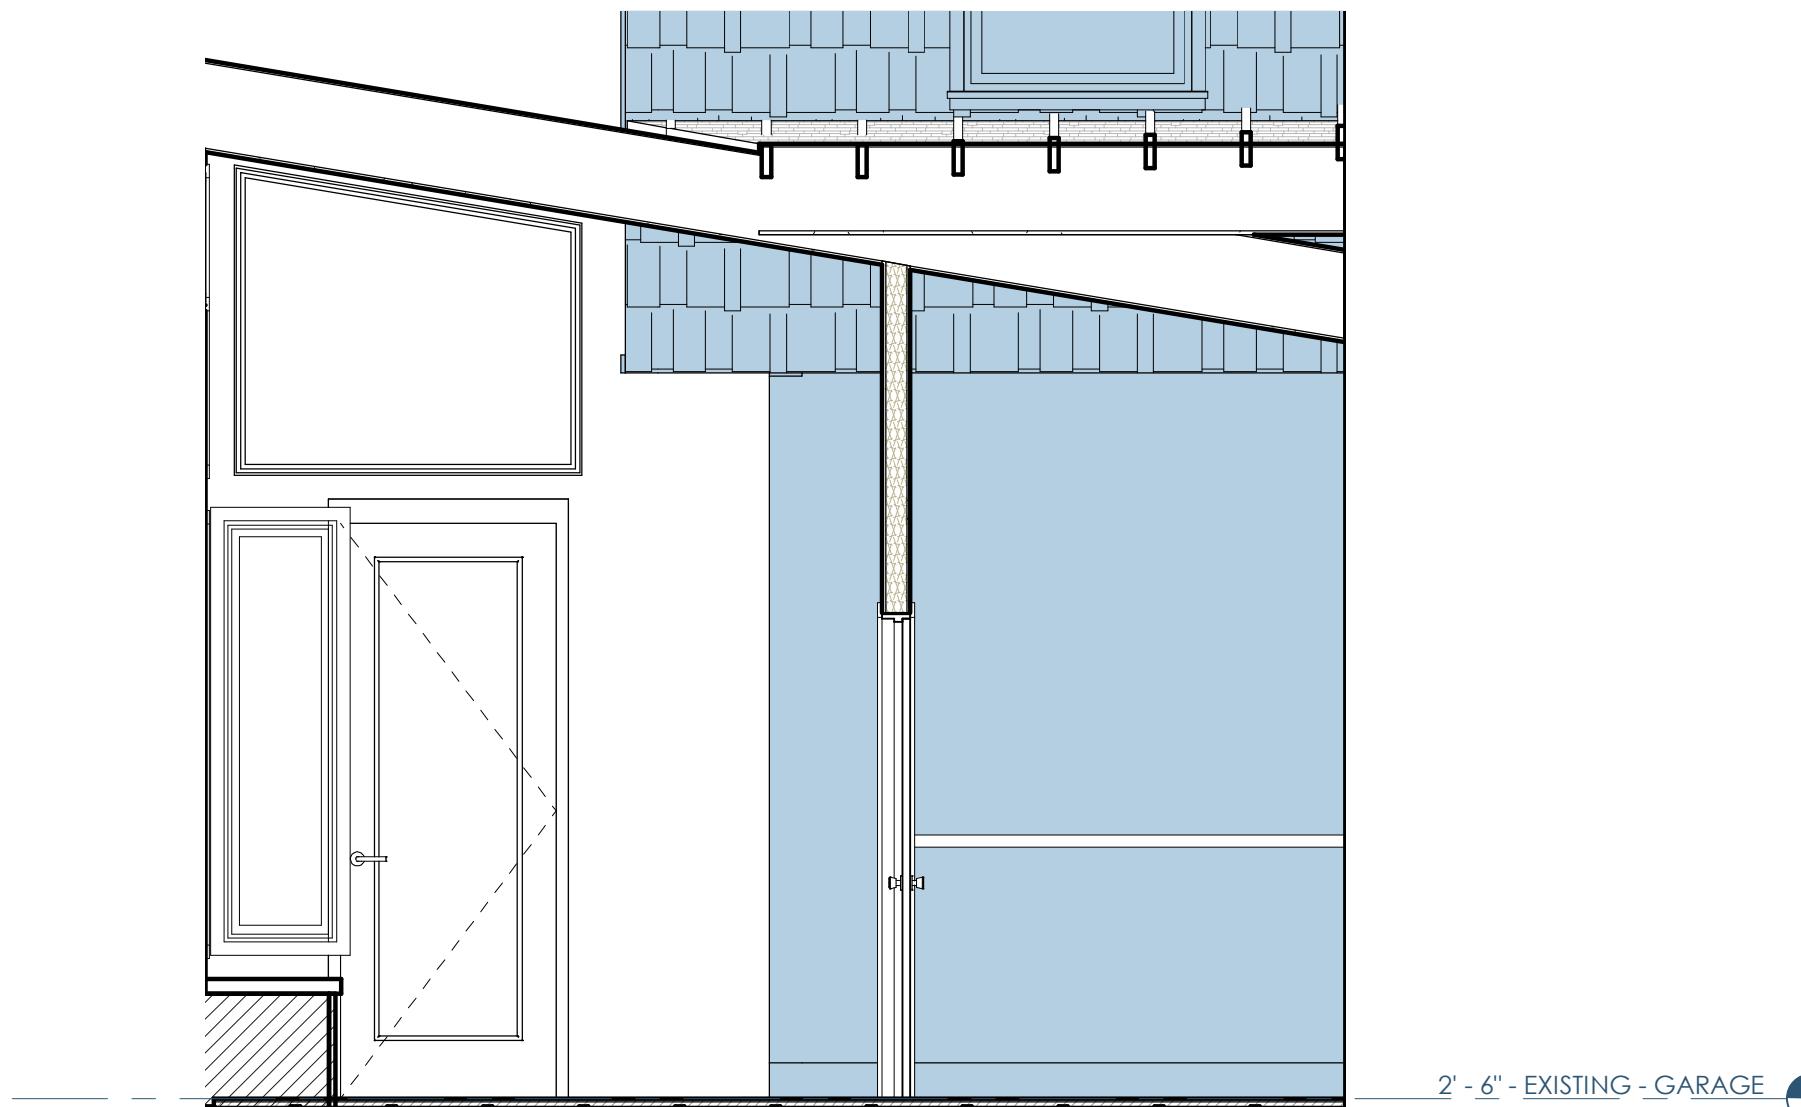

① FOYER - WEST WALL
3/8" = 1'-0"

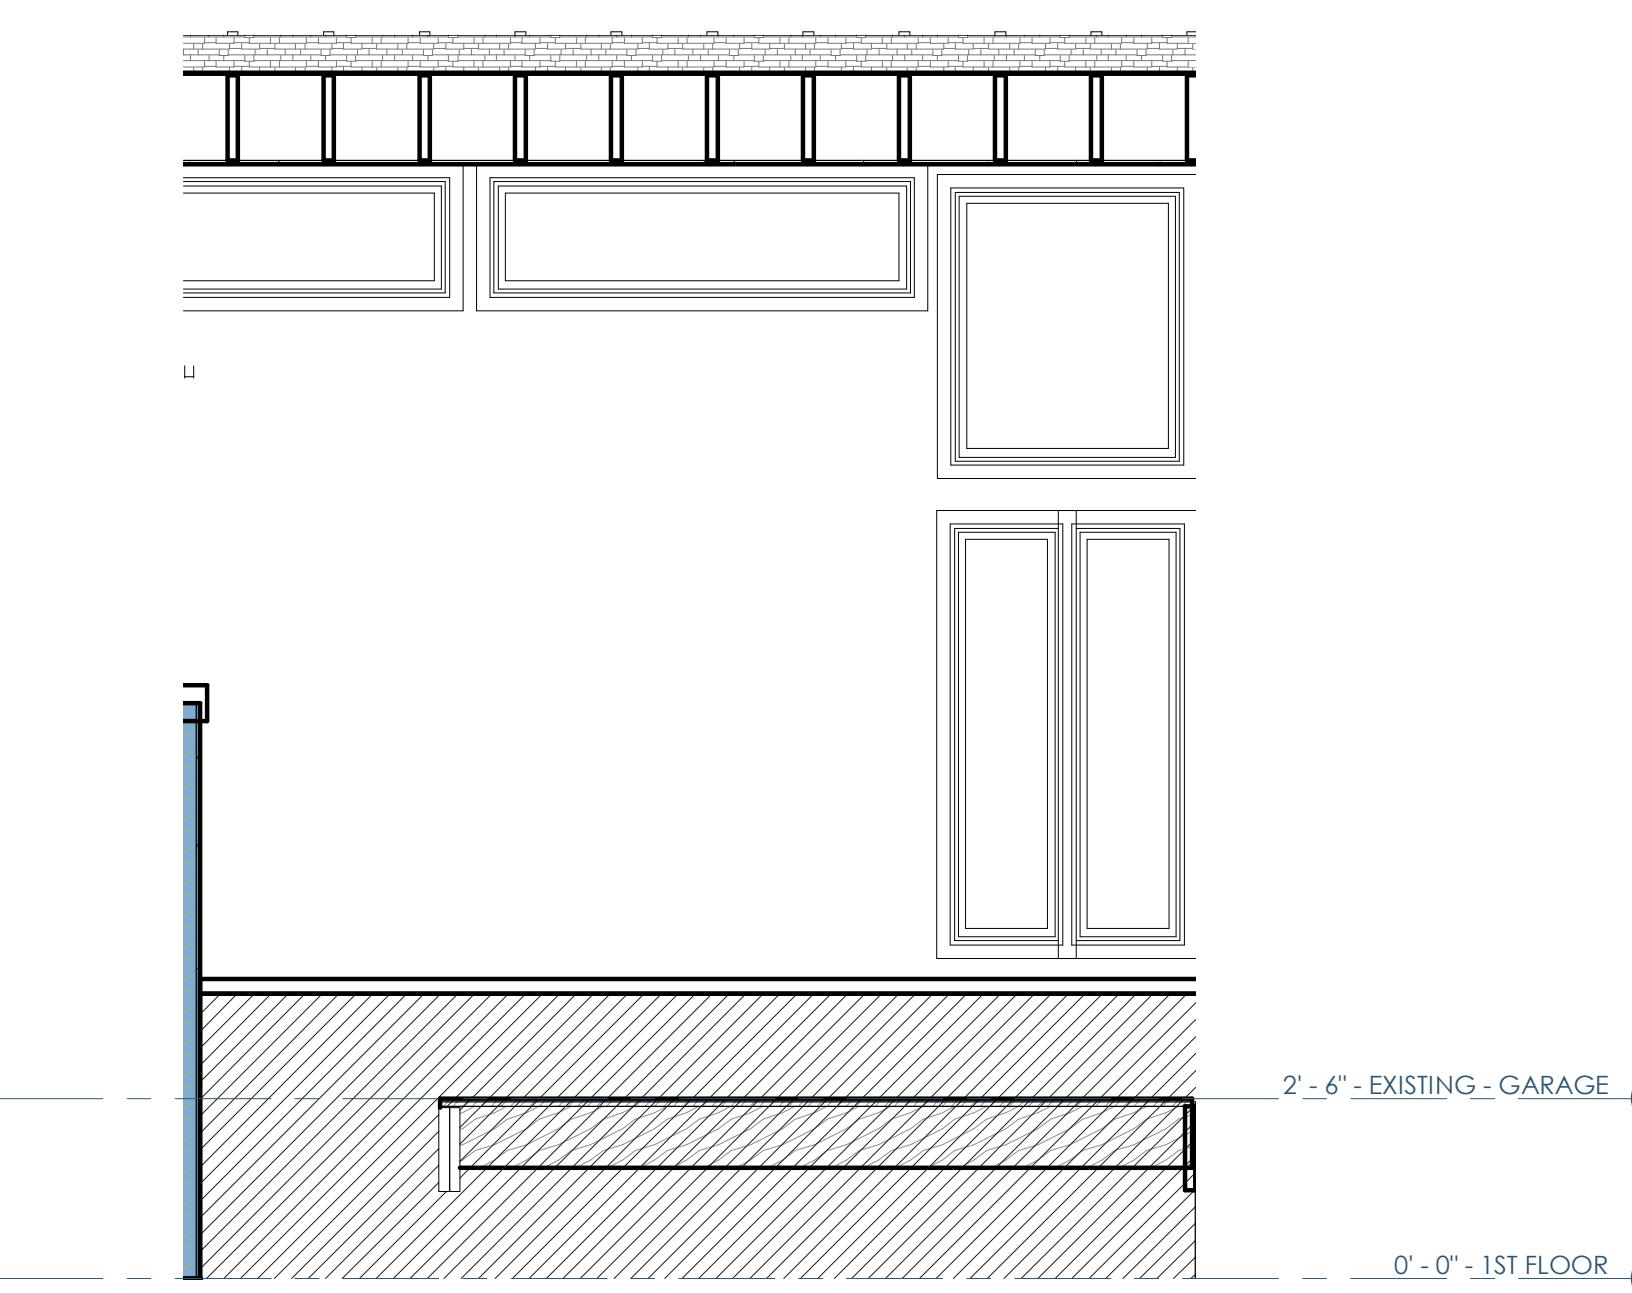

② FOYER - SOUTH WALL
3/8" = 1'-0"

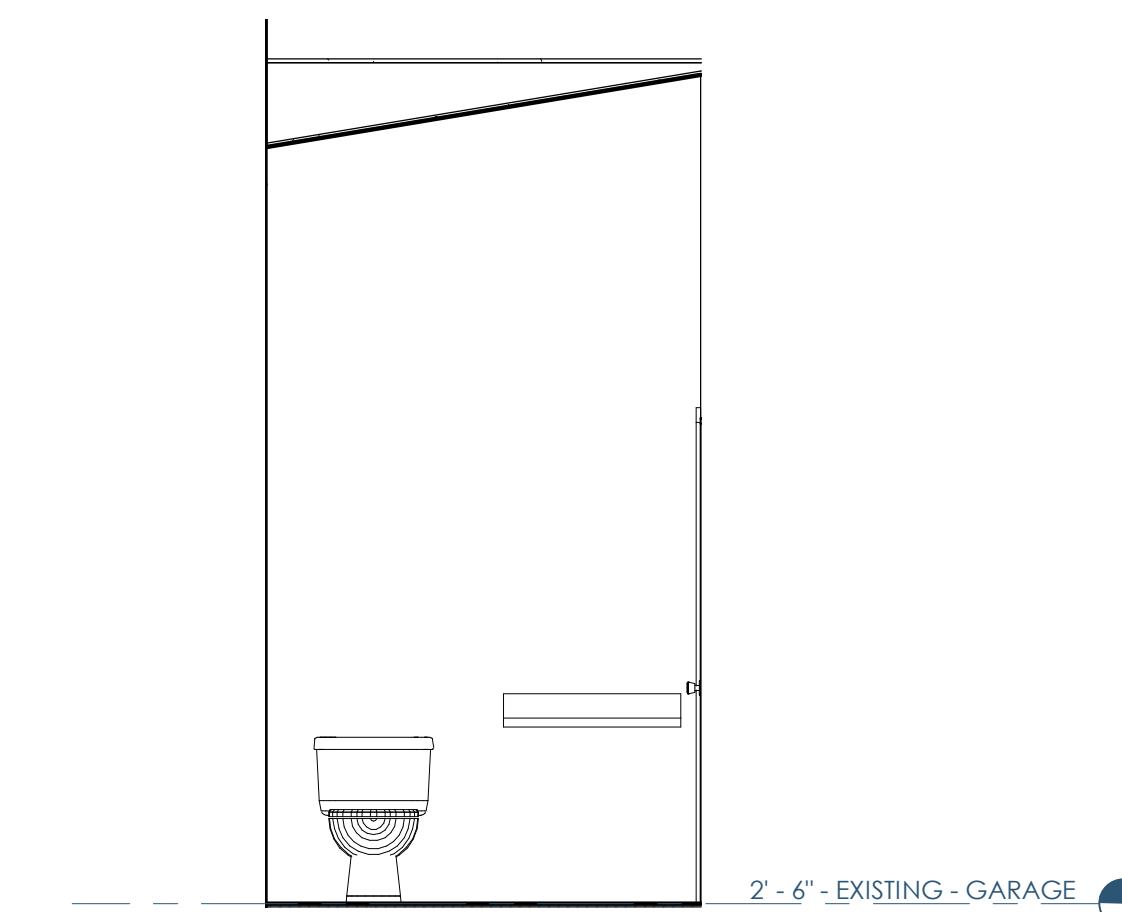


③ POWDER ROOM - EAST WALL
3/8" = 1'-0"


0 2' 4' 6'



5 4 3 2 1

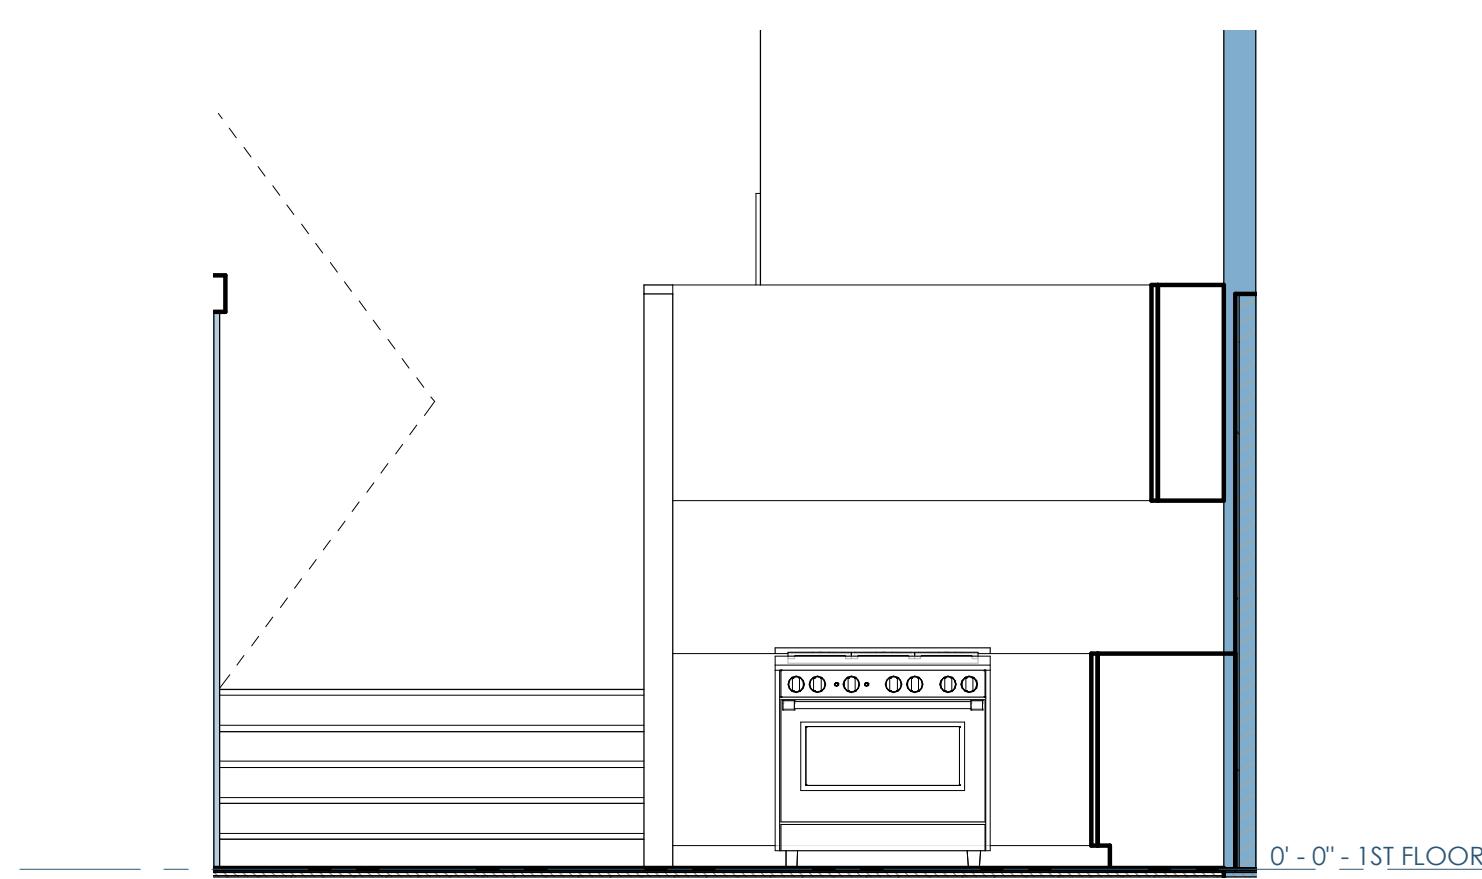


① KITCHEN - WEST WALL
3/8" = 1'-0"

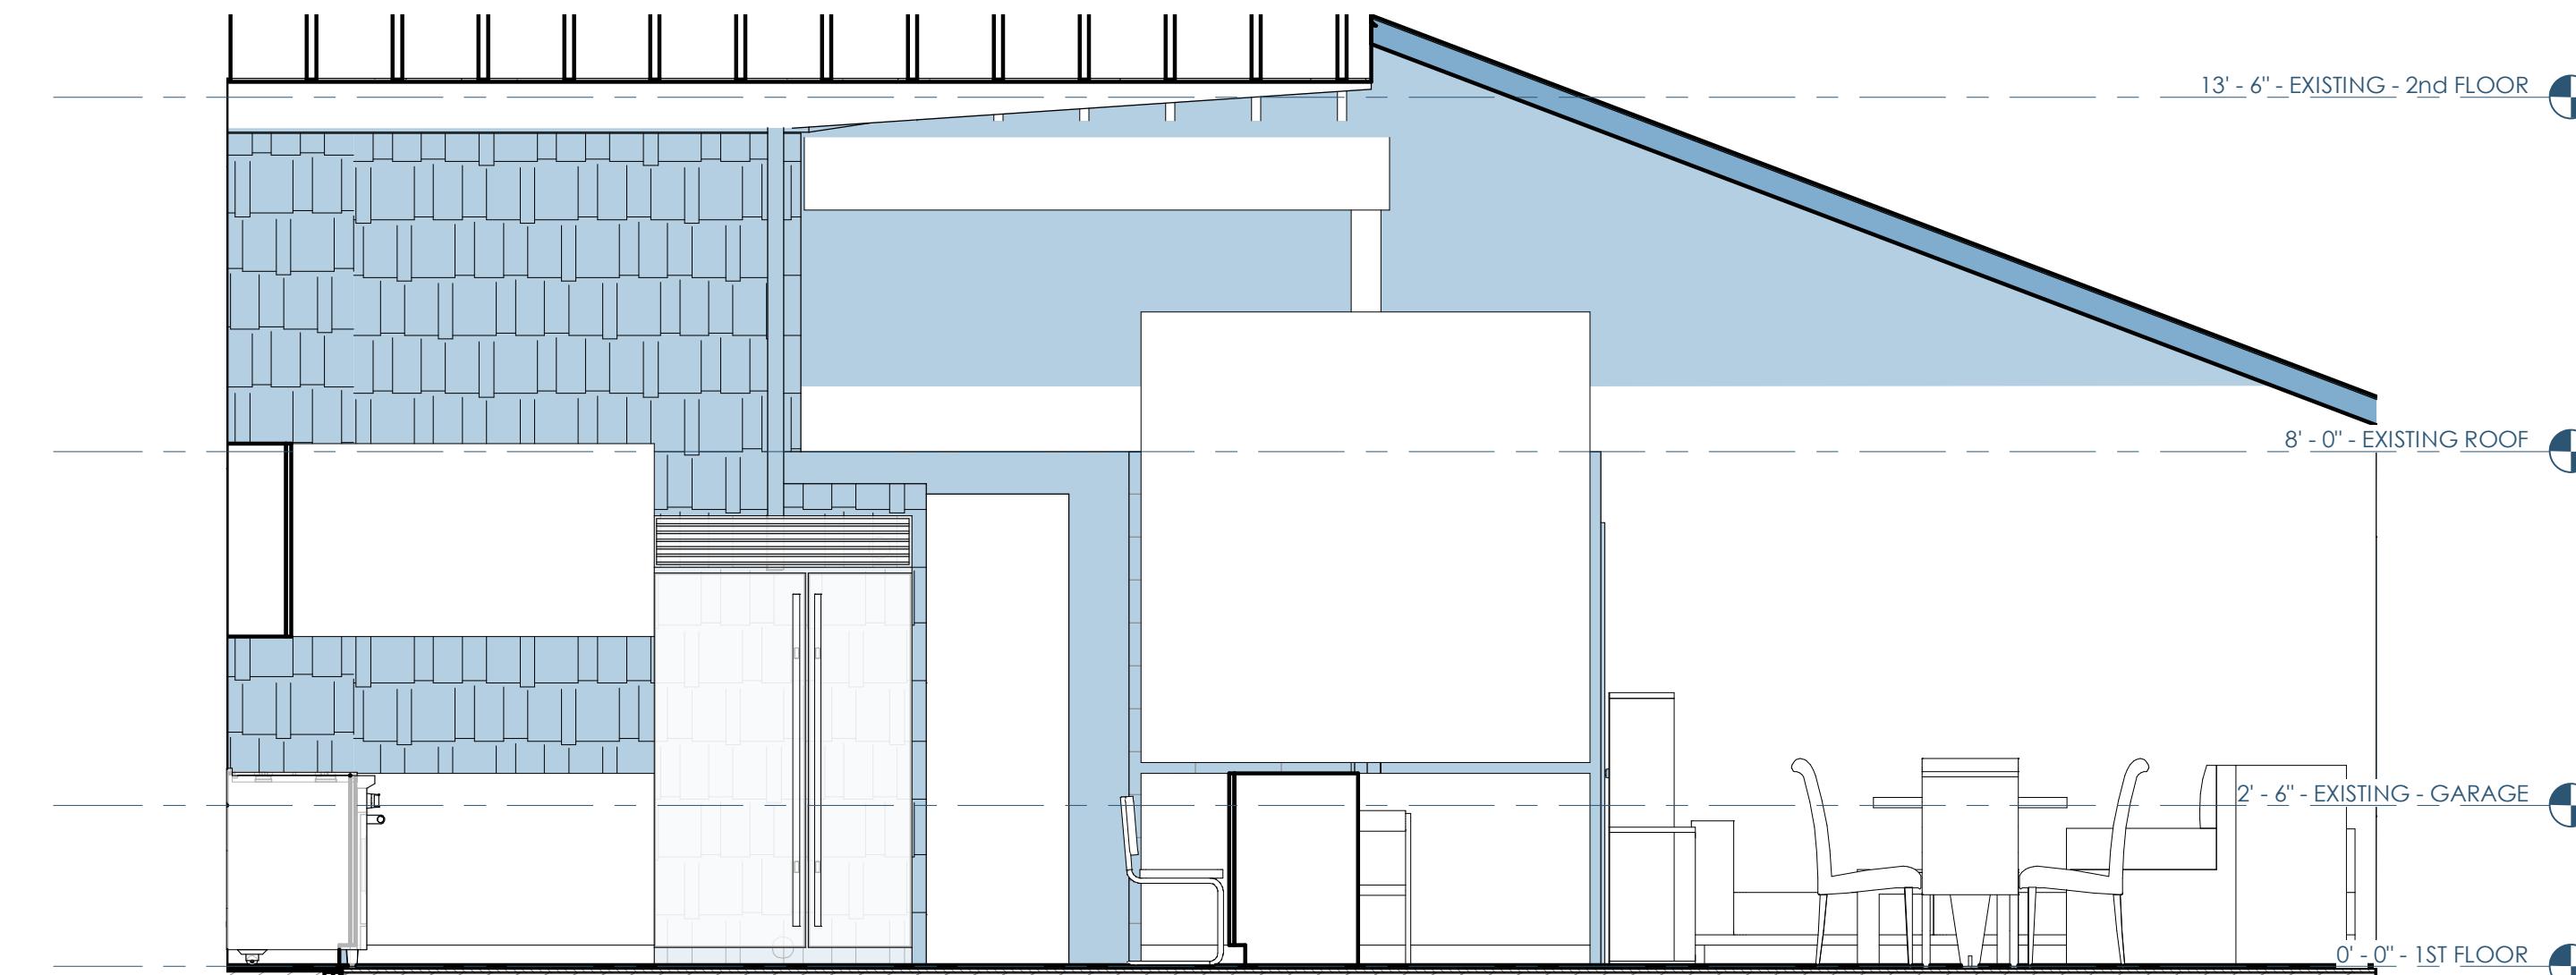


② KITCHEN - NORTH WALL
3/8" = 1'-0"

0 2' 4' 6'

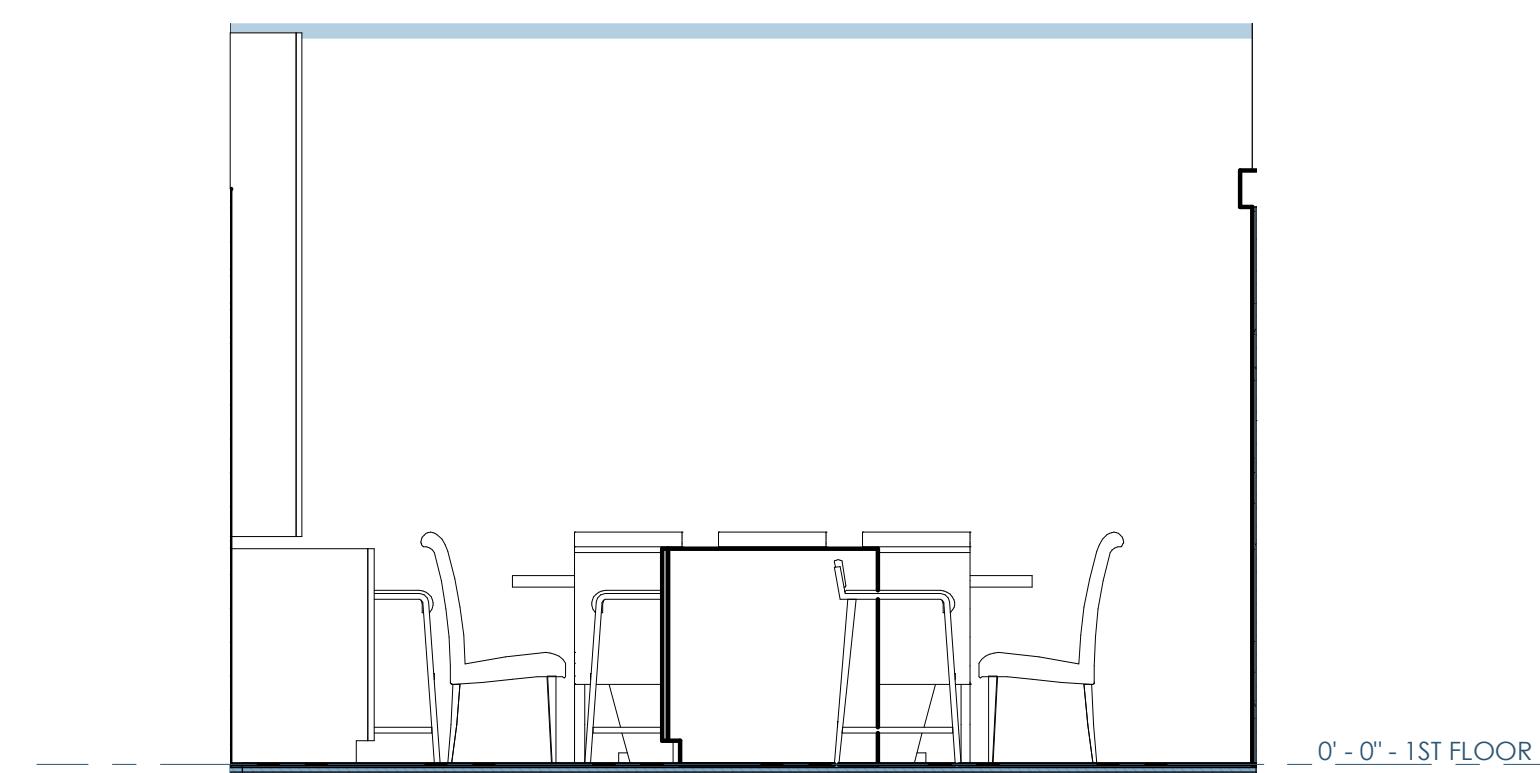

③ KITCHEN - EAST WALL
3/8" = 1'-0"

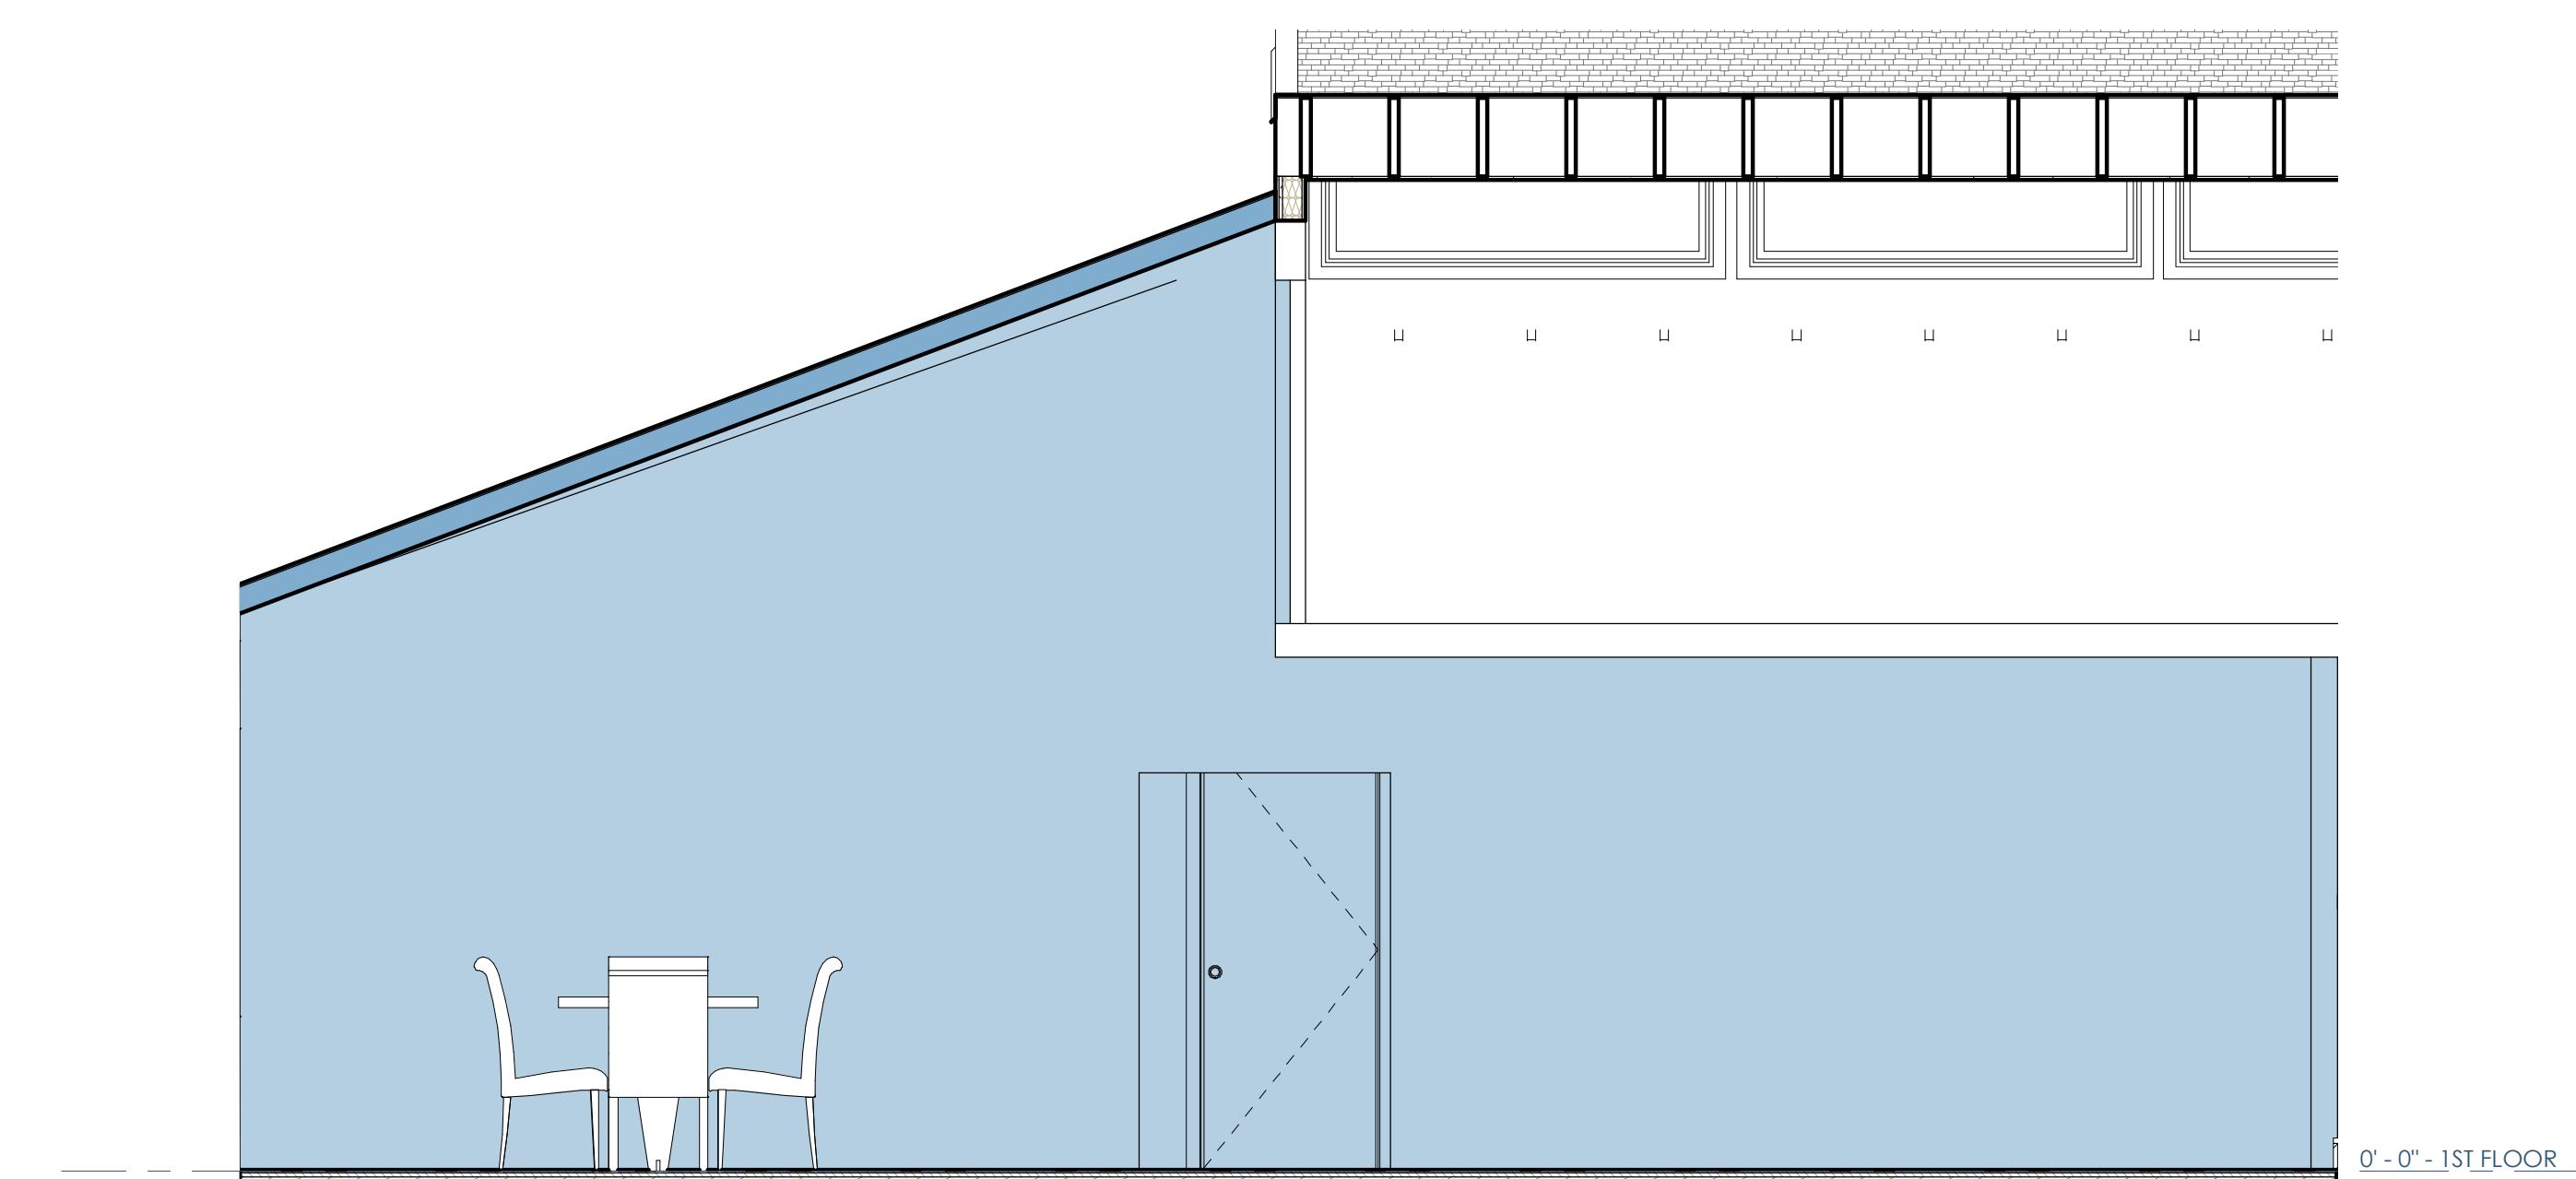

④ KITCHEN - SOUTH WALL
3/8" = 1'-0"

0 2' 4' 6'

5

4

3

2

1

C


C

B


B

A

A

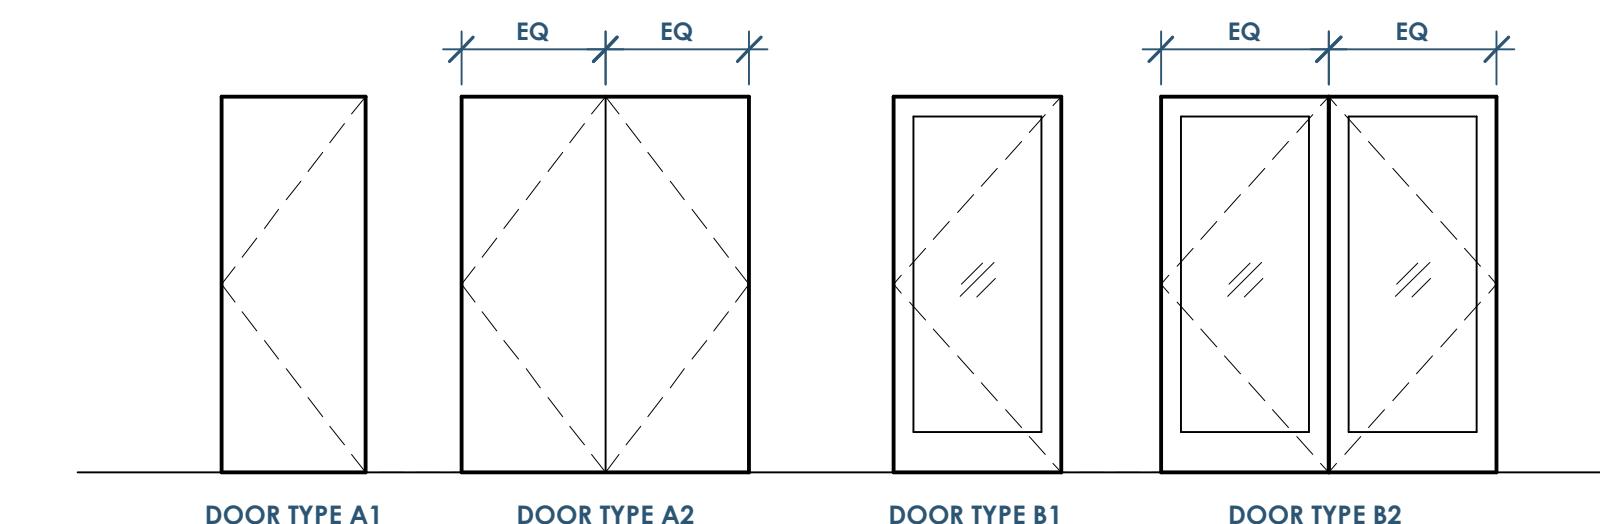


① DOOR TYPES
1/4" = 1'-0"

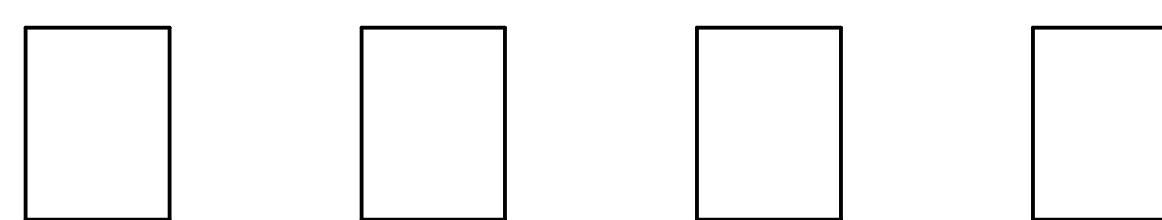

WINDOW TYPE A WINDOW TYPE B WINDOW TYPE C WINDOW TYPE D

② WINDOW TYPES
1/4" = 1'-0"

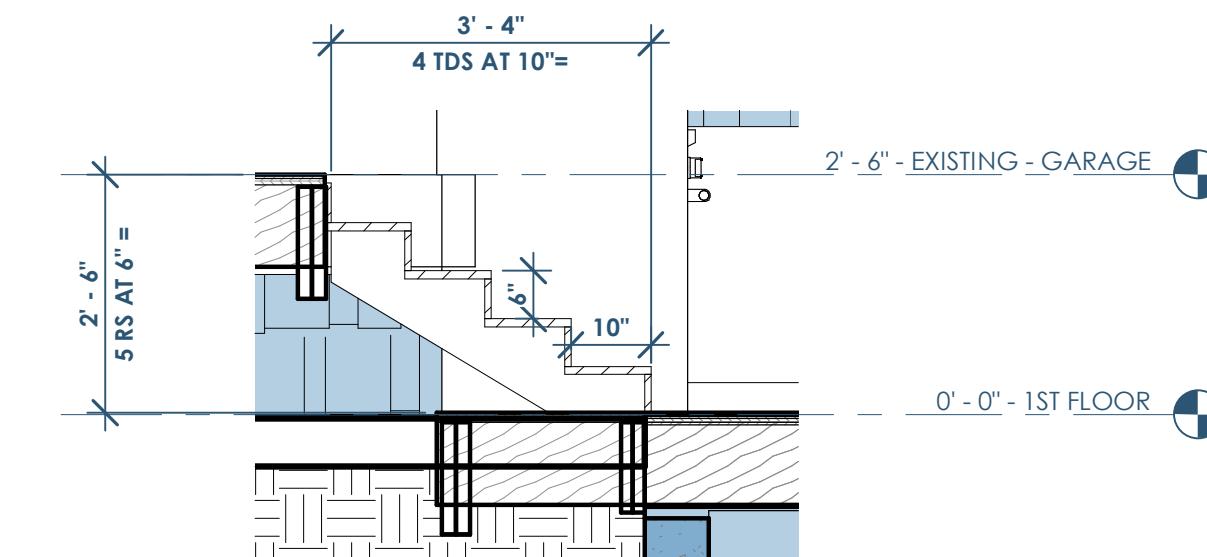

③ STAIR SECTION
1/2" = 1'-0"
0' 1' 2' 4'



Architect: OpeningDesign
316 W Washington Ave | Suite 675
Madison, WI 53703
ryan@openingdesign.com | 773.425.6456

SCHEDULES, DOOR AND WINDOW TYPES - 08/16/2019
KERN RESIDENCE
N6790 SHOREWOOD HILLS RD - LAKE MILLS, WI 53551

A600